

**I N D E X :**

**WORK PORTFOLIO**

**KHAN ASHIYA IQBAL**

**MASJID - ALLAHABAD**

**FAMILY QUARTER - ALLAHABAD**

**SANTOSH MHATRE RESIDENCE - CHIKHALE**




**AUTOFLOW OFFICE - NEW PANVEL**

**SITE VISIT - KARJAT**

**JASNATH MANDIR TRUST**

**HZL INDUSTRY**



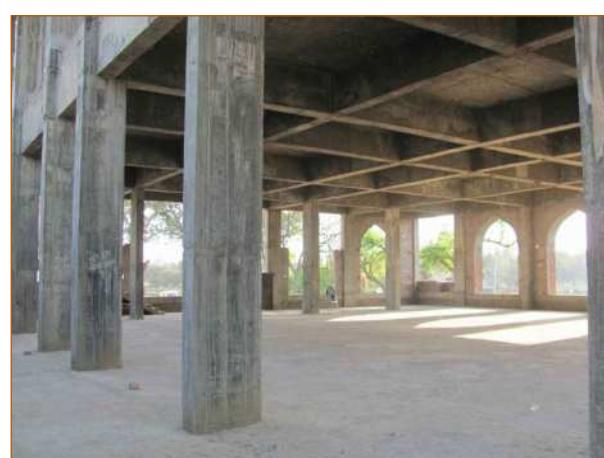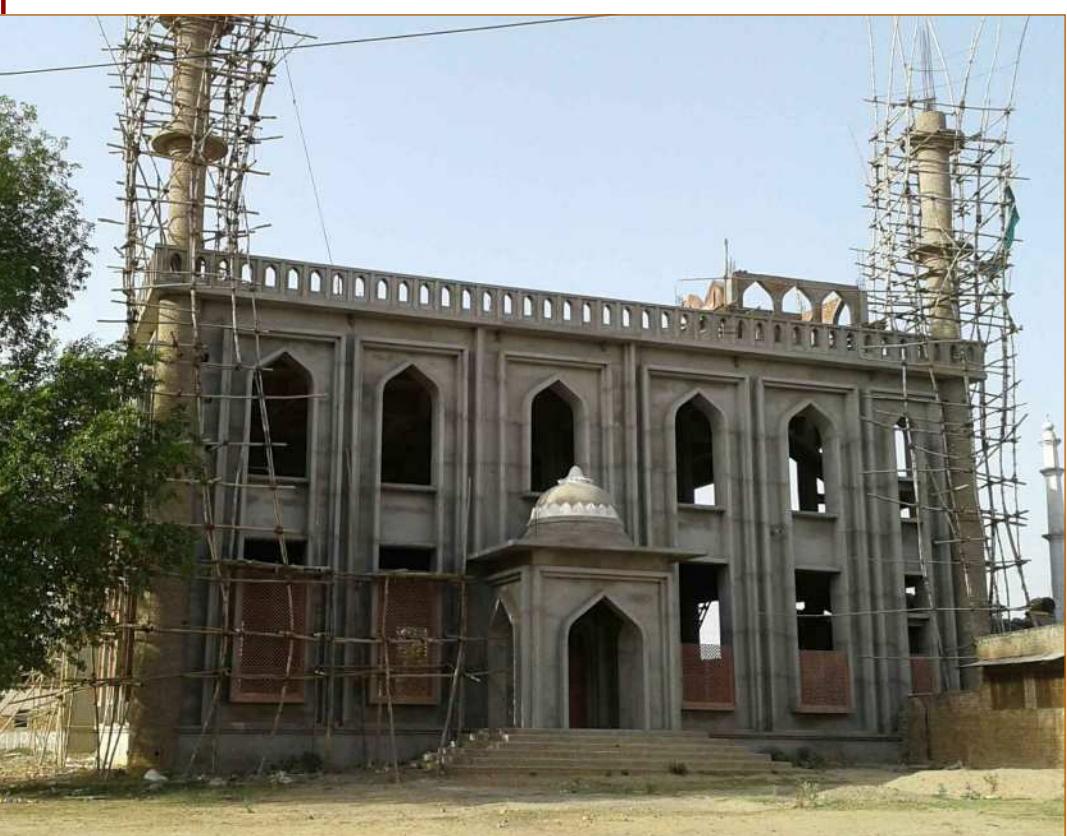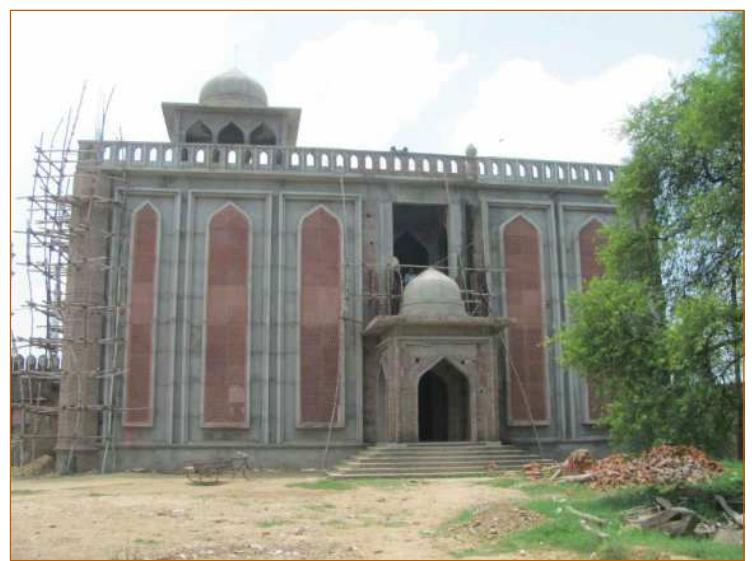

SITE IMAGES - ALLAHBAD




Internal Elevation - North Side




J : Jali / Mesh  
F : Fixed Window  
O : Openable Window

PLAN : CORRIDOR - NORTH SIDE

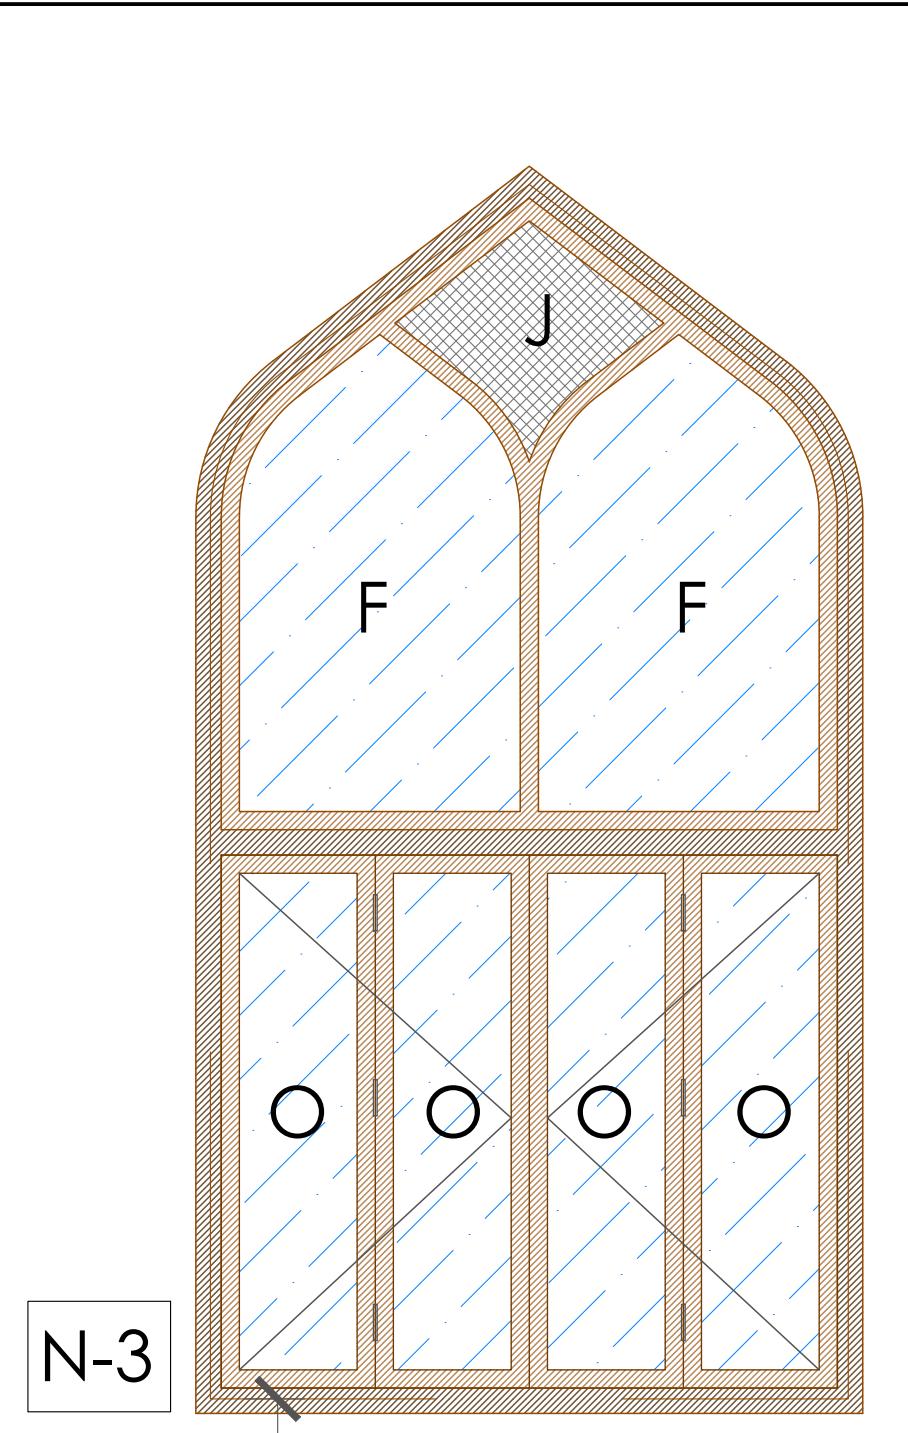


N-3

ELEVATION

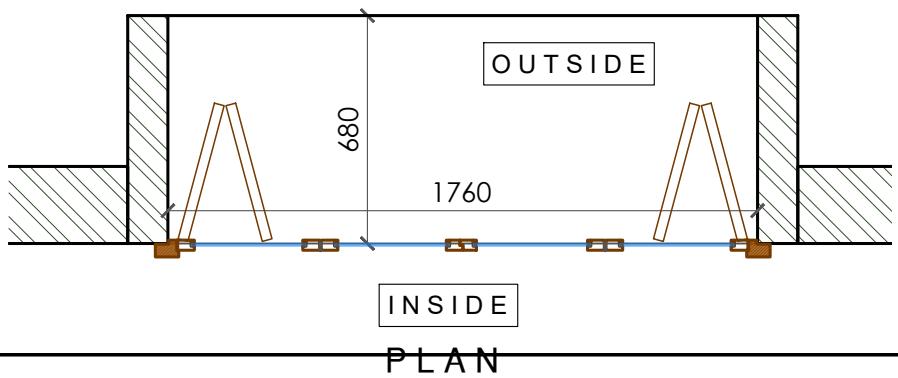


PLAN

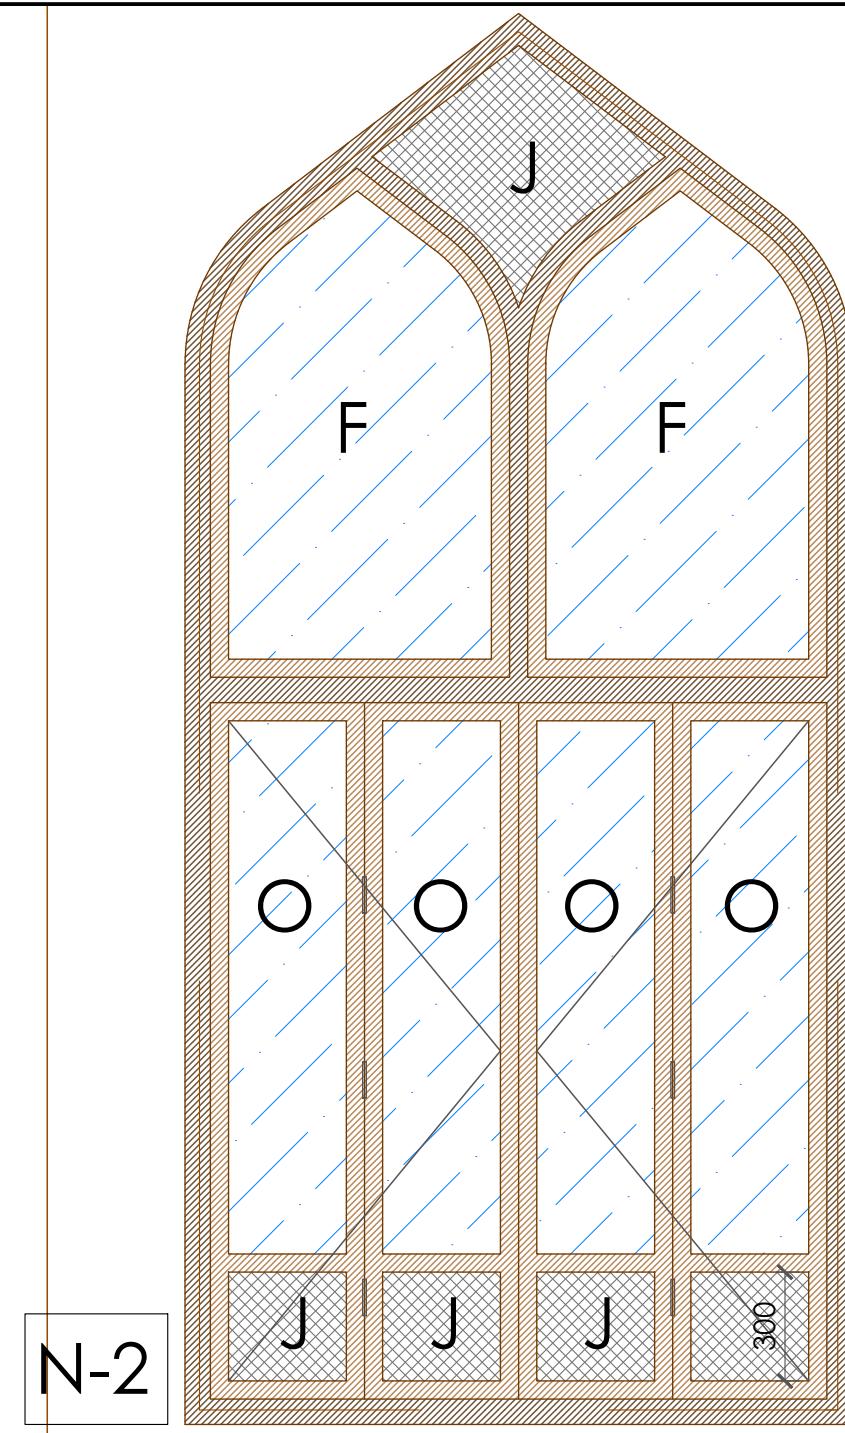


N-2

ELEVATION

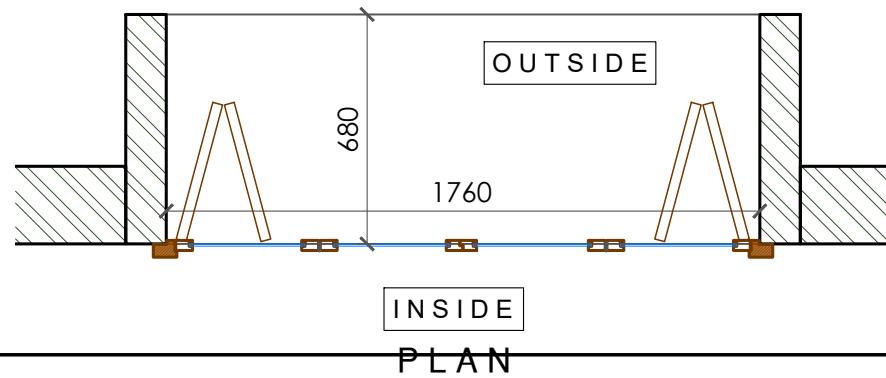


PLAN






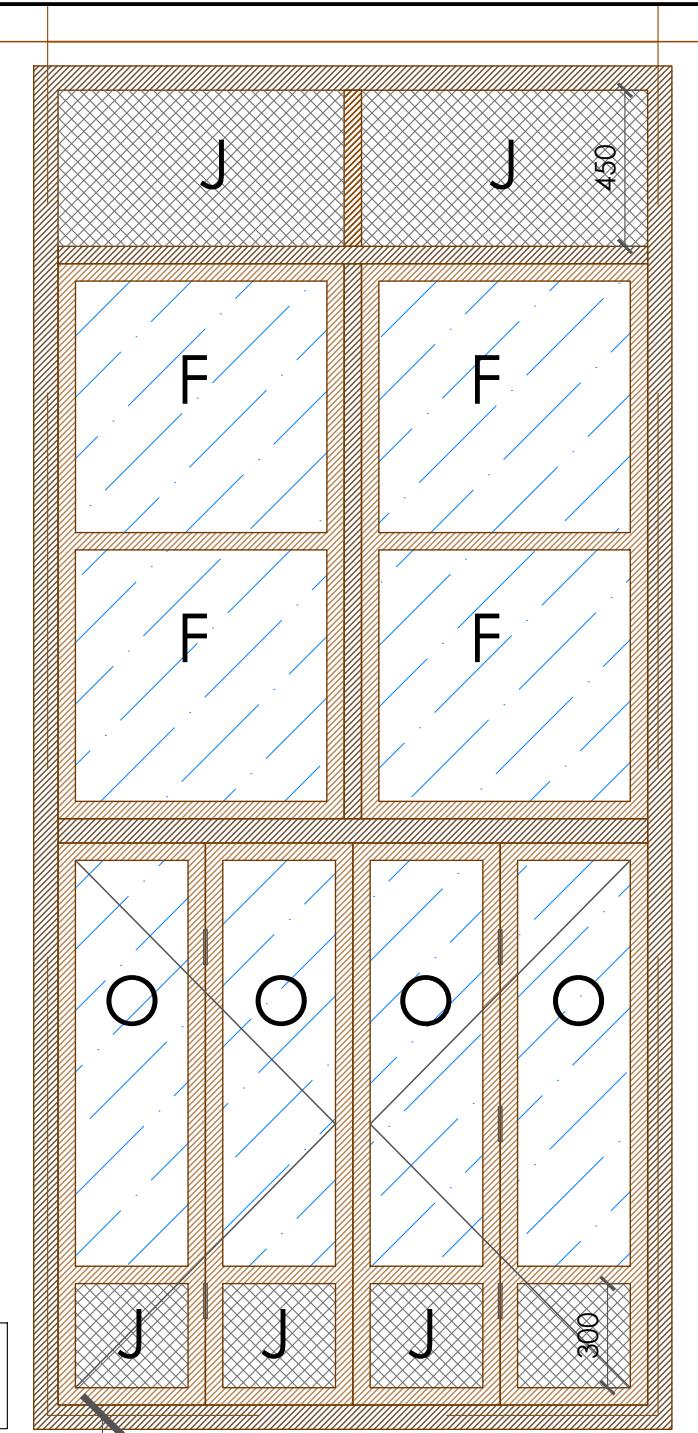


N-1

ELEVATION

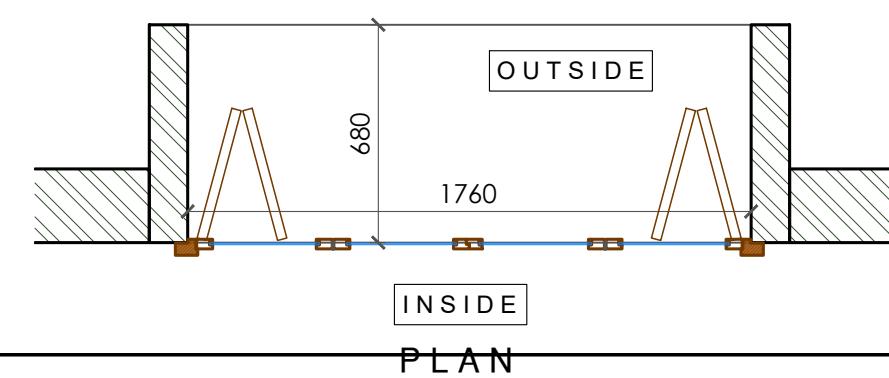


PLAN

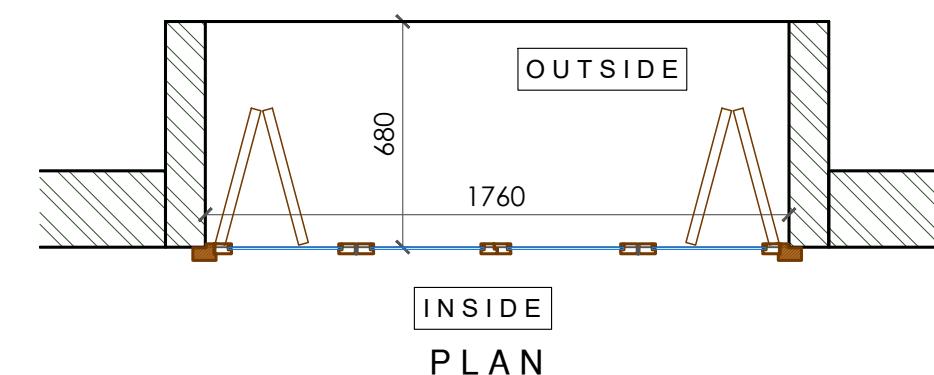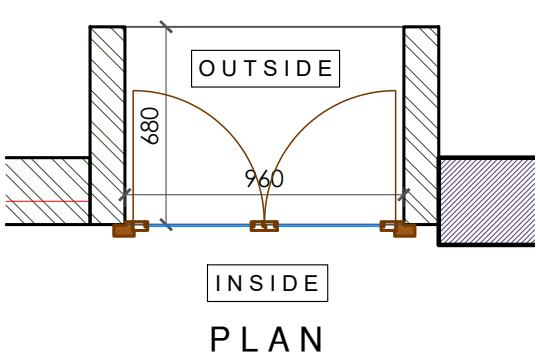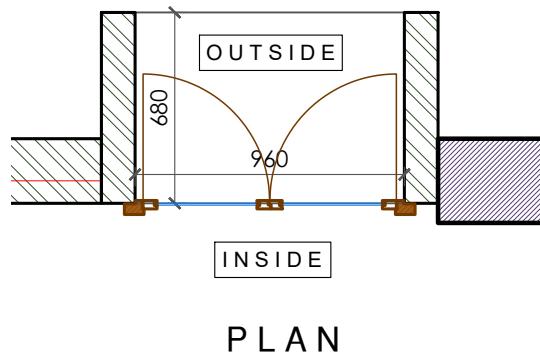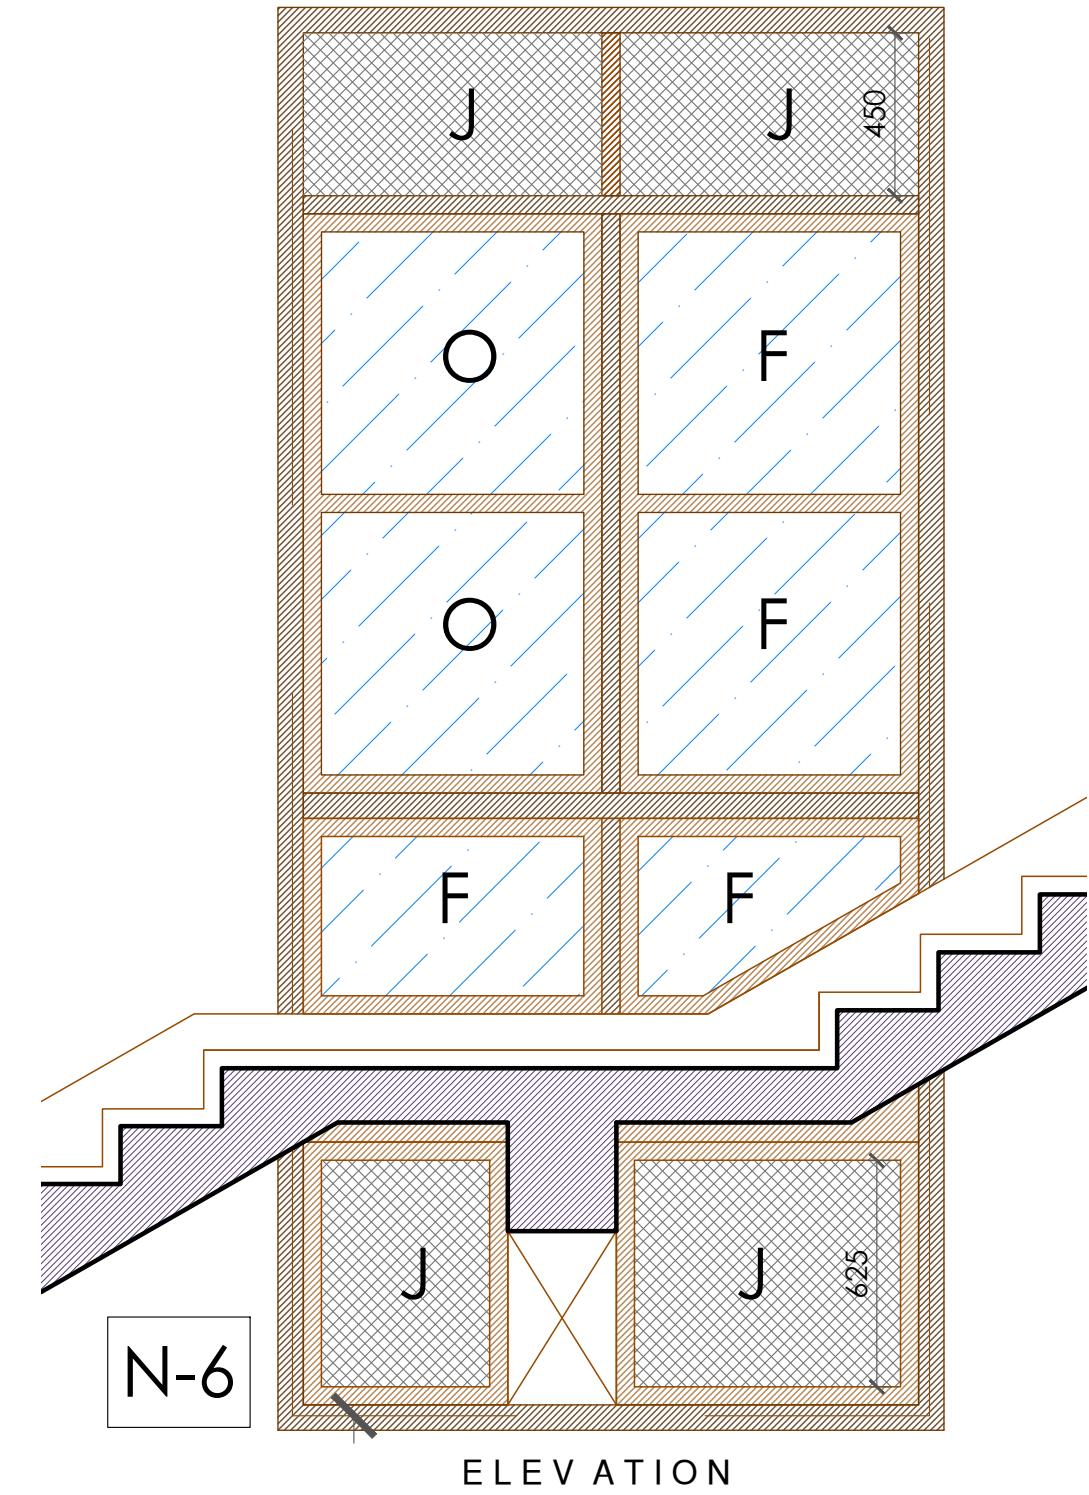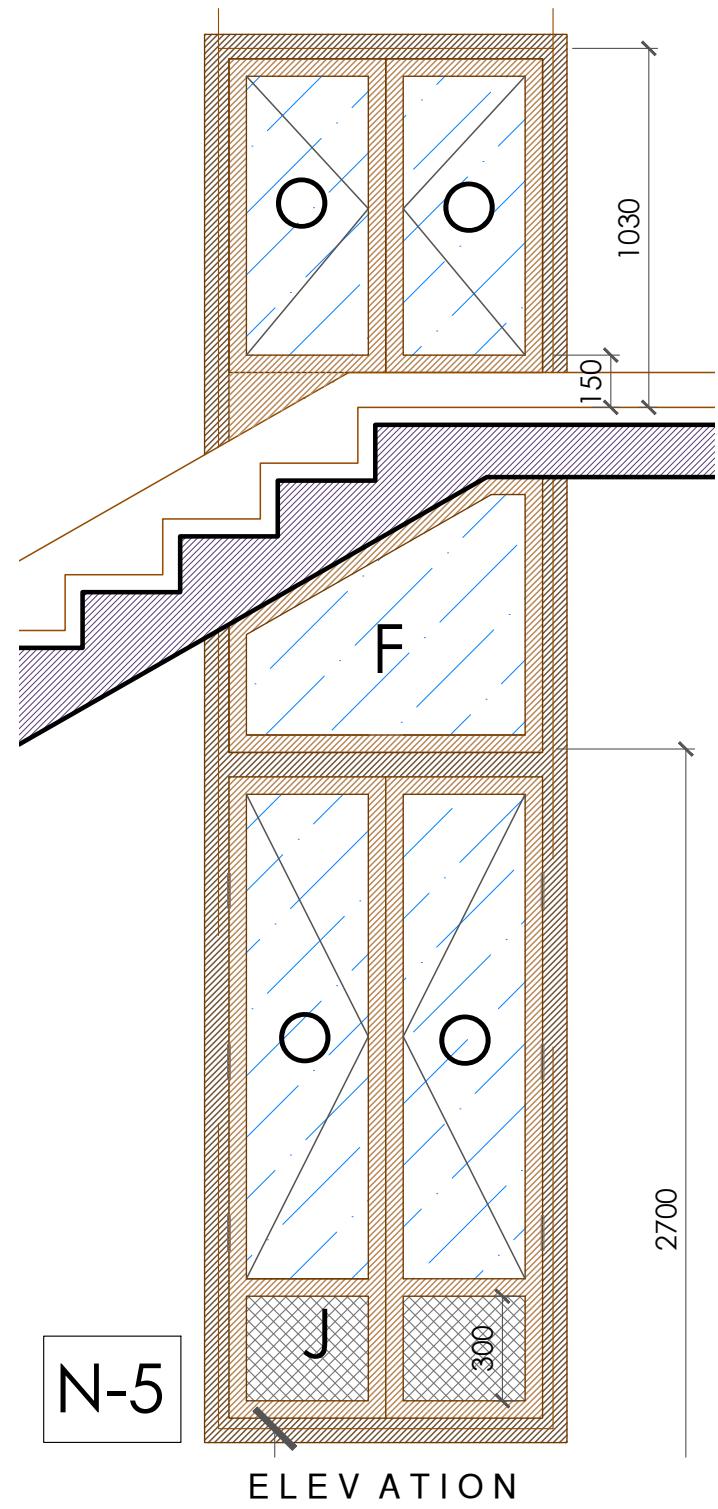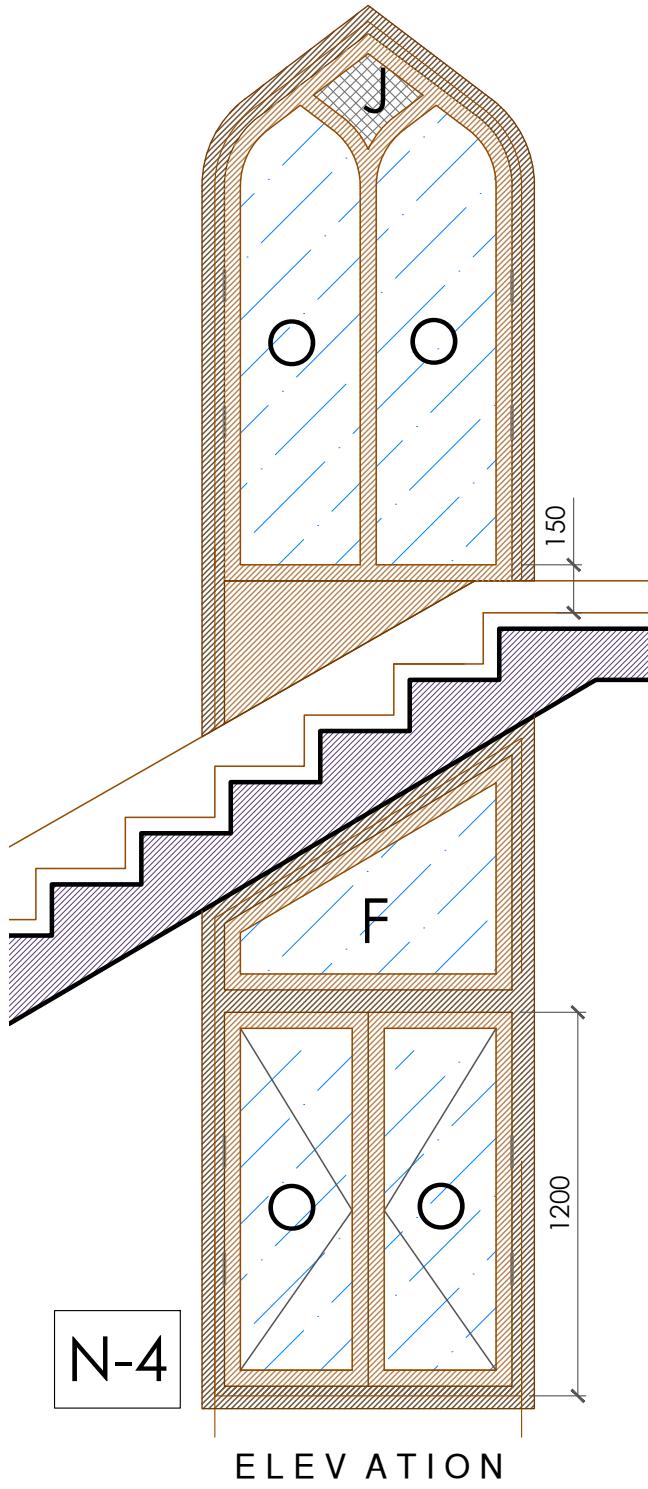









## Internal Elevation - South Side

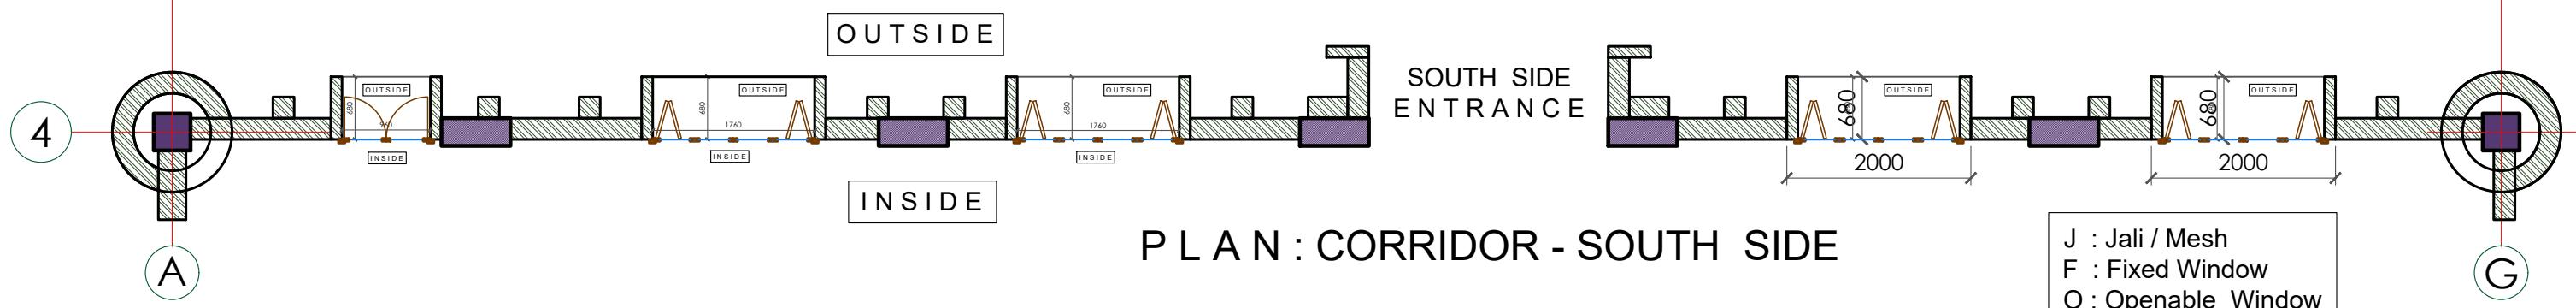

## PLAN : CORRIDOR - SOUTH SIDE

J : Jali / Mesh  
F : Fixed Window  
O : Openable Window


Sheet no.	VISHAL SOLANKI ASSOCIATES svdesign.v@gmail.com   09920351604	Internal Corridor Elevation : South Side Sayed Saraon Dargah Masjid - Allahabad	Stamp	Sign Type
-----------	---	--	-------	-----------

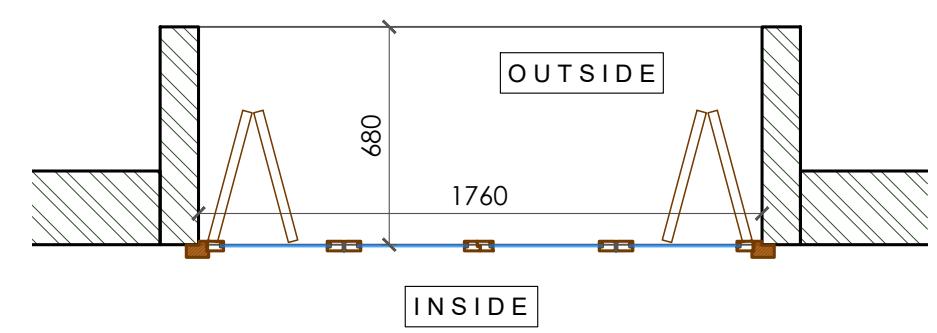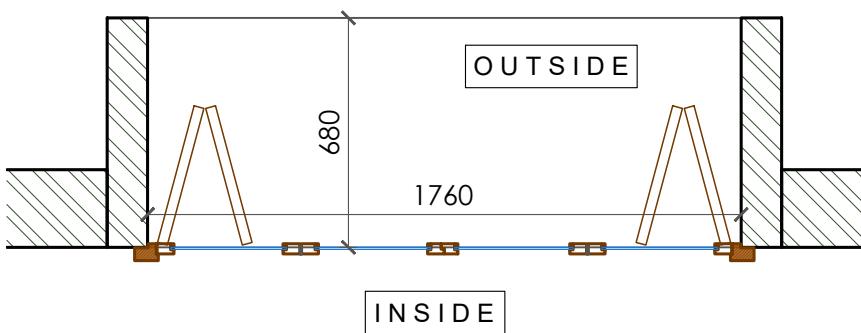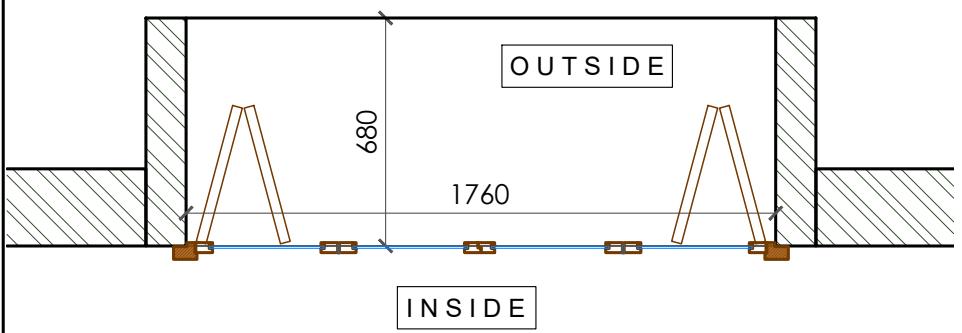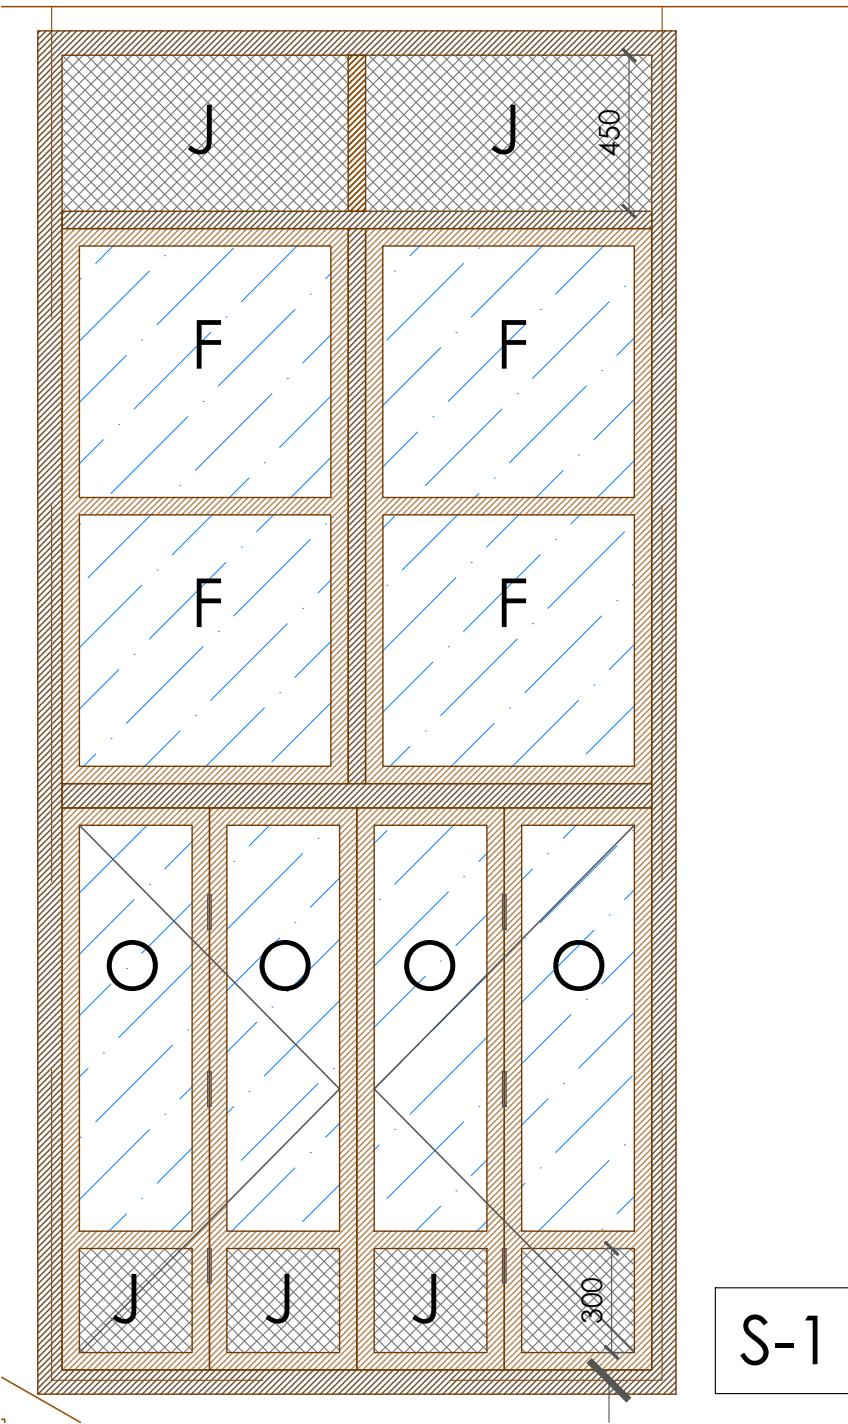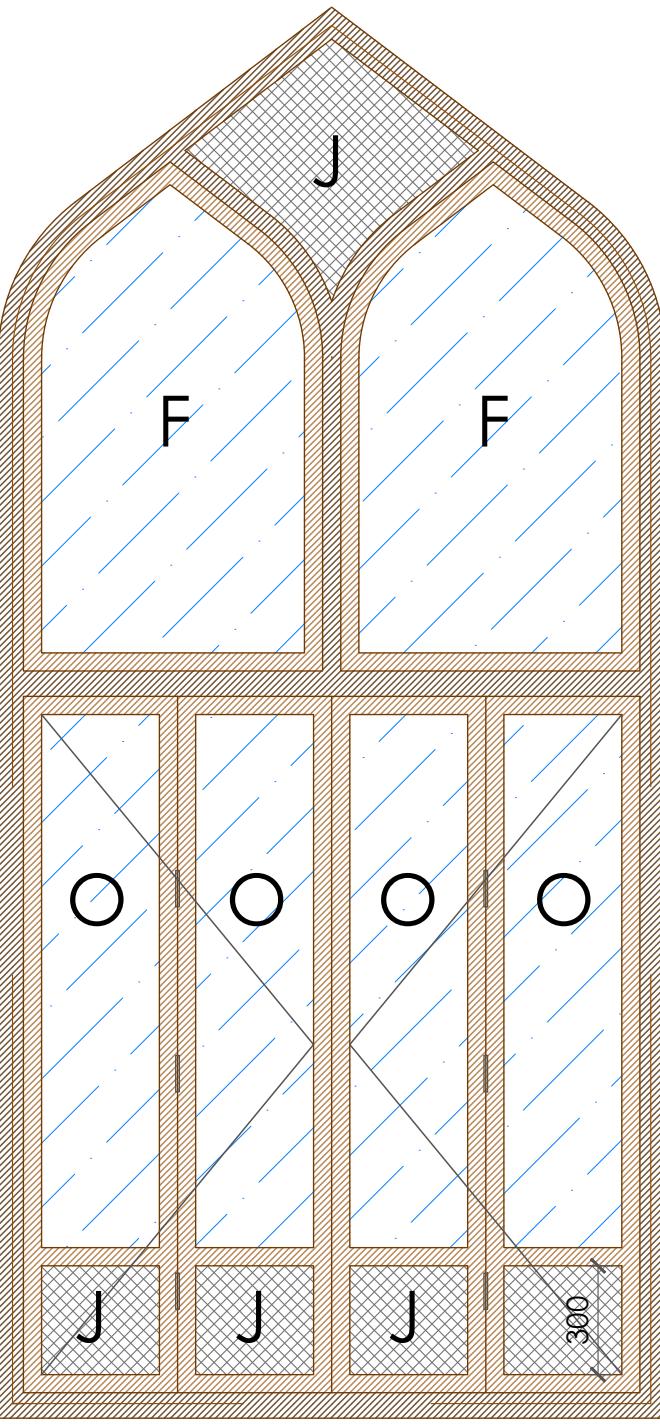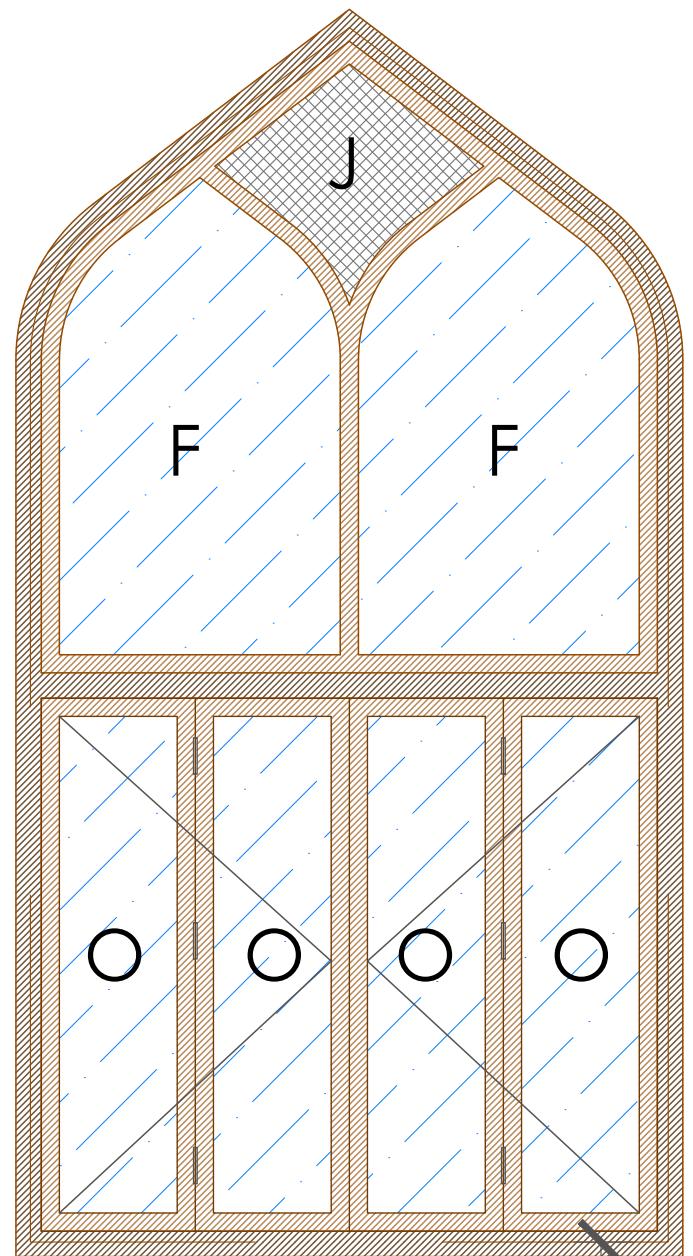

PLAN


PLAN

PLAN

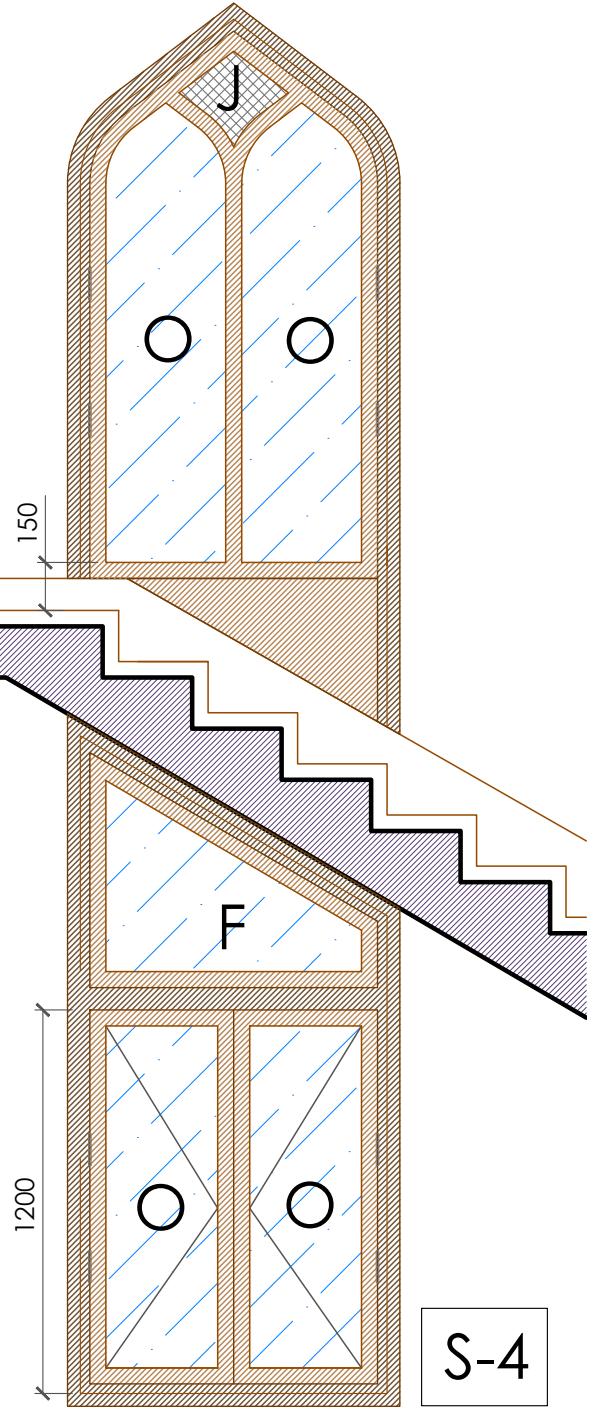


ELEVATION

S-4

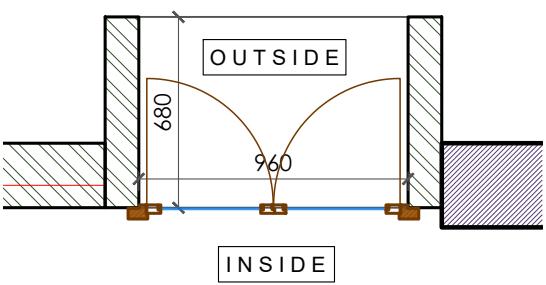


PLAN

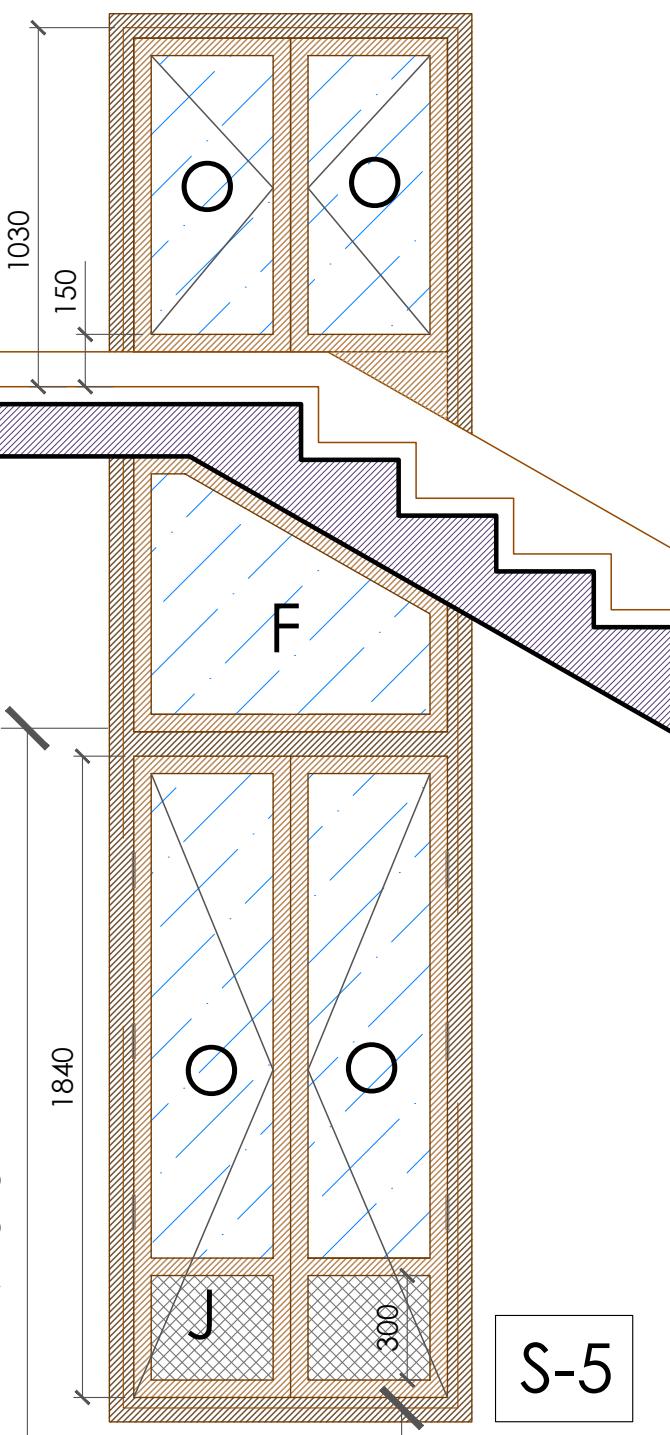


ELEVATION

S-5

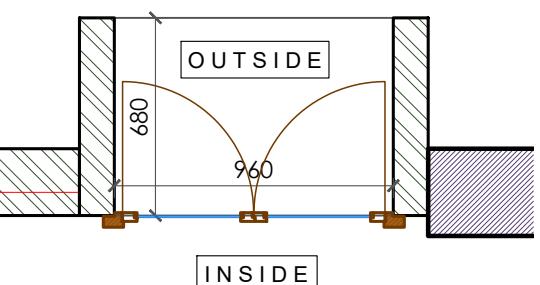


PLAN

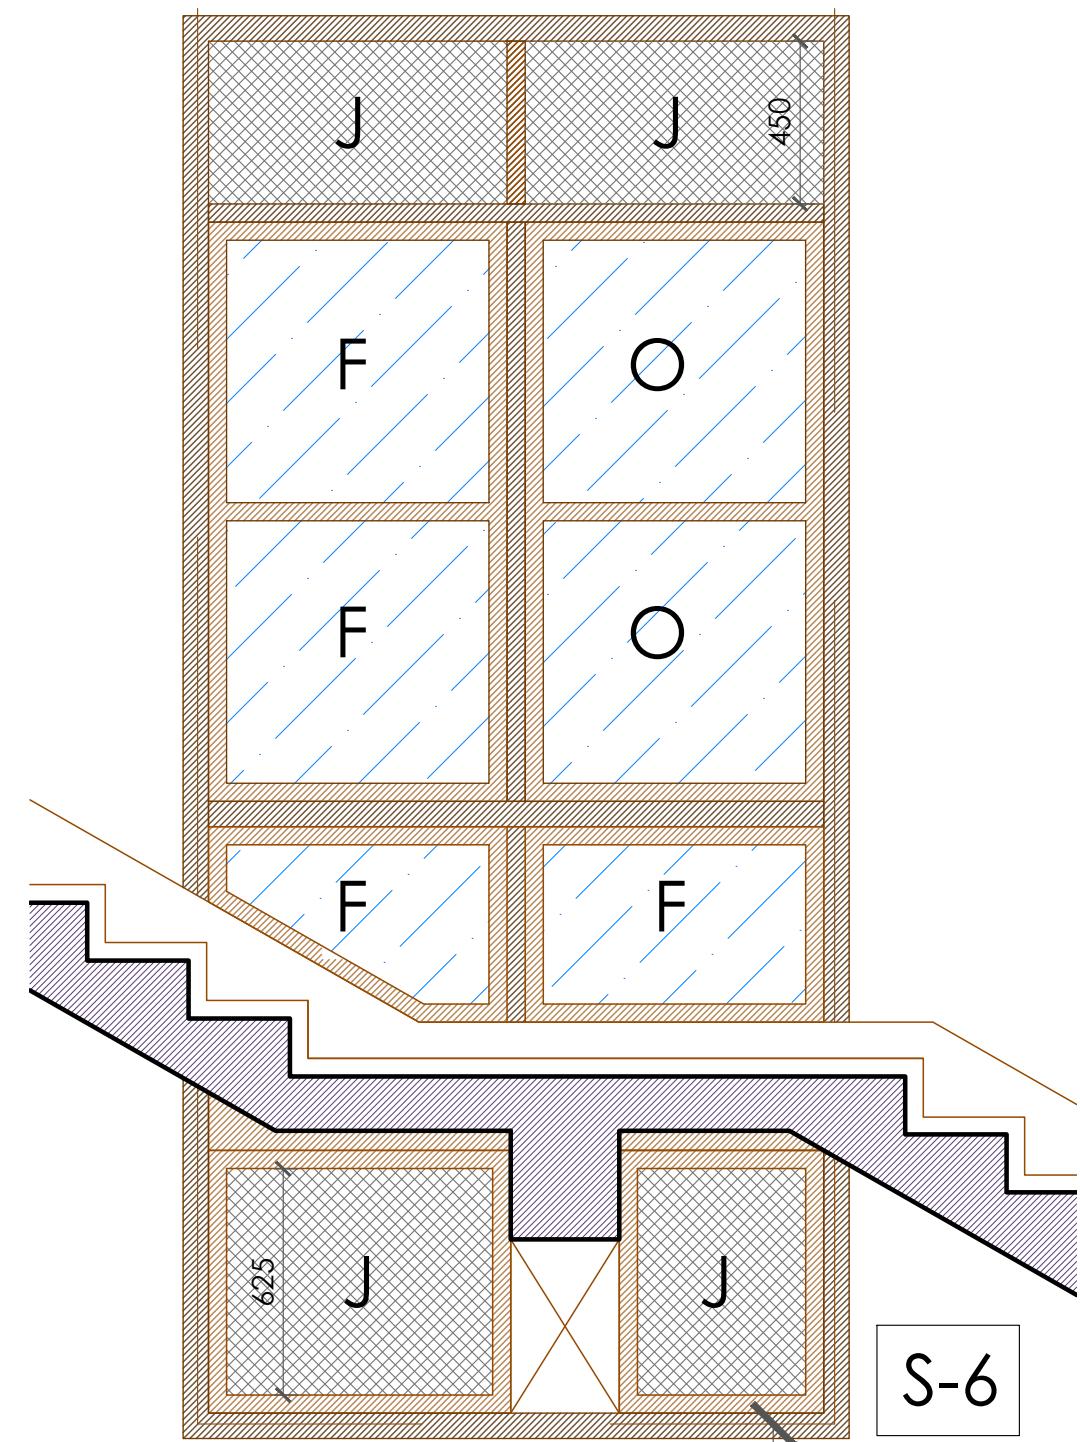


ELEVATION

S-6

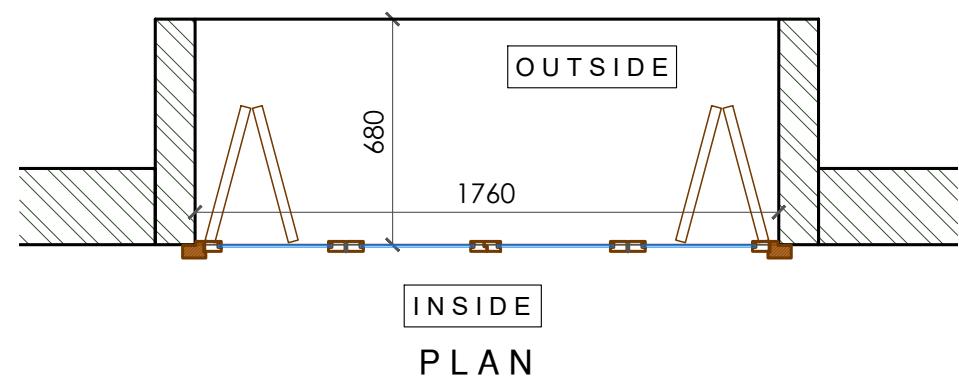

PLAN



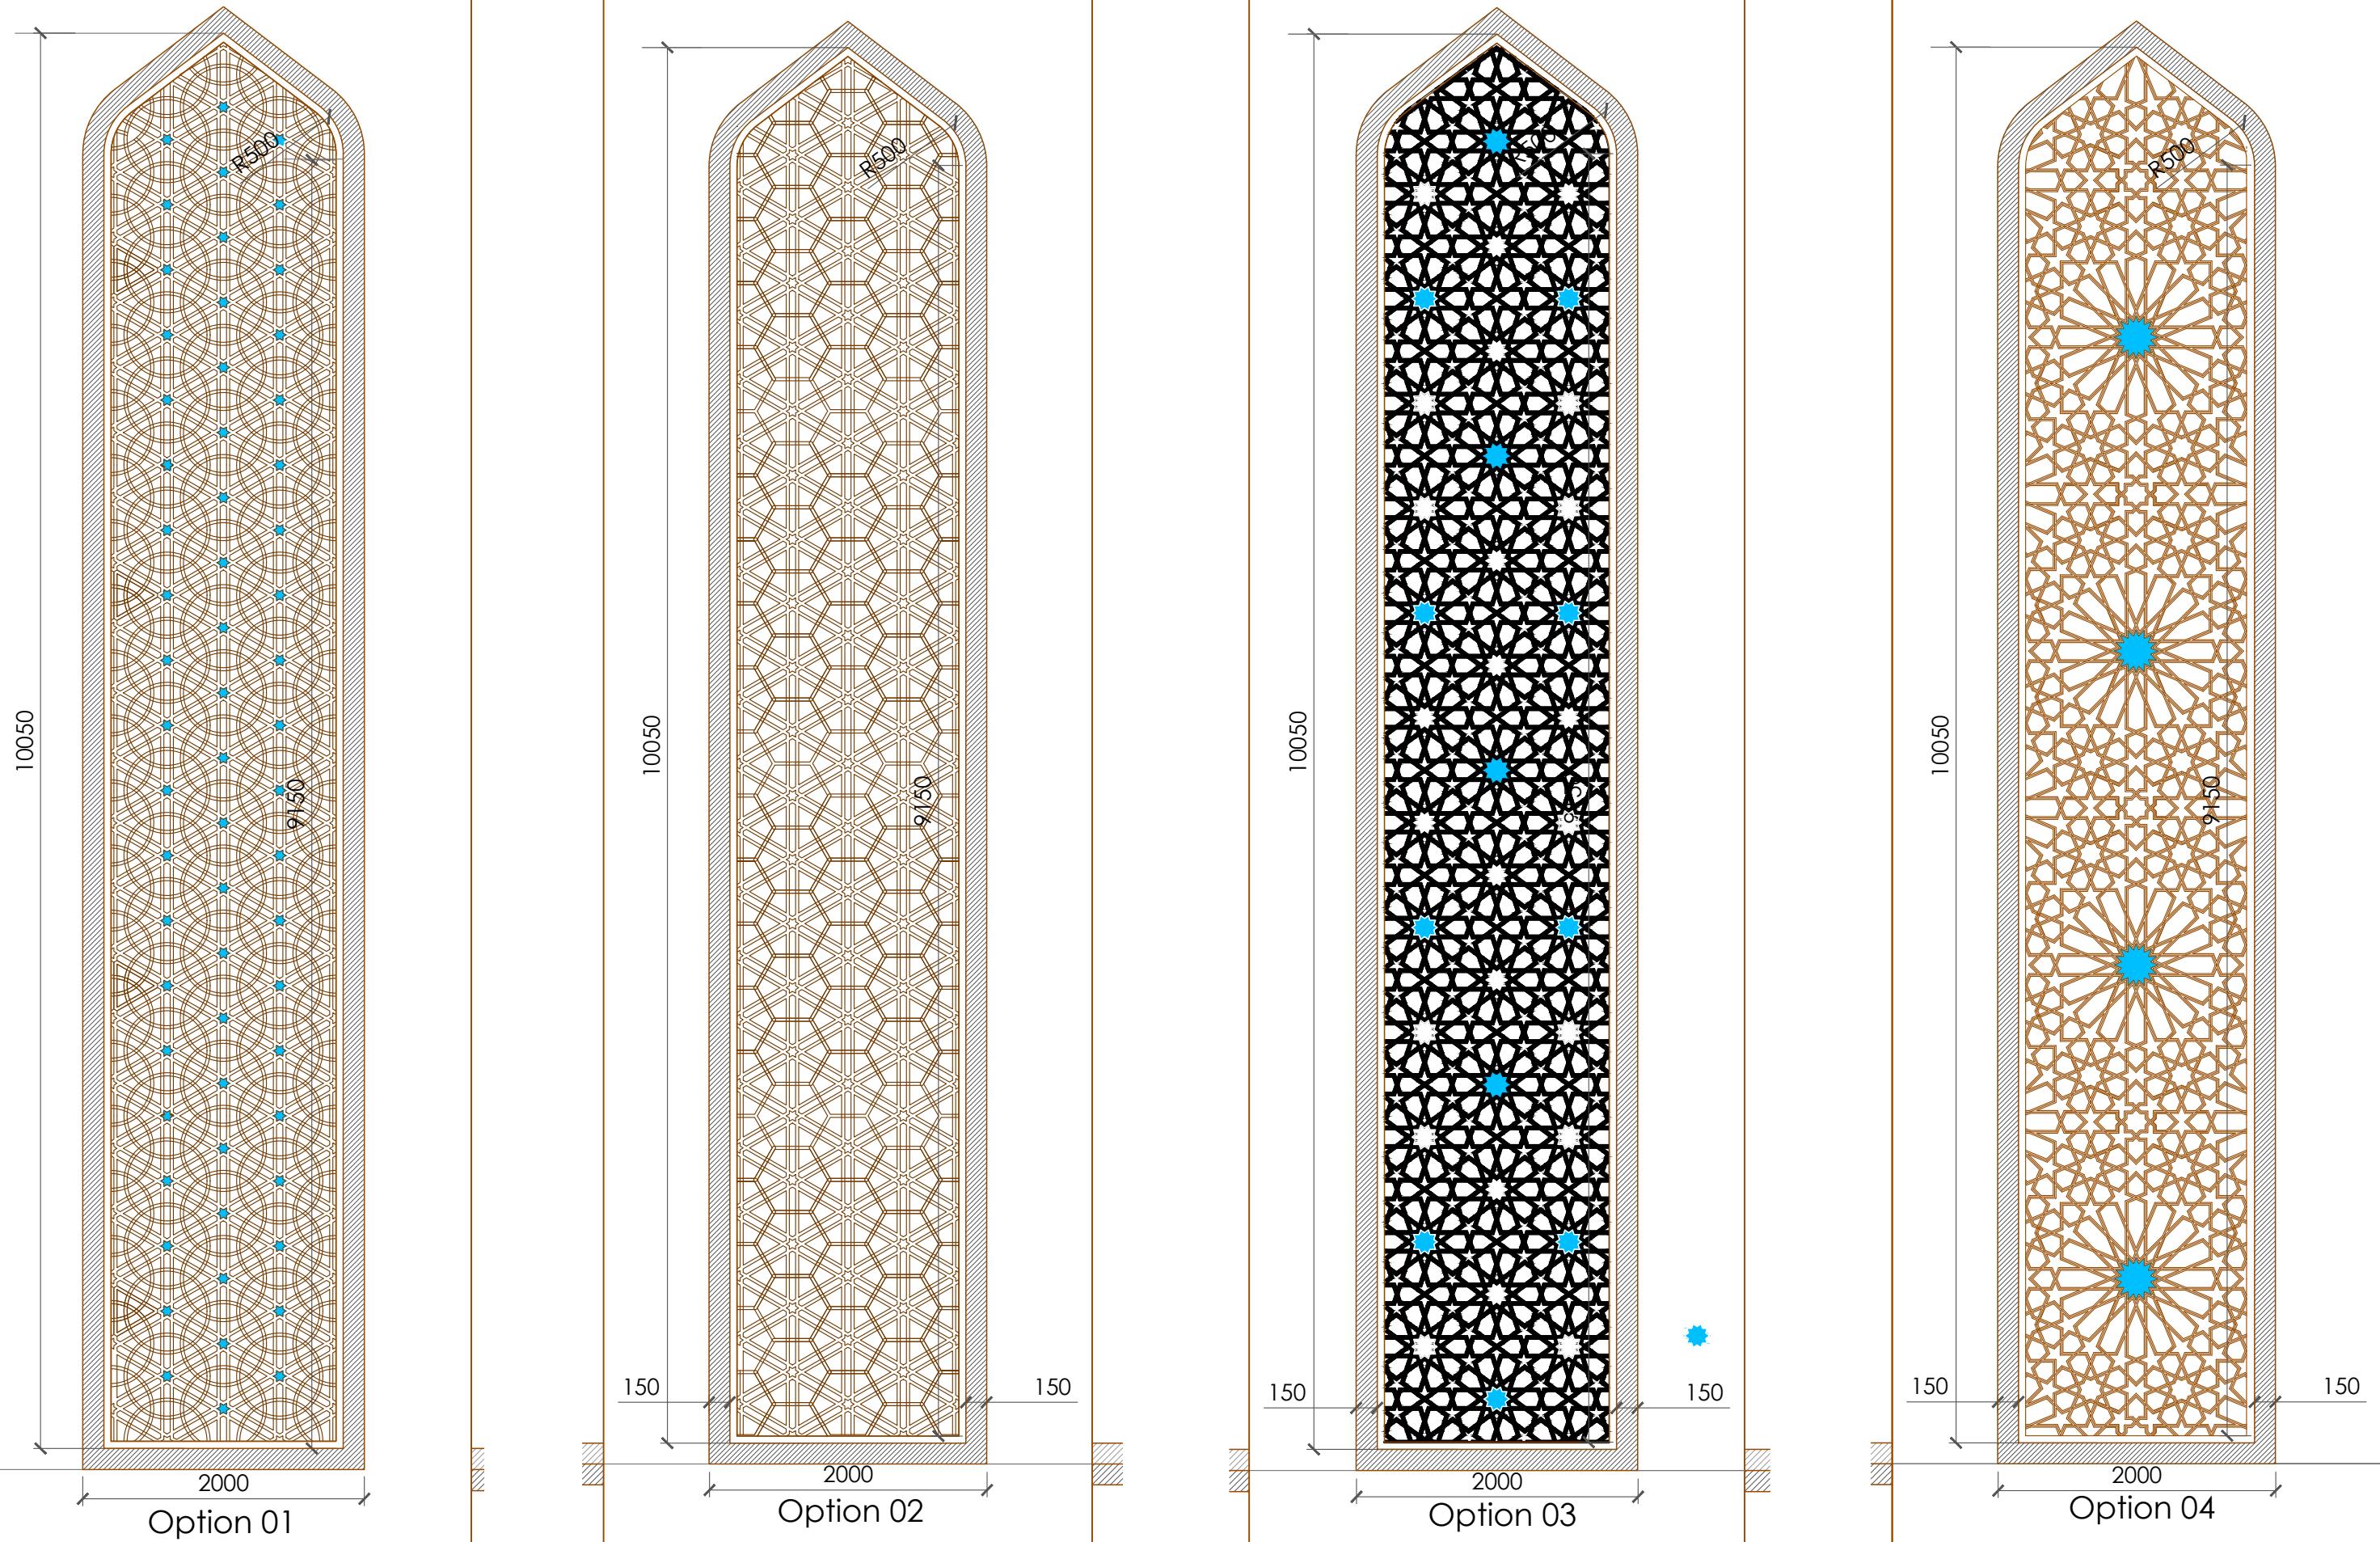

Sheet no.

VISHAL SOLANKI ASSOCIATES

svdesign.v@gmail.com | 09920351604


External Elevation : West Side. (Qibla wall)


Sayed Saroan Dargah Masjid - Allahabad

Stamp \_\_\_\_\_

Sign \_\_\_\_\_

Type G.A

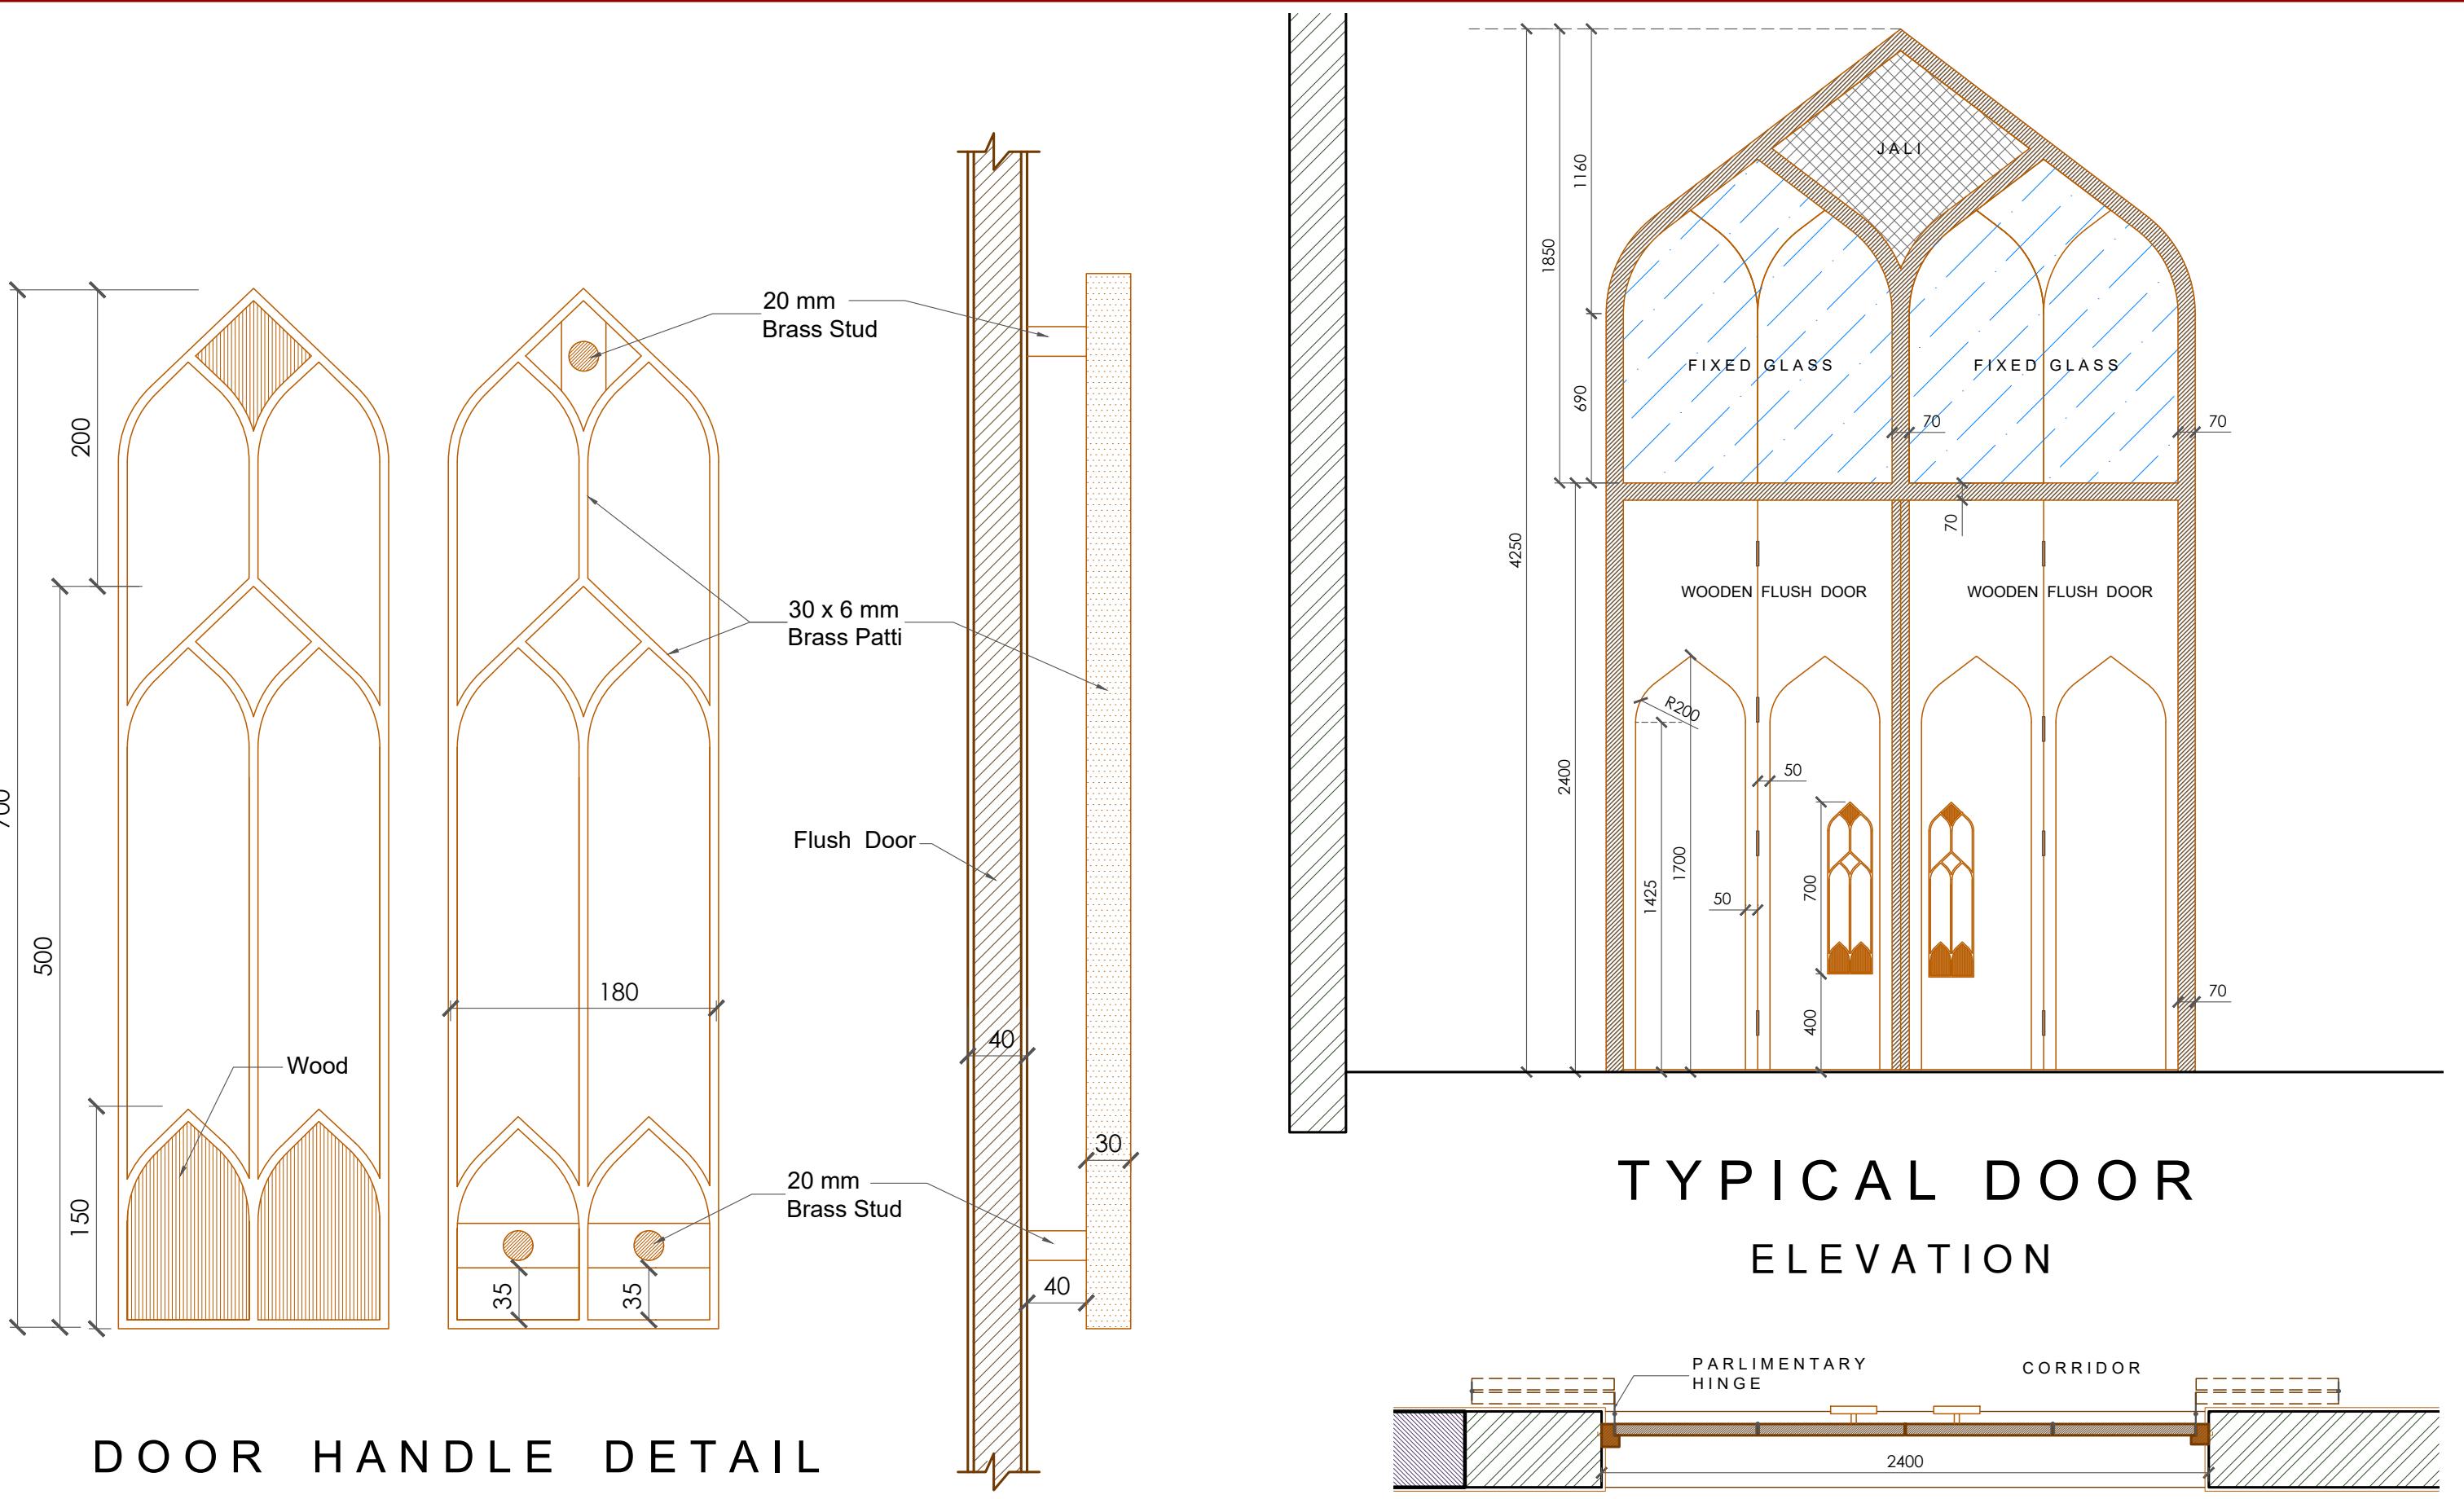

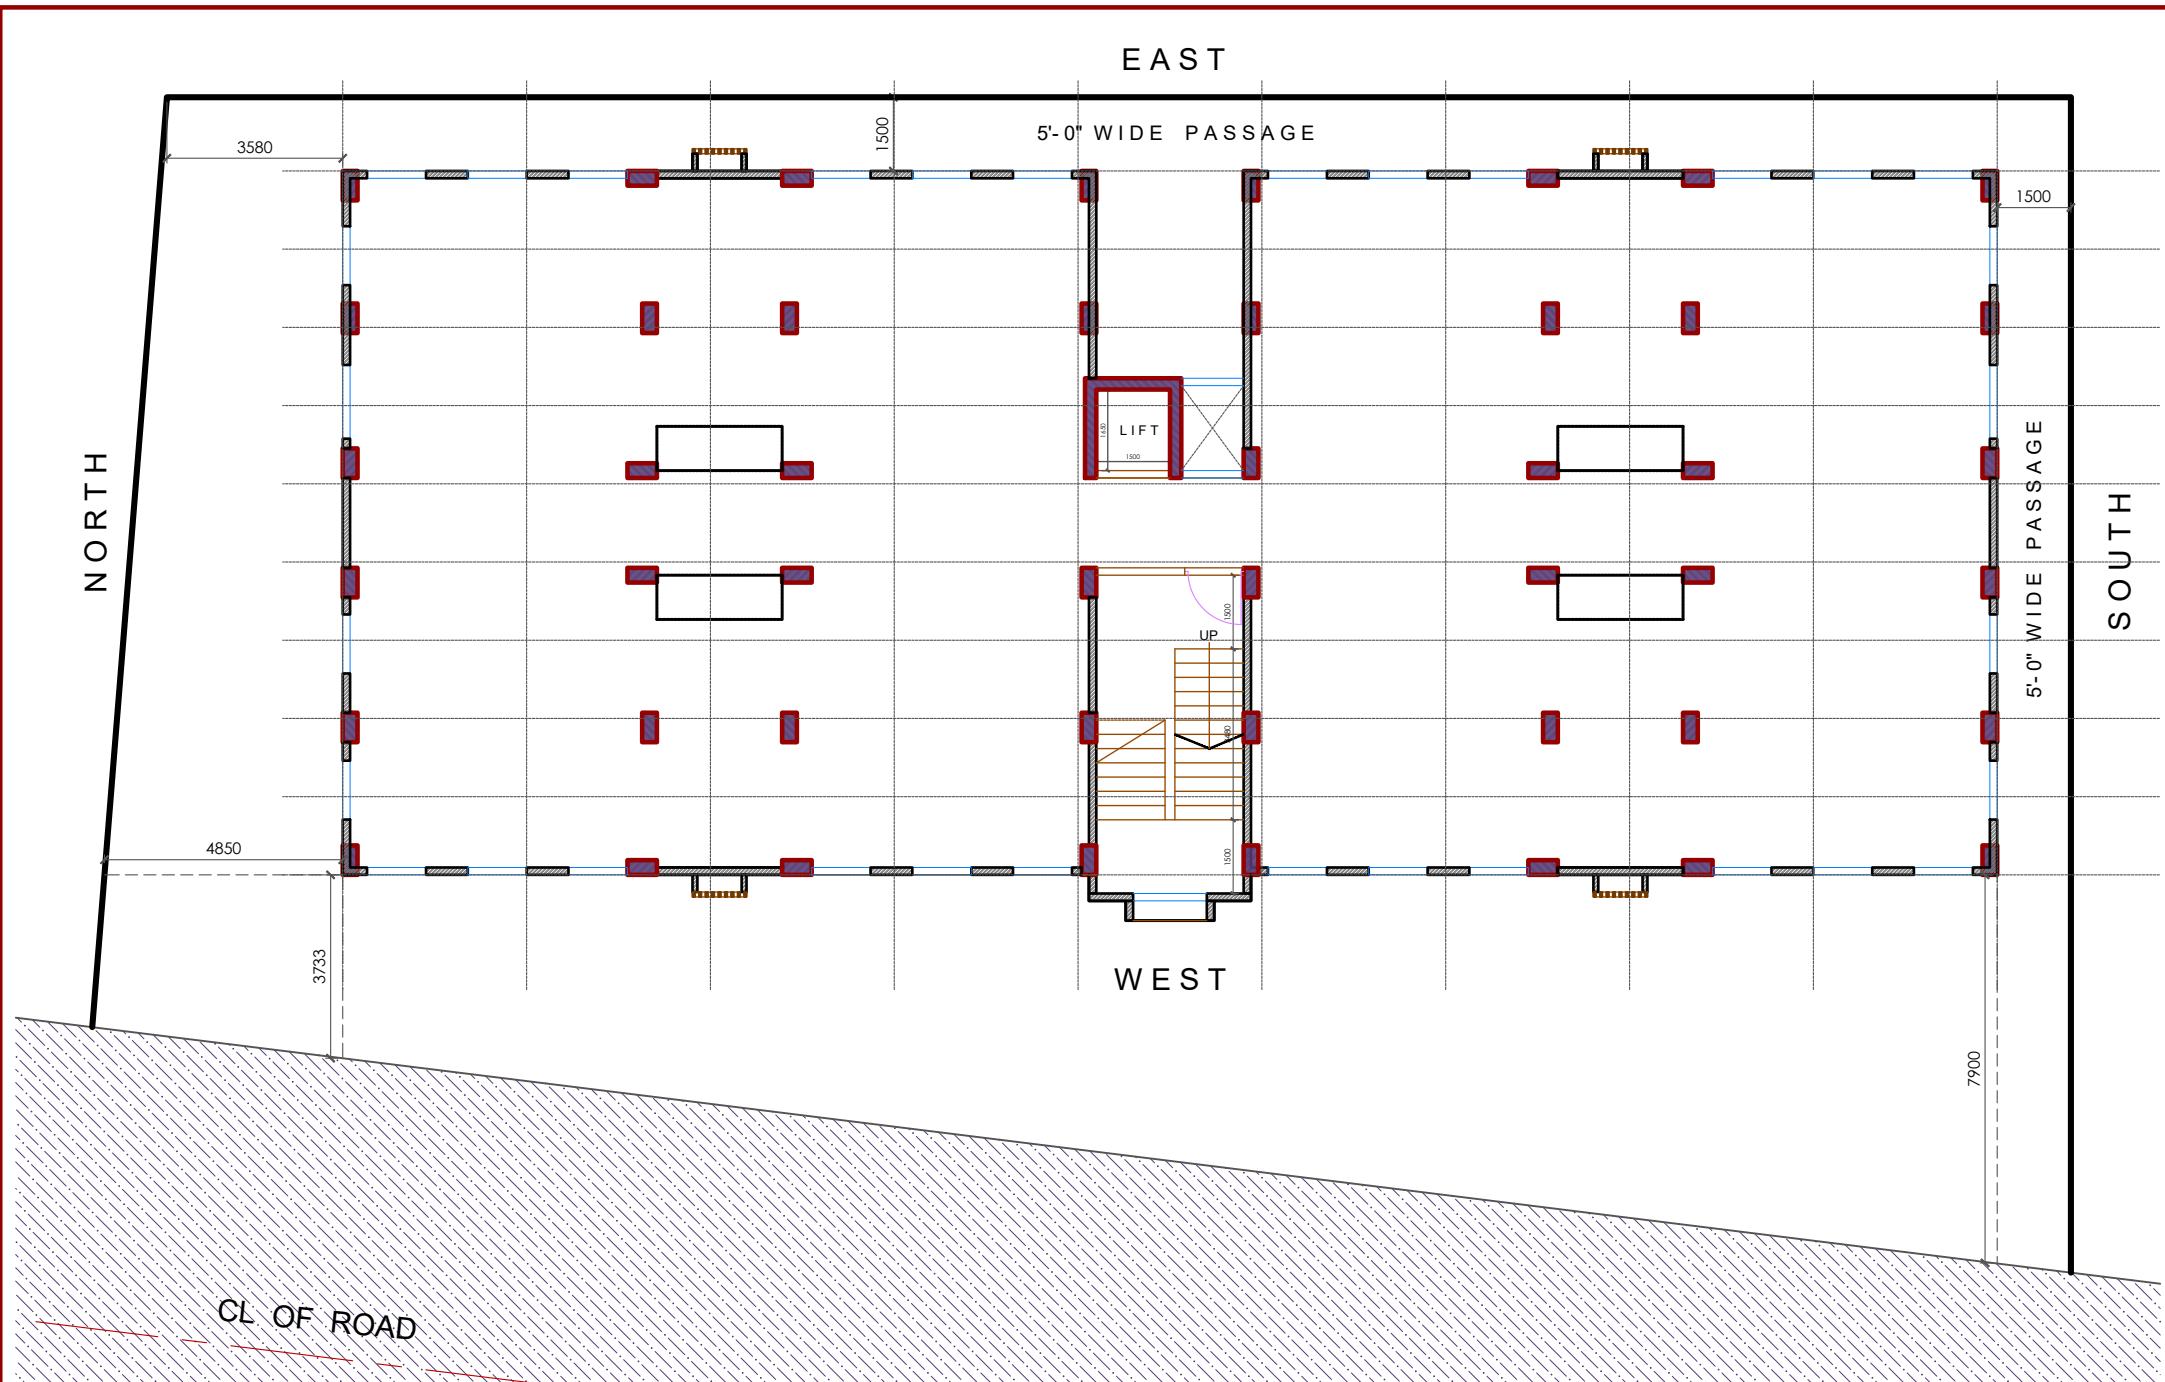

Sayed Saraon Dargah Masjid - Allahabad


VISHAL SOLANKI ASSOCIATES

Site Layout Plan



No Type GA Dwg Rev


No FQ.MP.01 Date 10-11-2019

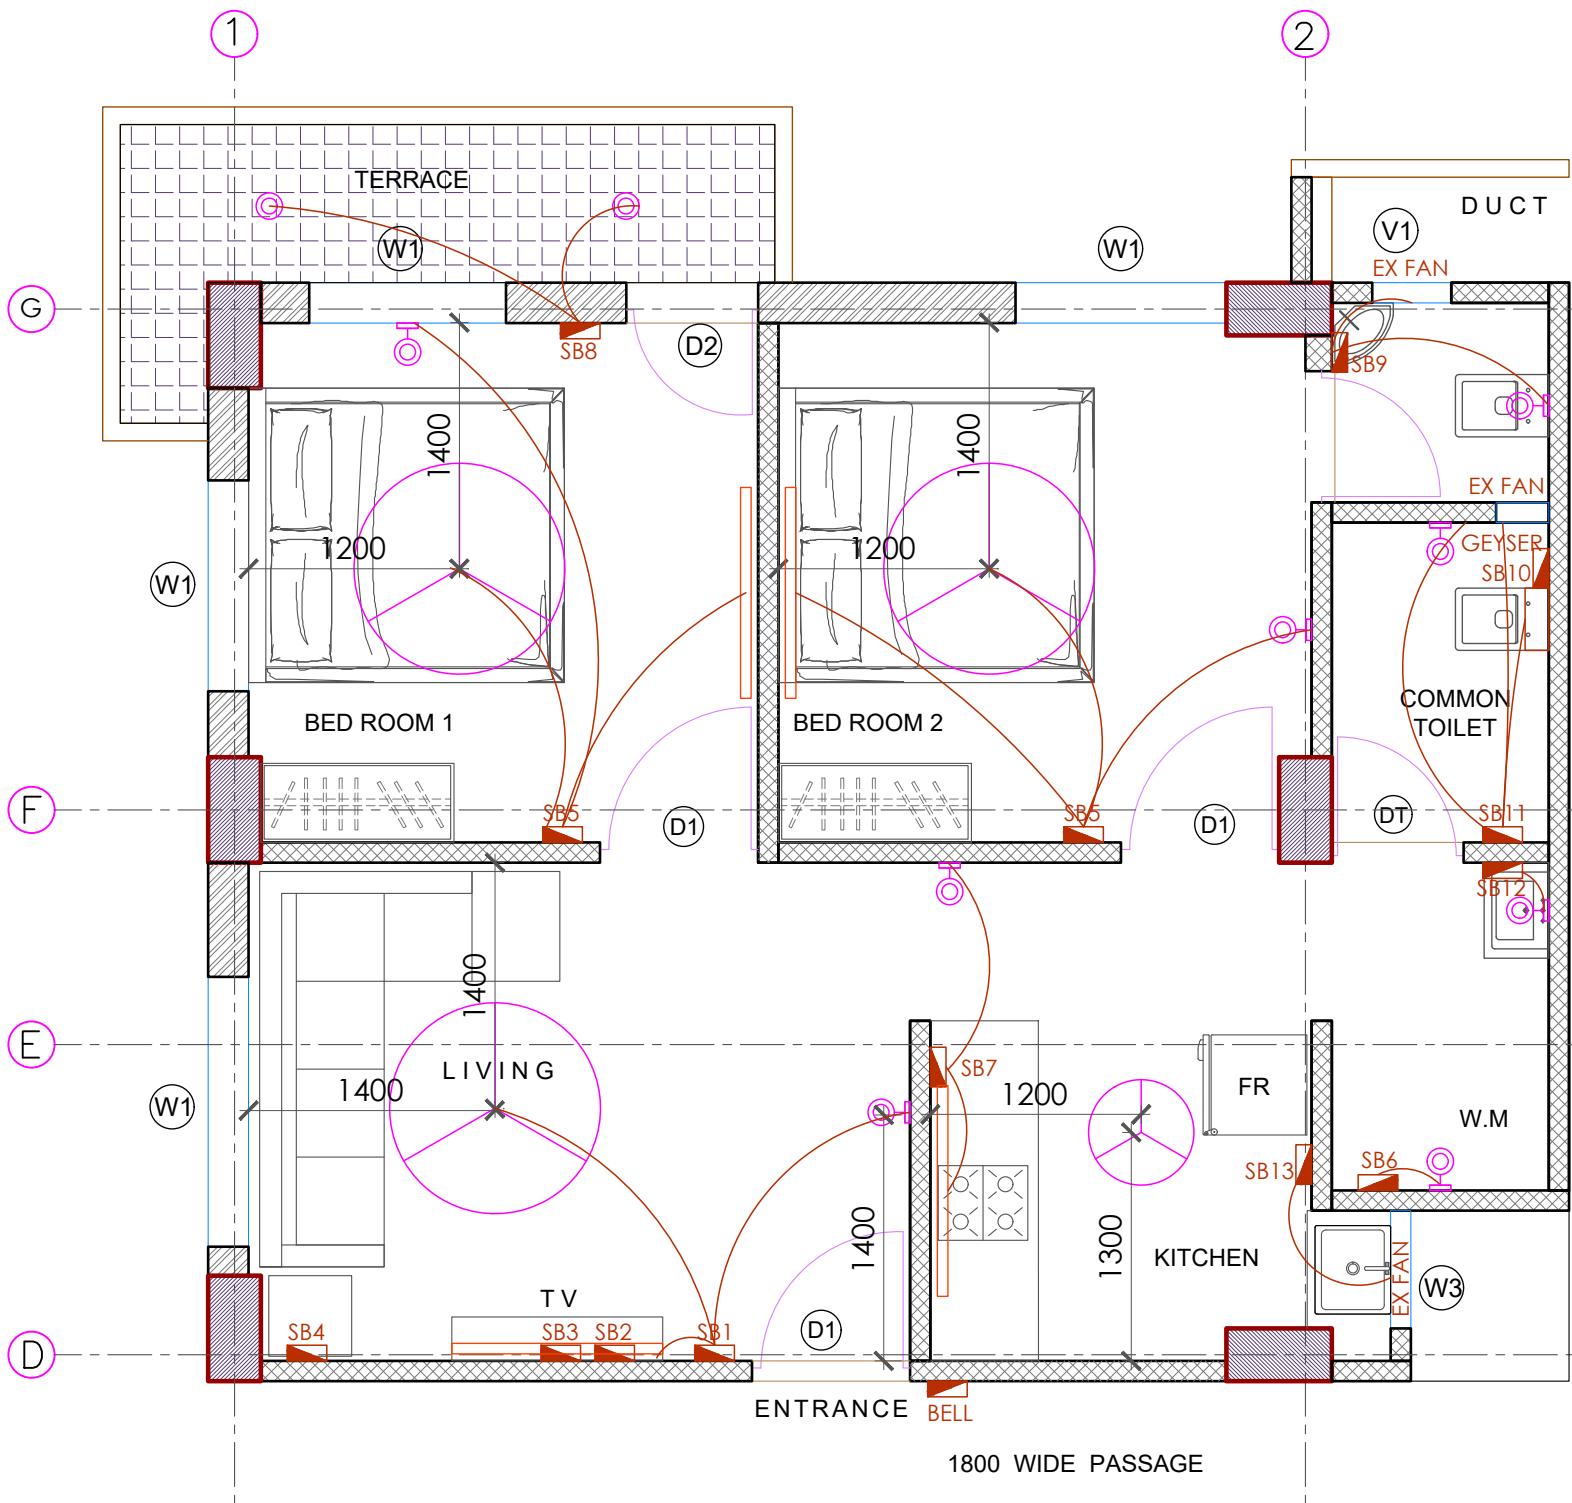


SYMBOL	PLATE	HEIGHT FROM FFL
SB1	(12 Module)	1500 mm
SB2	(8 Model)	600 mm
SB3	TV (2 Model)	1200 mm
SB4	(6 Module)	750 mm
SB 5	(8 Model)	1500 mm
SB 6	WASHING MACHINE 16 A (3 Model)	1500 mm
SB 7	16 A (12 Module)	1500 mm
SB 8	(6 Model)	1500 mm

SYMBOL	PLATE	HEIGHT FROM FFL
SB 9	(2 Model)	1500 mm
SB10	GEYSER 16 A (2 Model)	2200 mm
SB11	(4 Model)	1500 mm
SB12	(4 Model)	1500 mm
SB 13	FRIDGE 16 A (3 Model)	1500 mm
SB G1	(8 Model)	1500 mm
SB G2	(8 Model)	1500 mm

4' TUBE LIGHT	2200 mm
BULB HOLDER	At Slab Bottom
BULB HOLDER	2200 mm

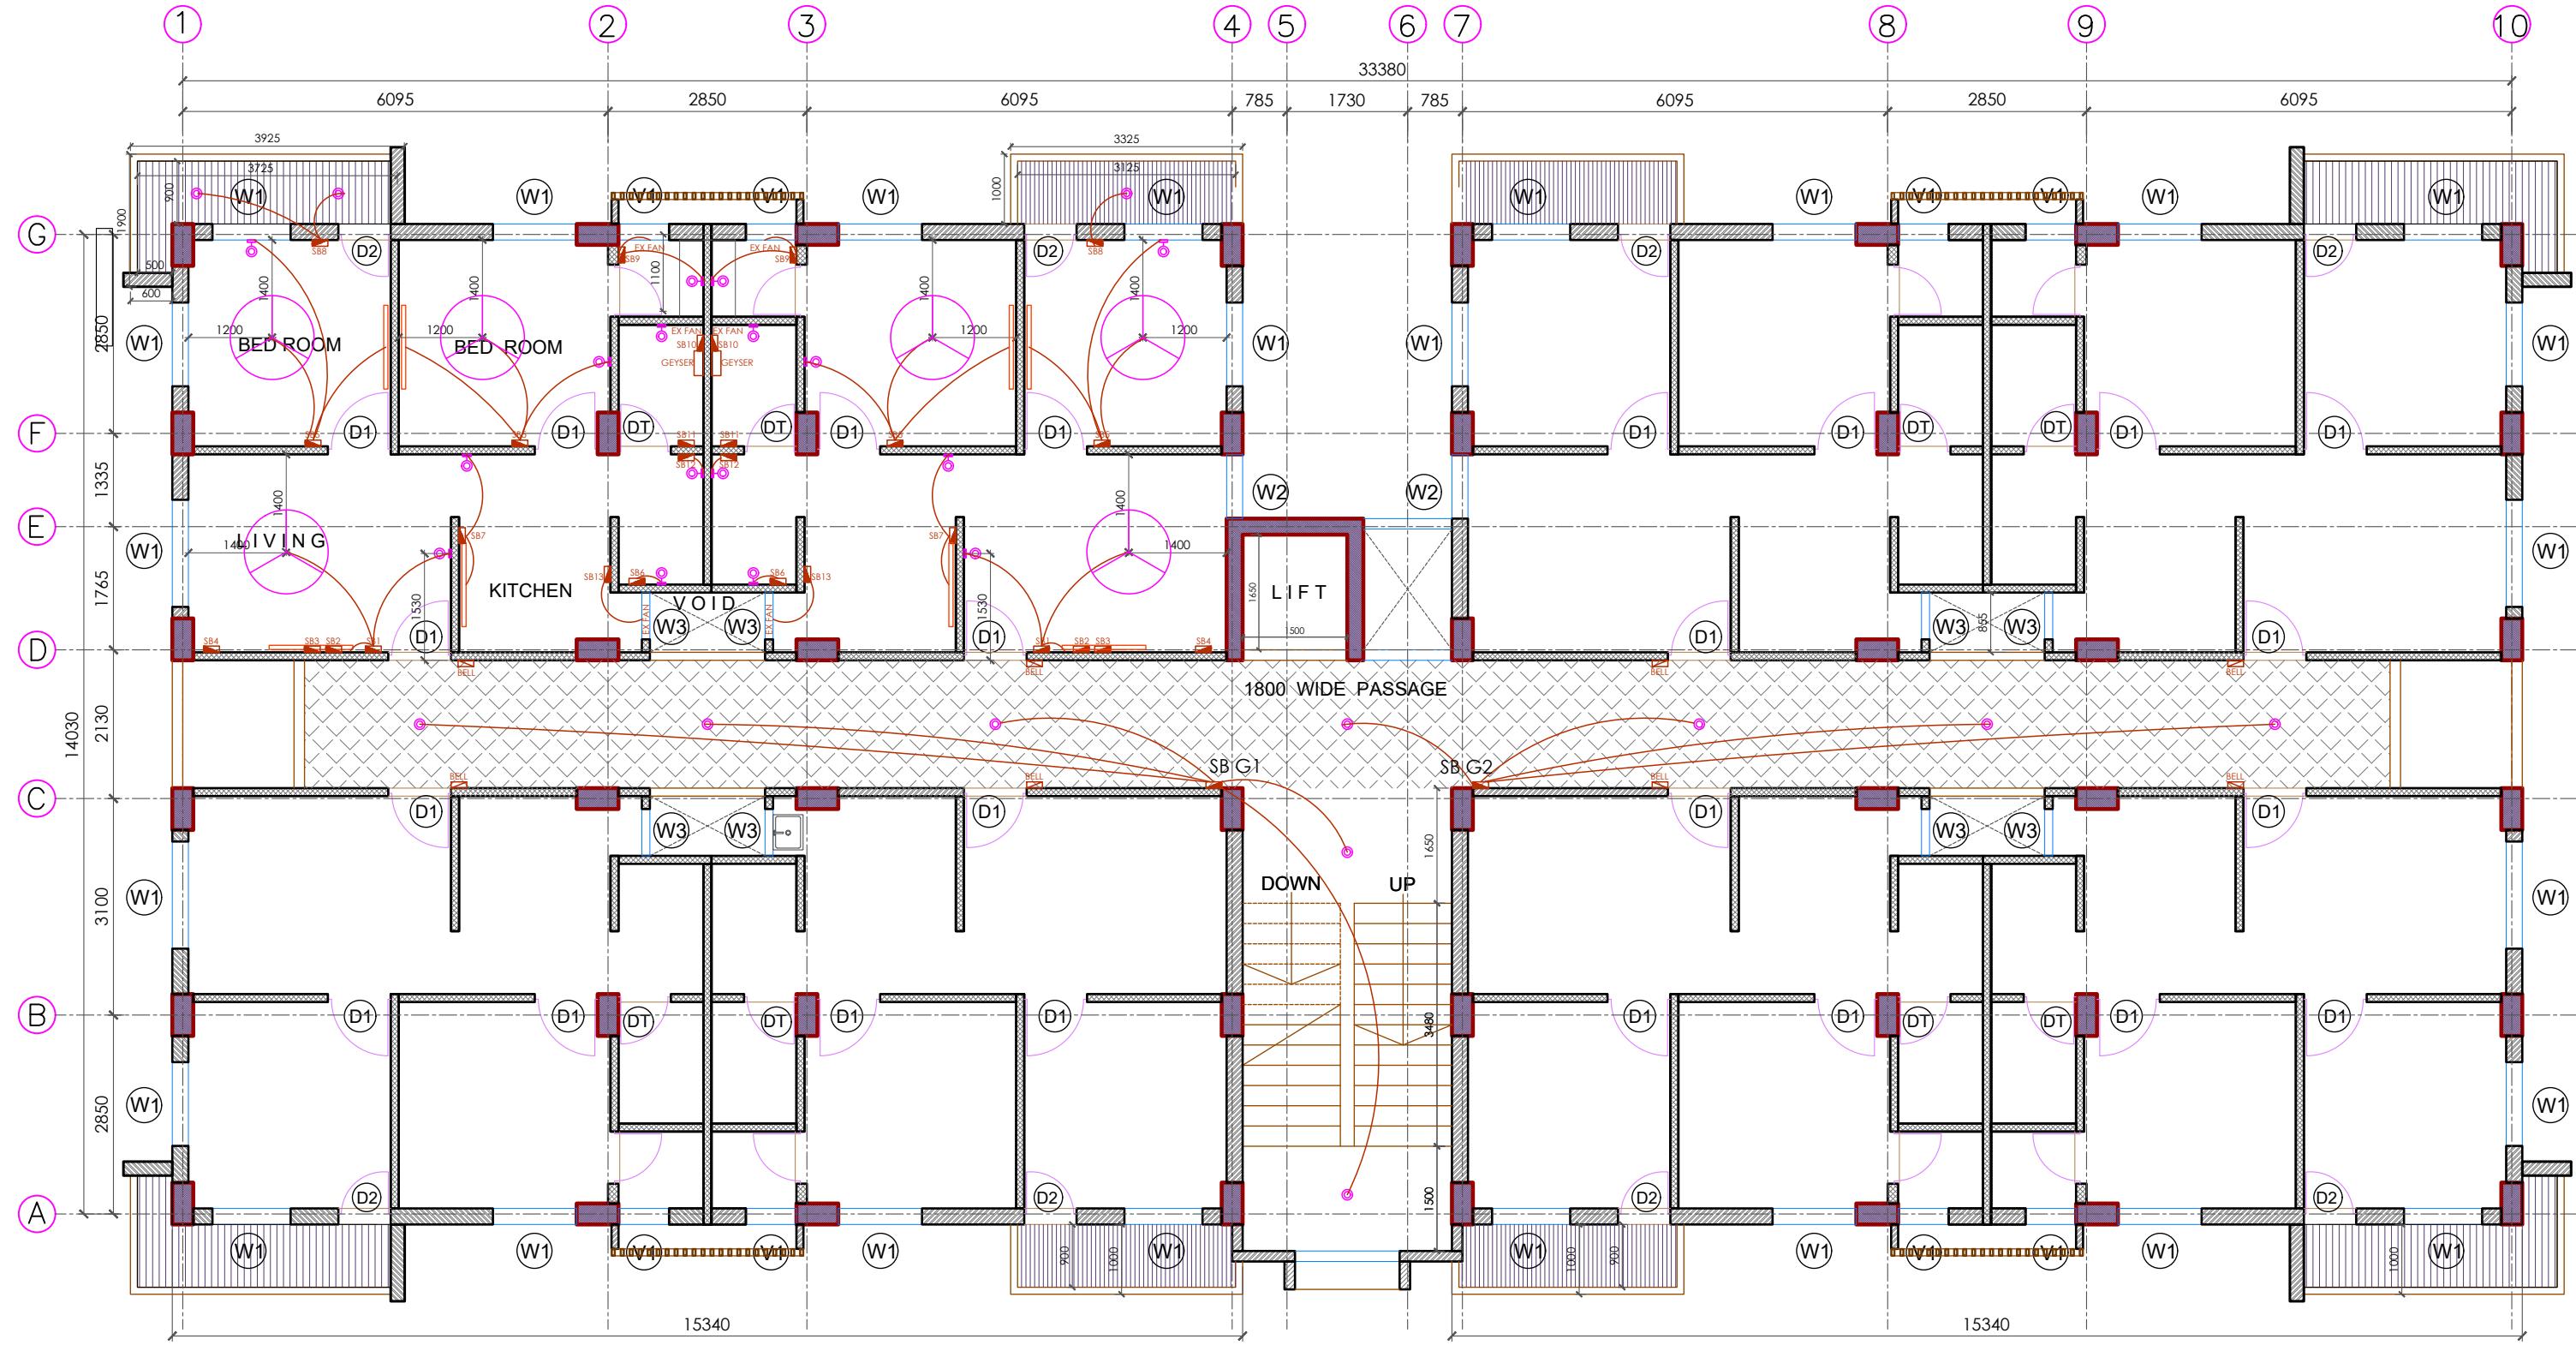

Sayed Saraon Dargah Masjid - Allahabad	TYPICAL FLOOR PLAN : ELECTRICAL PLAN		Type	GA Dwg	Rev	R0
VISHAL SOLANKI ASSOCIATES	FAMILY QUARTER		No	FQ.FP.01	Date	24-02-2020

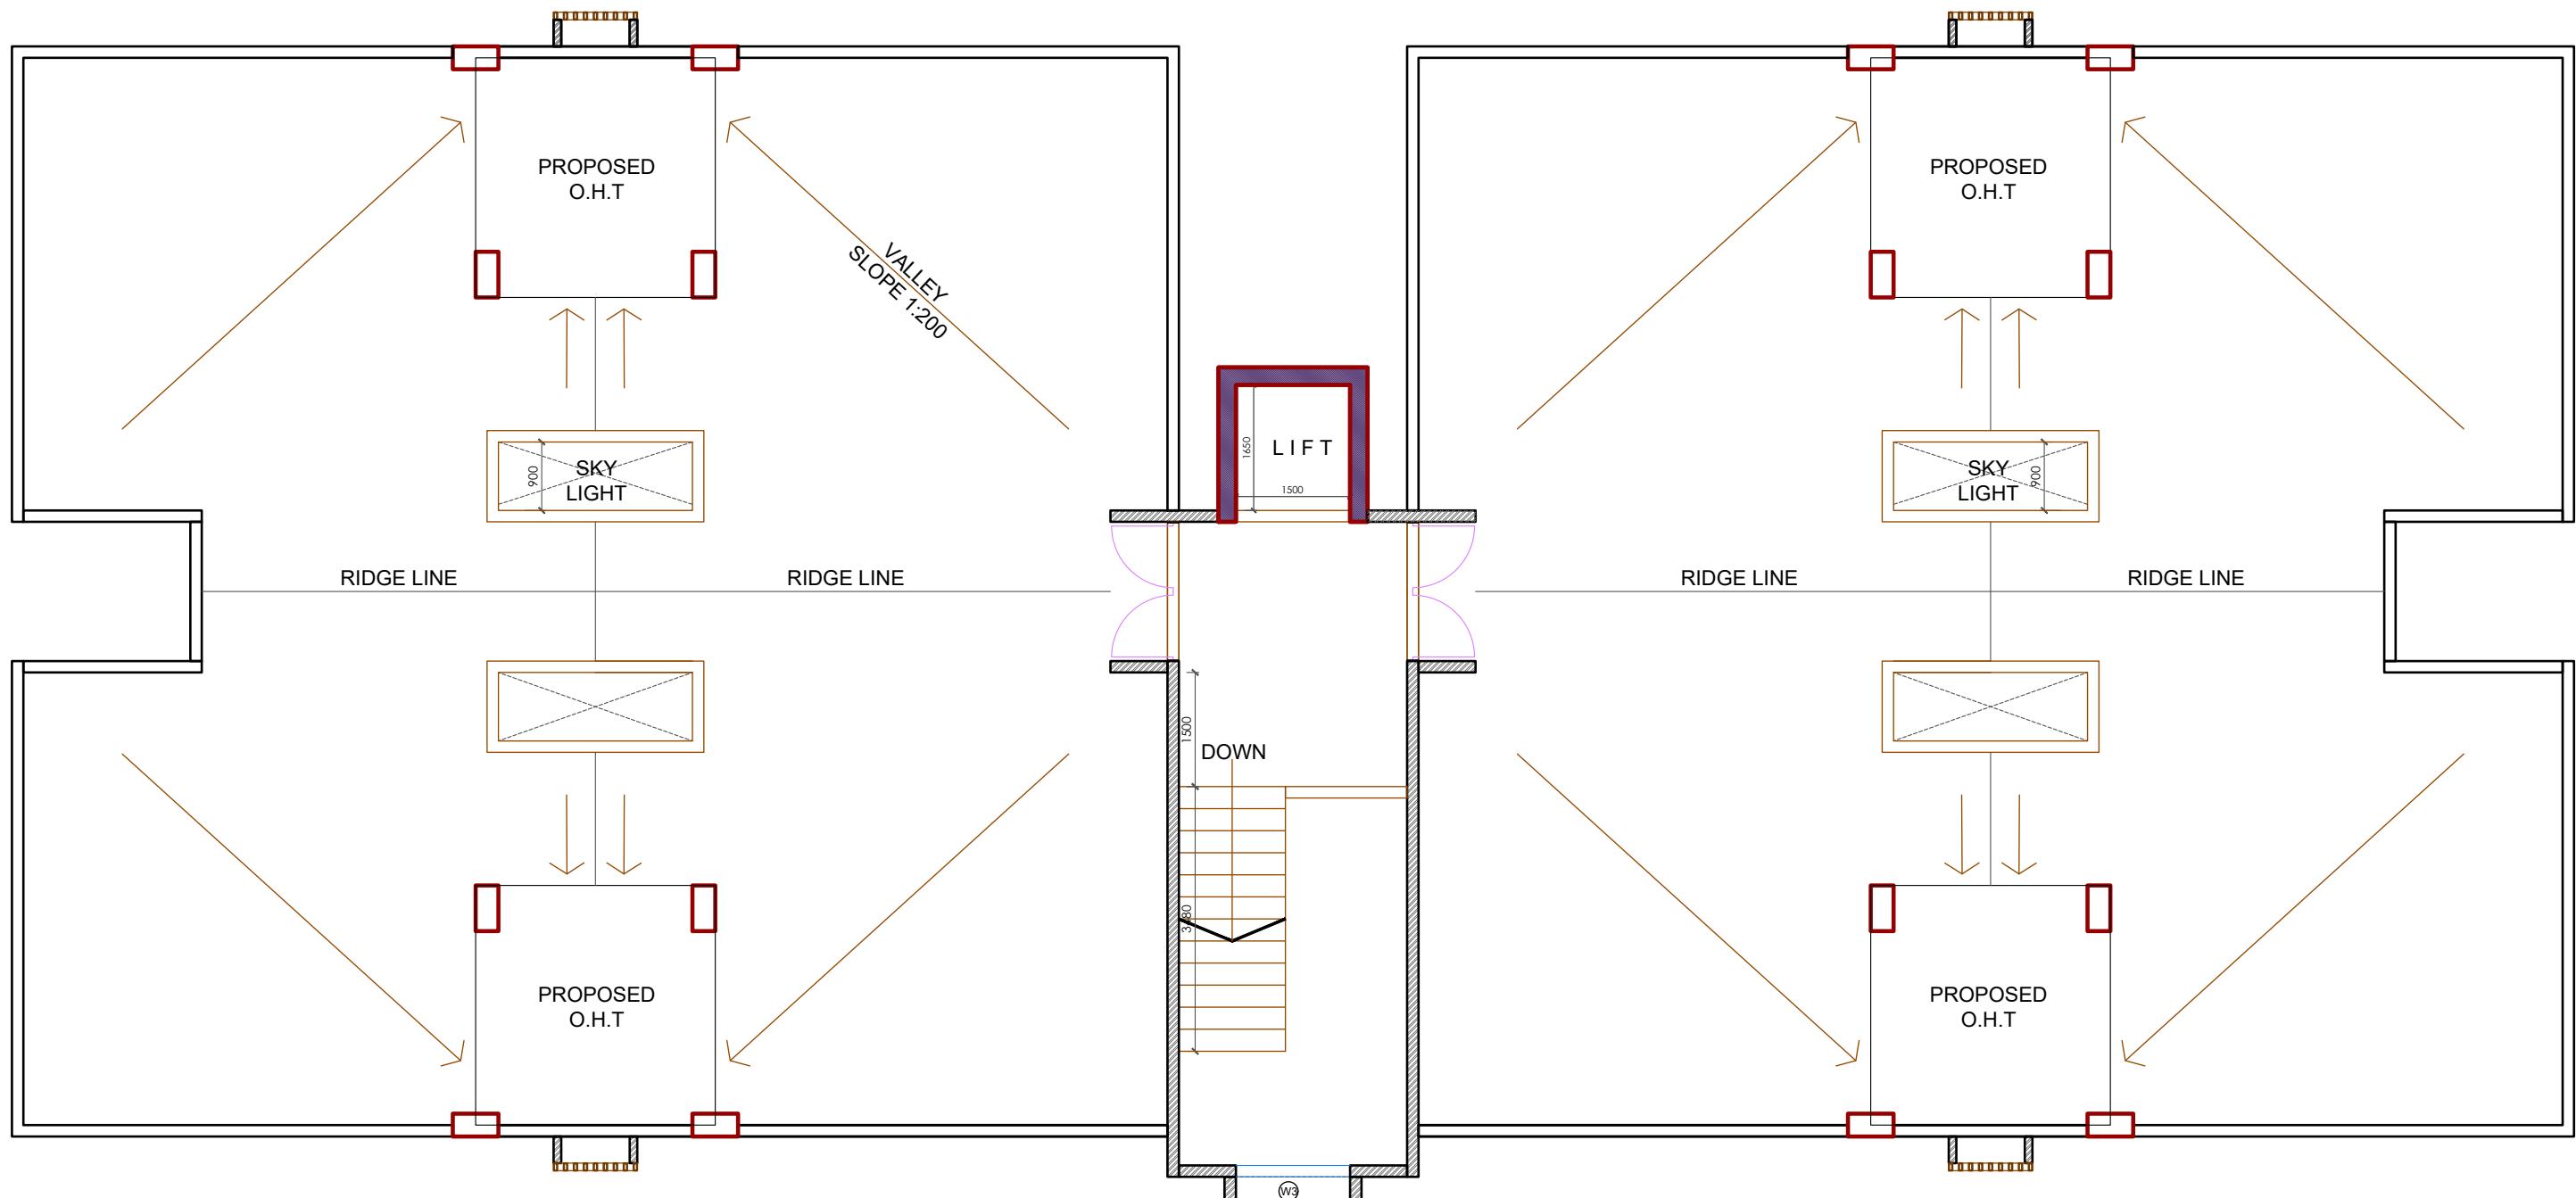


Sayed Saraon Dargah Masjid - Allahabad

TERRACE FLOOR PLAN

VISHAL SOLANKI ASSOCIATES

FAMILY QUARTER

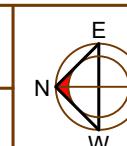

No

GA Dwg  
FQ.TR.01

Date  
10-11-2019

Rev  
R0



Sayed Saraon Dargah Masjid - Allahabad

Elevation

VISHAL SOLANKI ASSOCIATES

FAMILY QUARTER



No

Type

GA Dwg  
FQ.GP.01

Rev  
Date  
11-12-2019

R2



Sayed Saraon Dargah Masjid - Allahabad

Elevation

VISHAL SOLANKI ASSOCIATES

FAMILY QUARTER




No

GA Dwg  
FQ.GP.01

Rev  
Date  
11-12-2019

R2

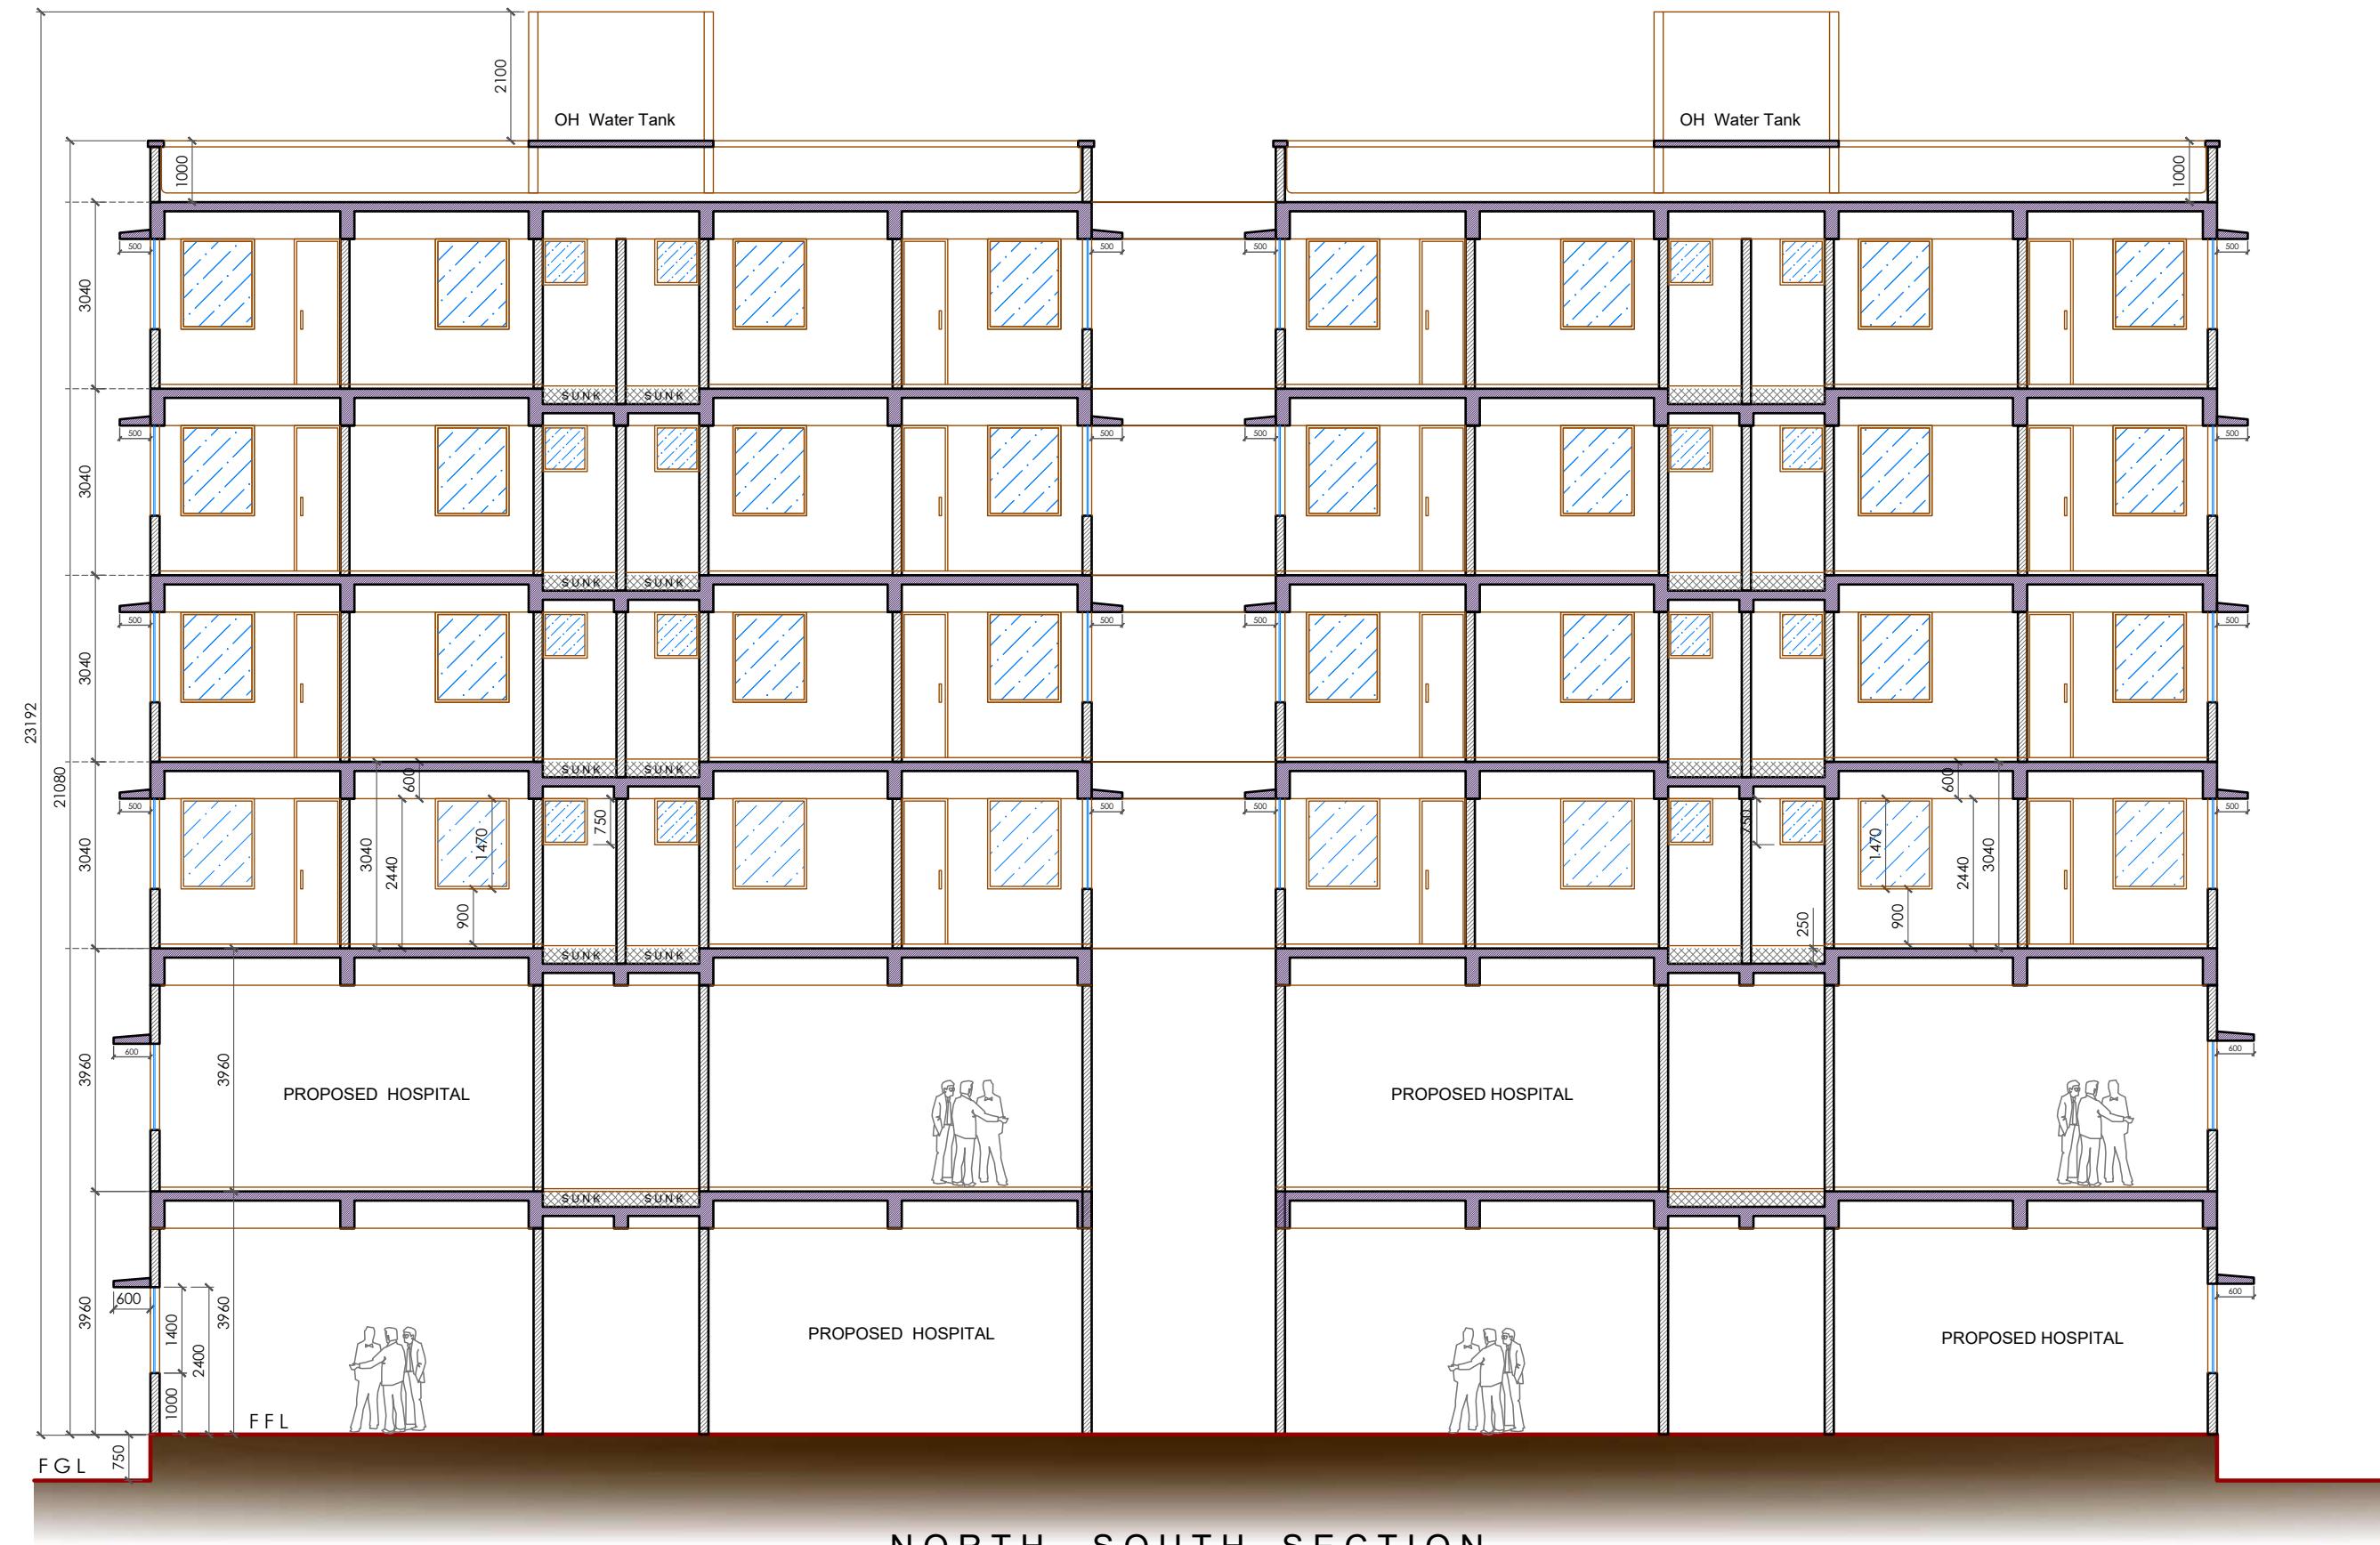


Sayed Saraon Dargah Masjid - Allahabad

VISHAL SOLANKI ASSOCIATES


SECTION



FAMILY QUARTER


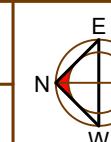



GA Dwg  
FQ.GP.01


Rev  
R2  
Date  
11-12-2019

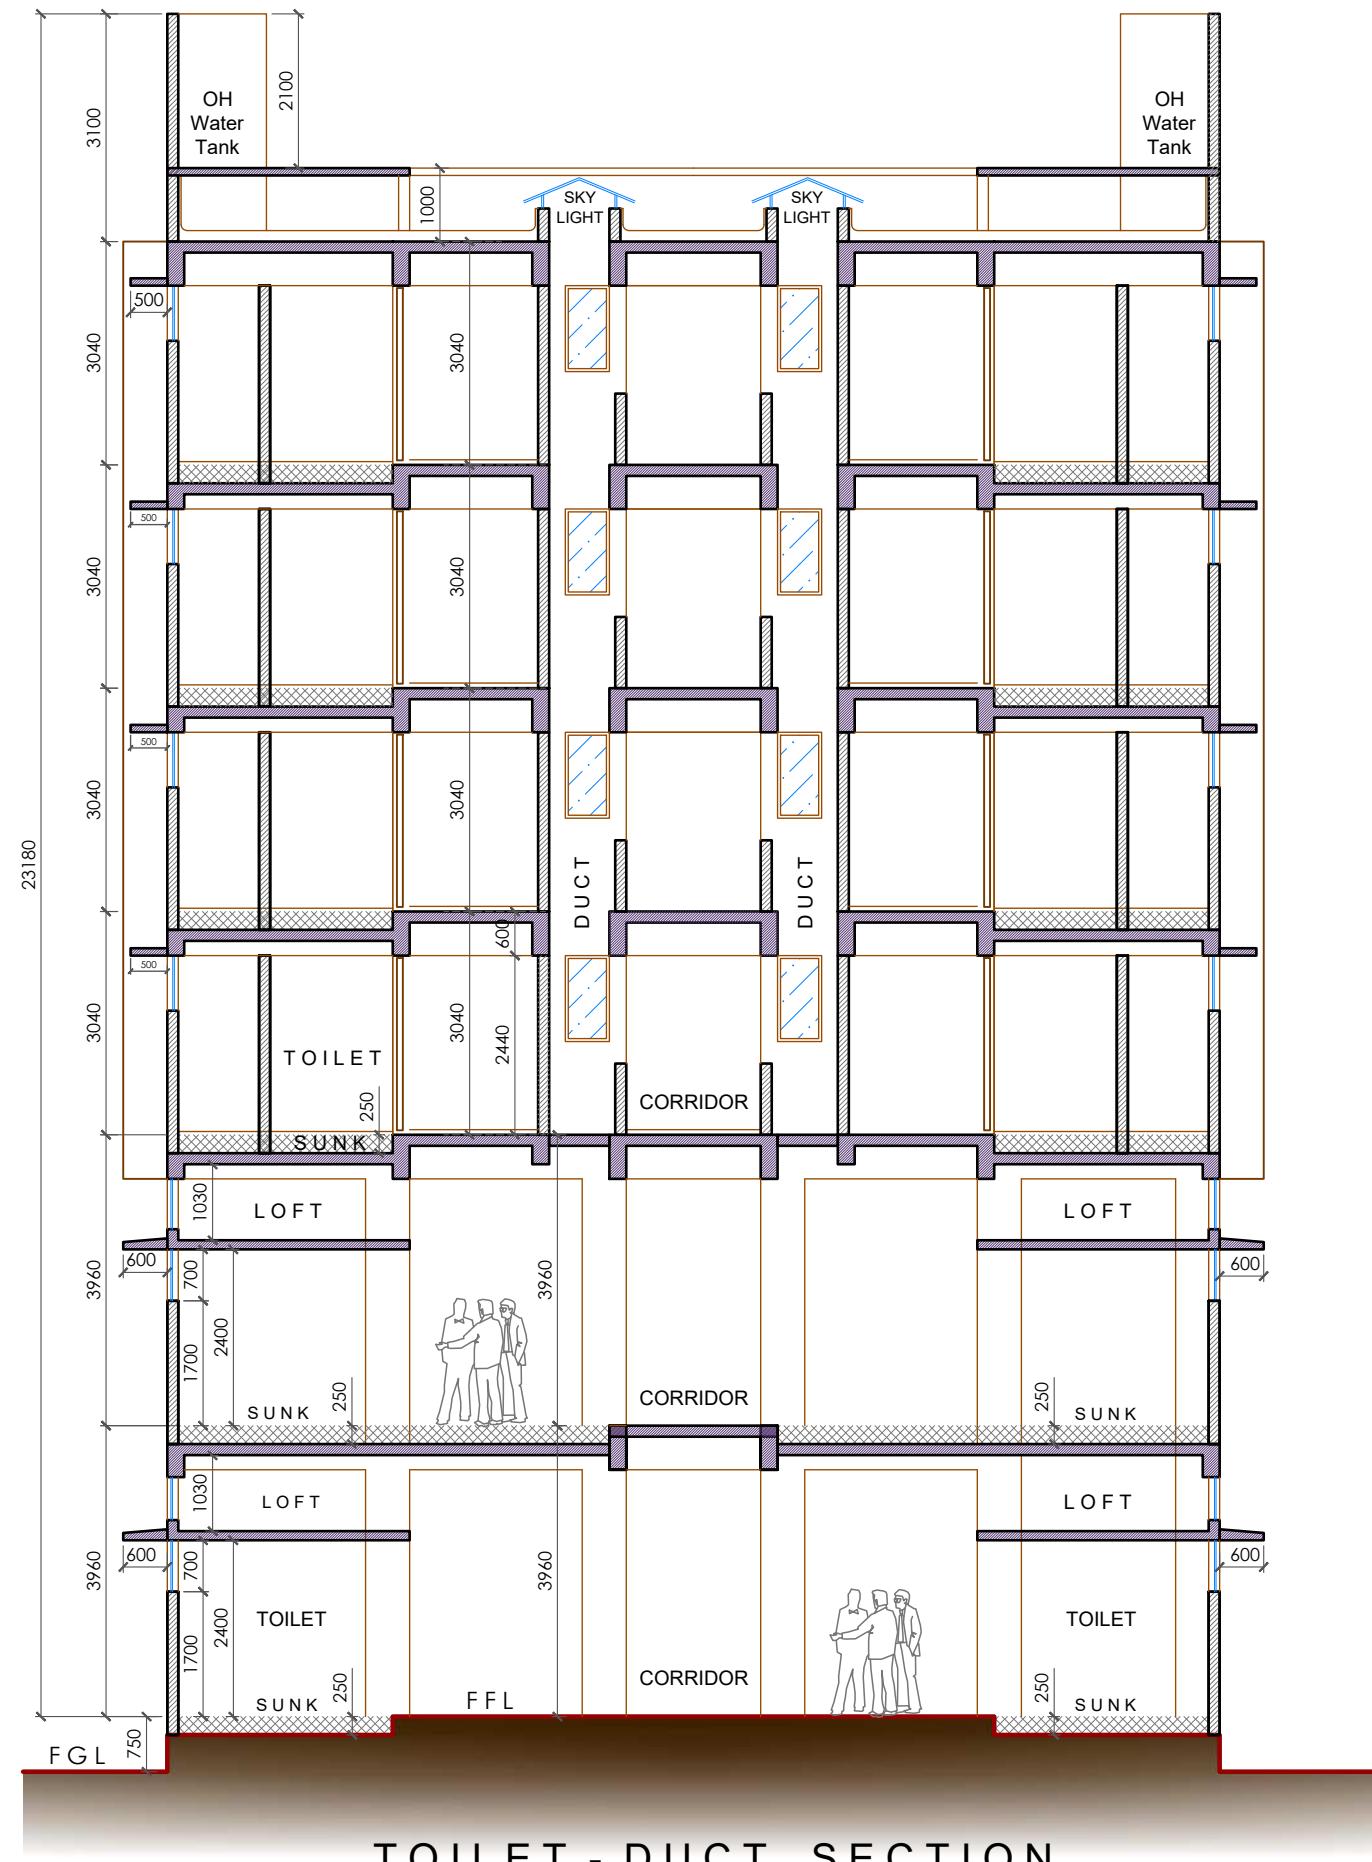


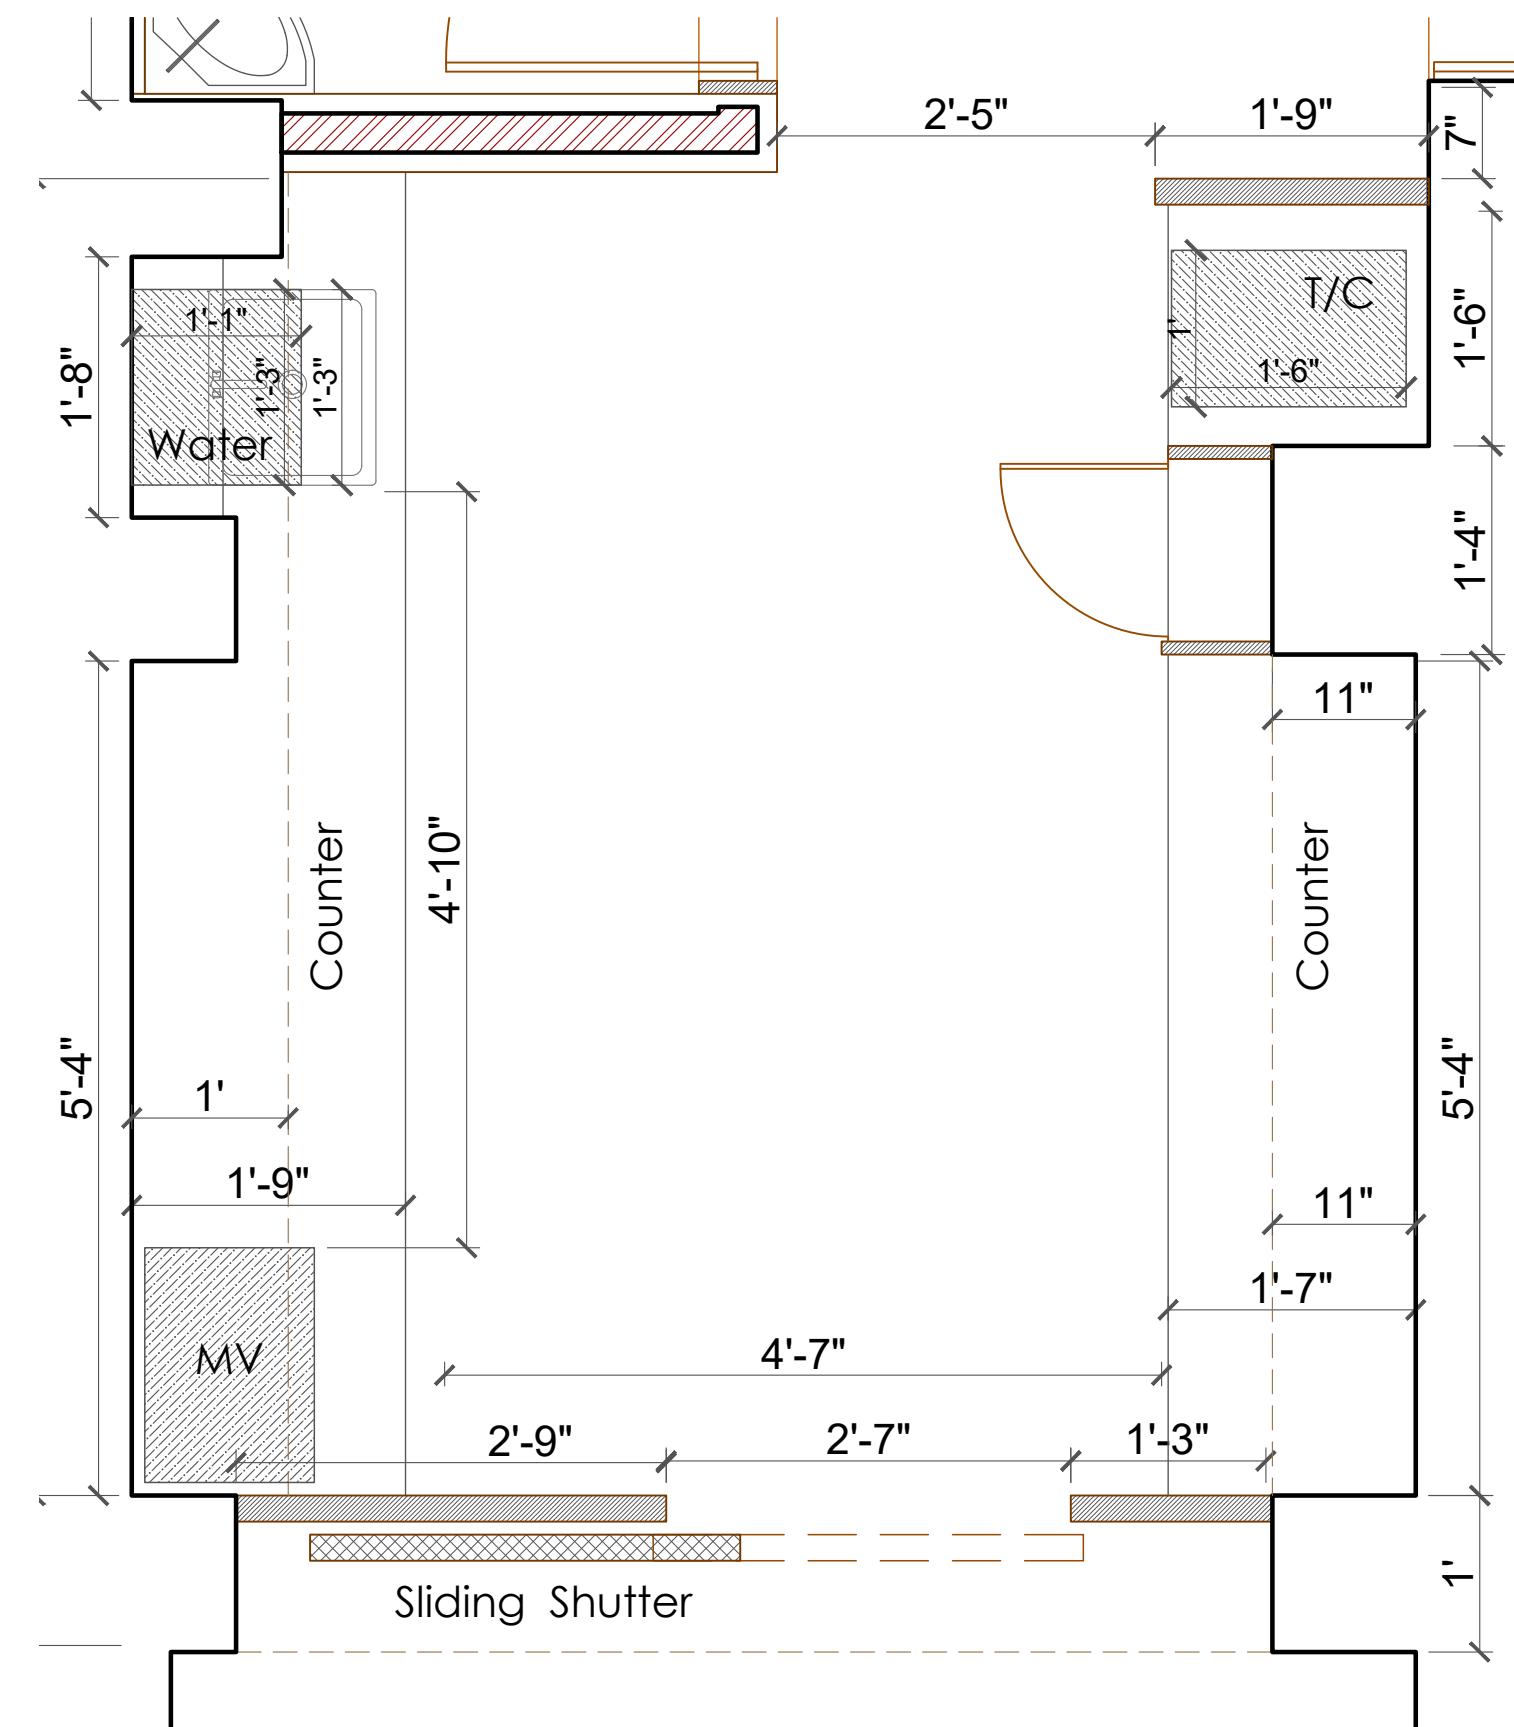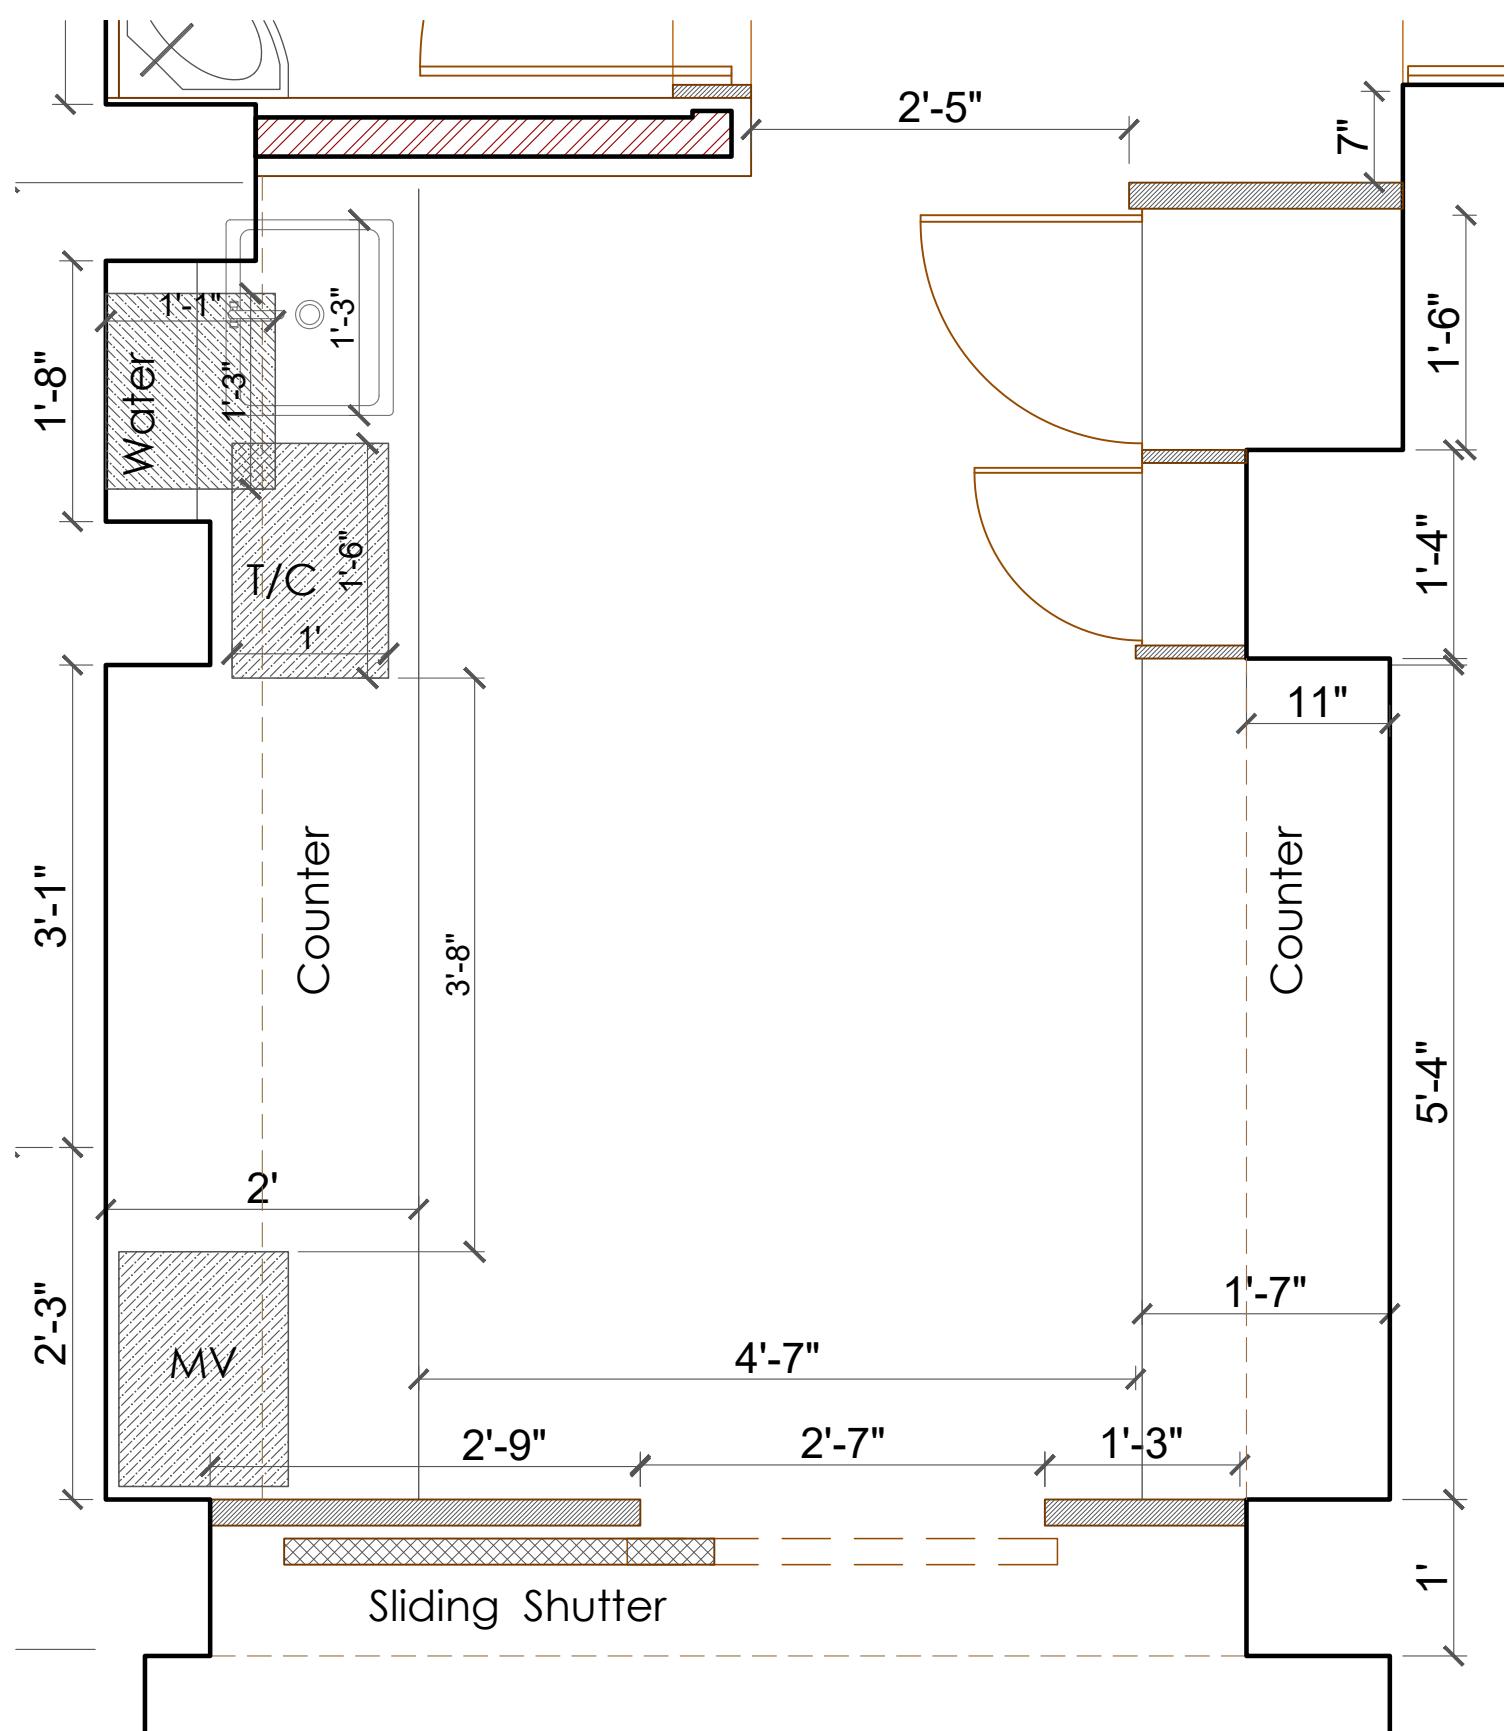

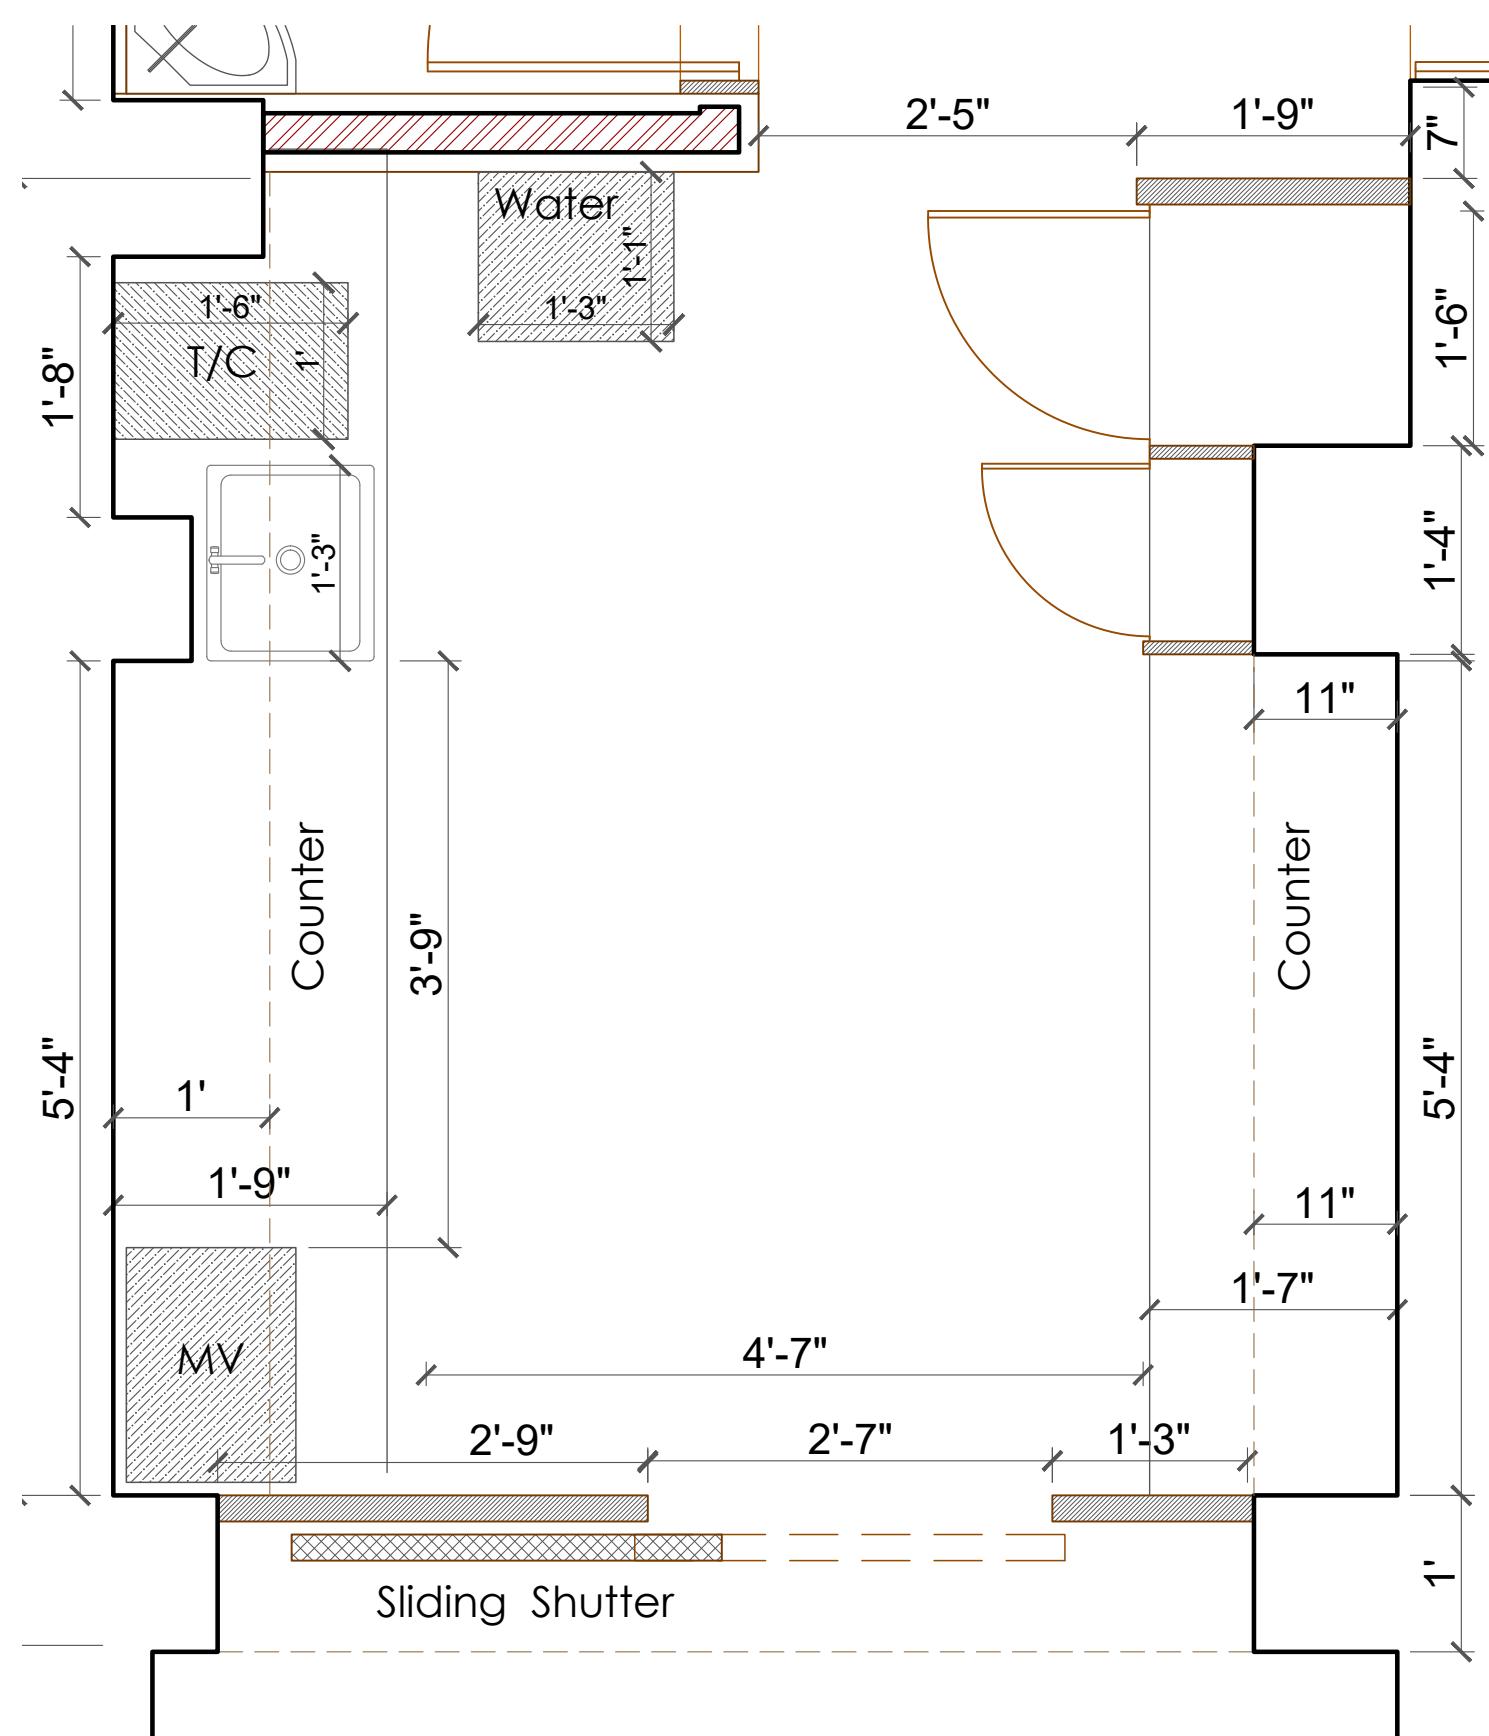
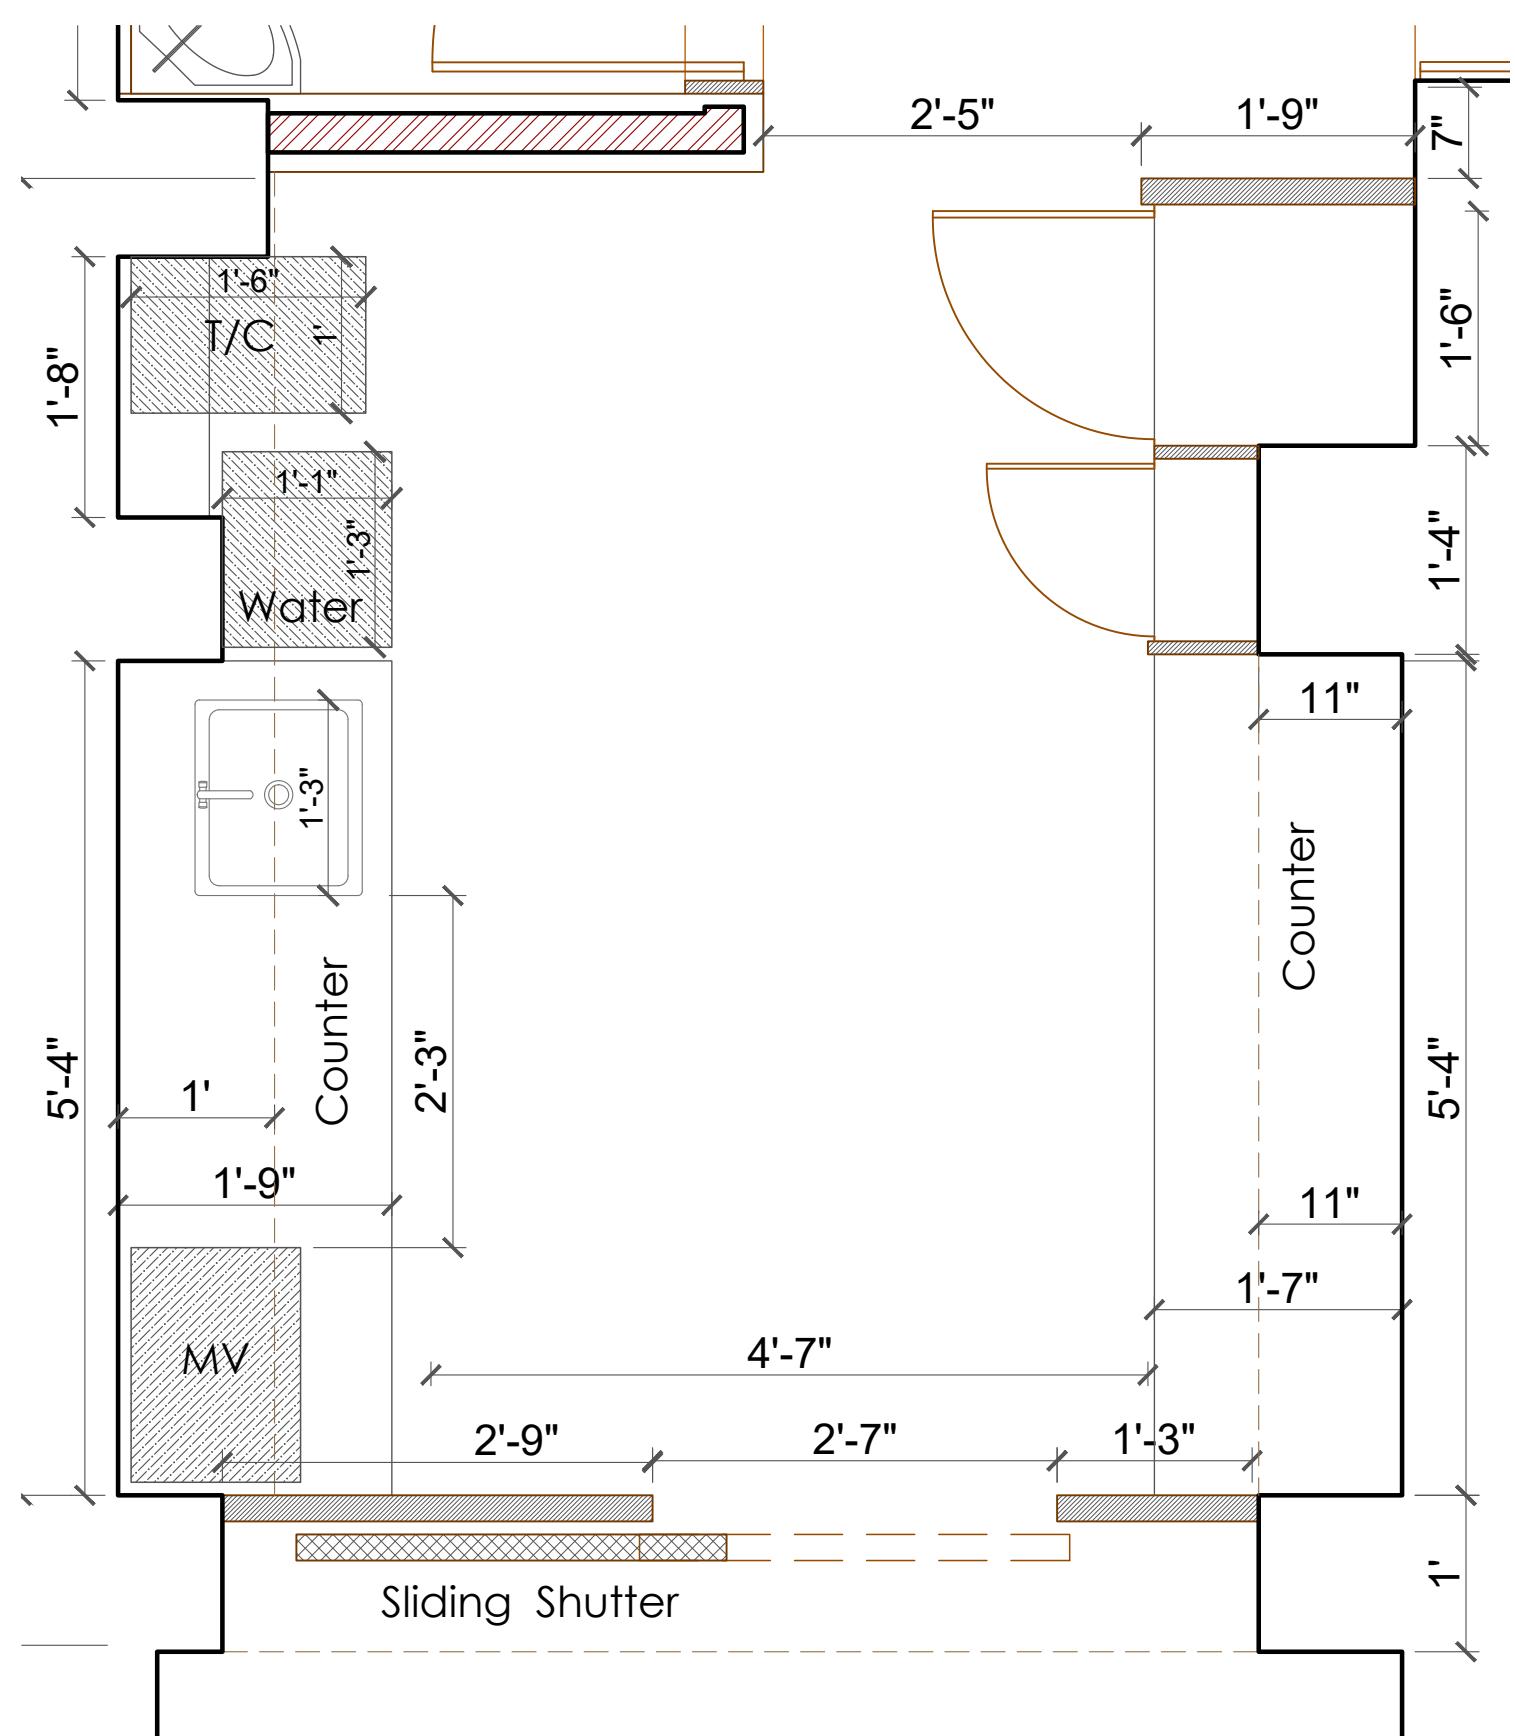



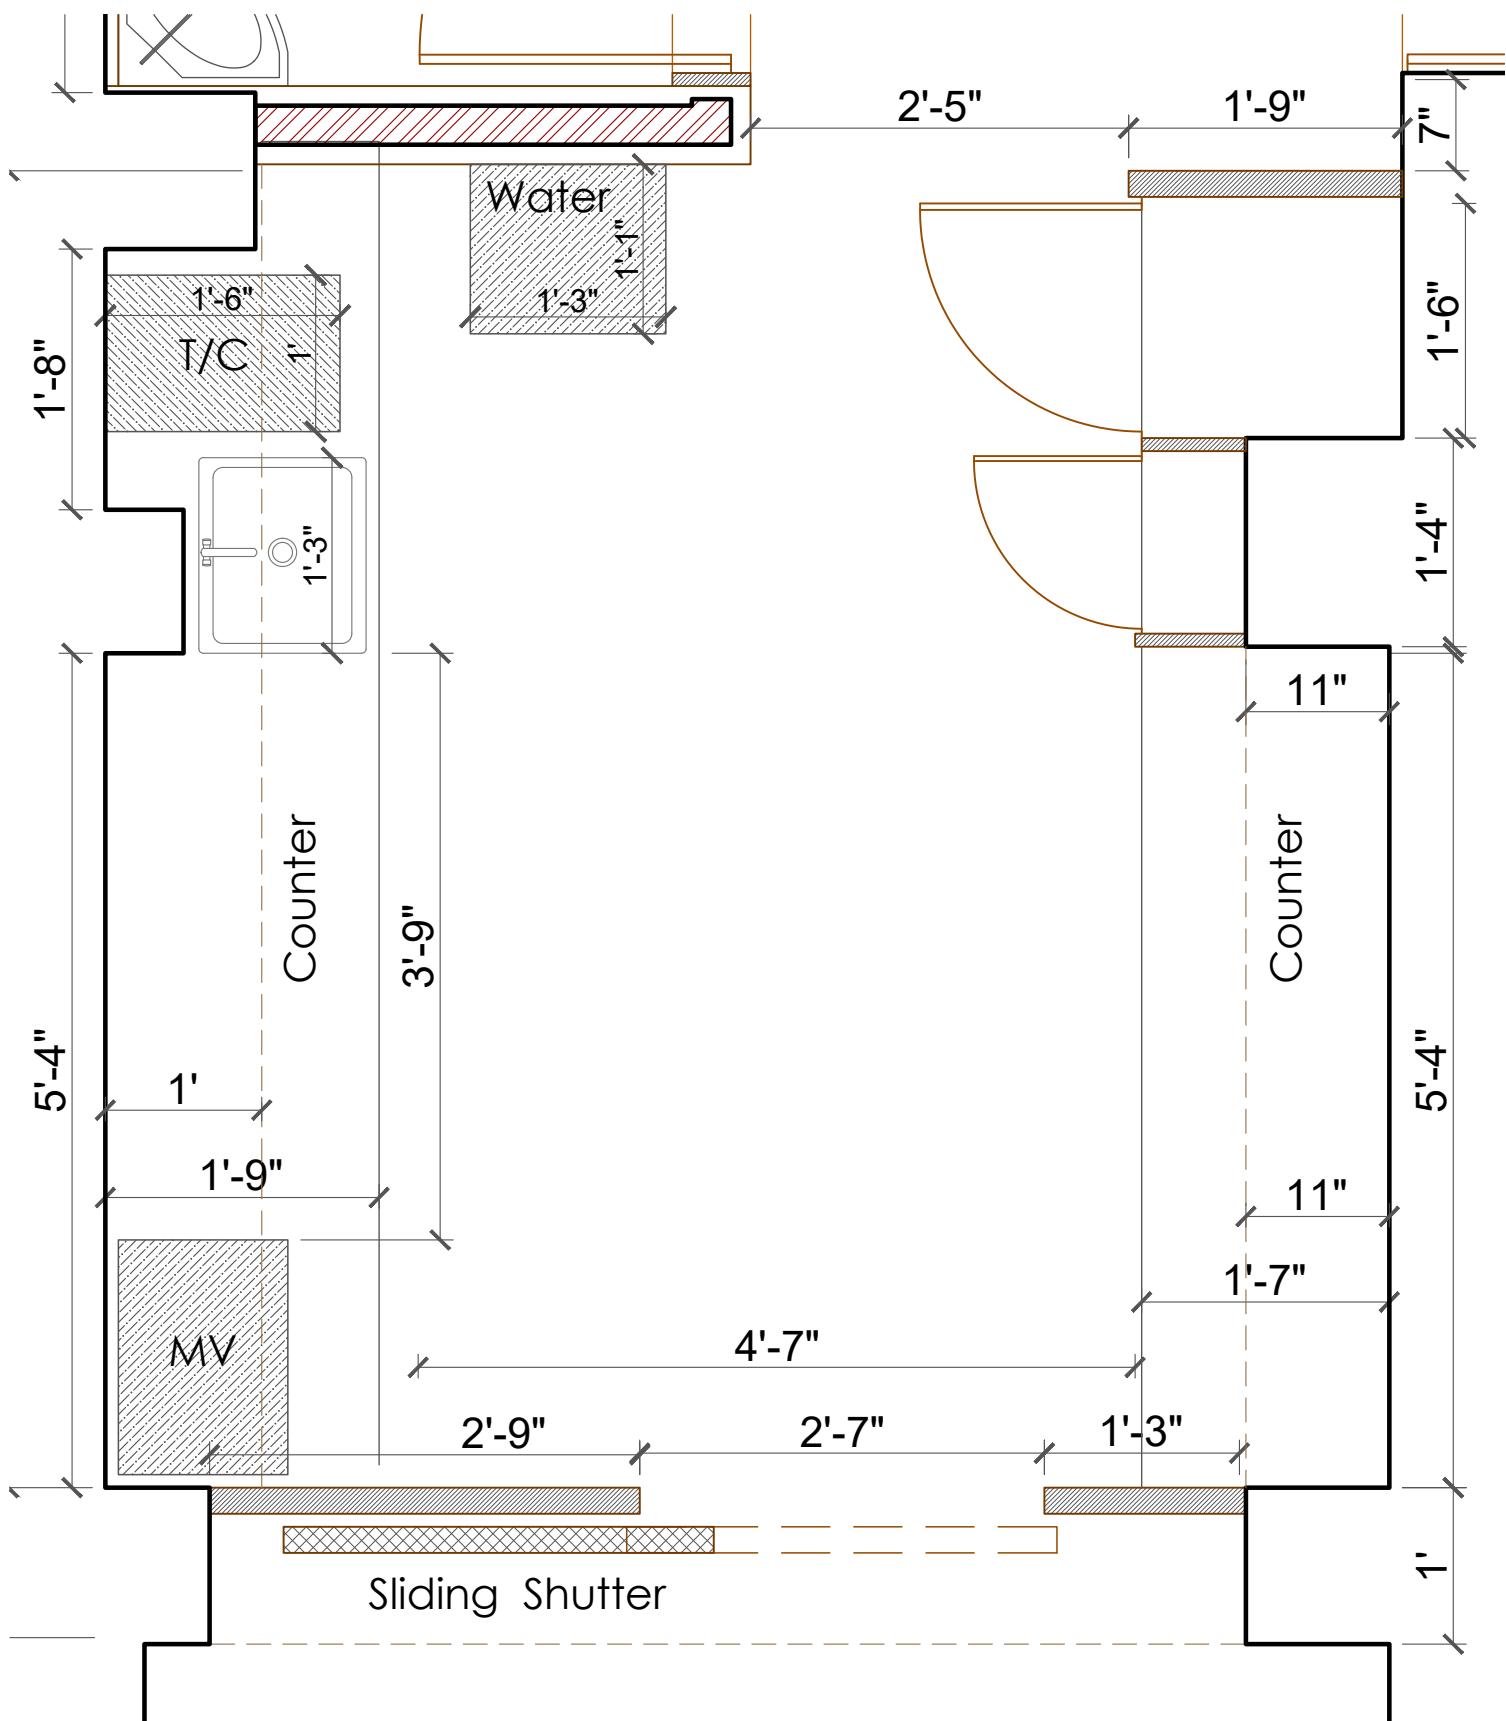



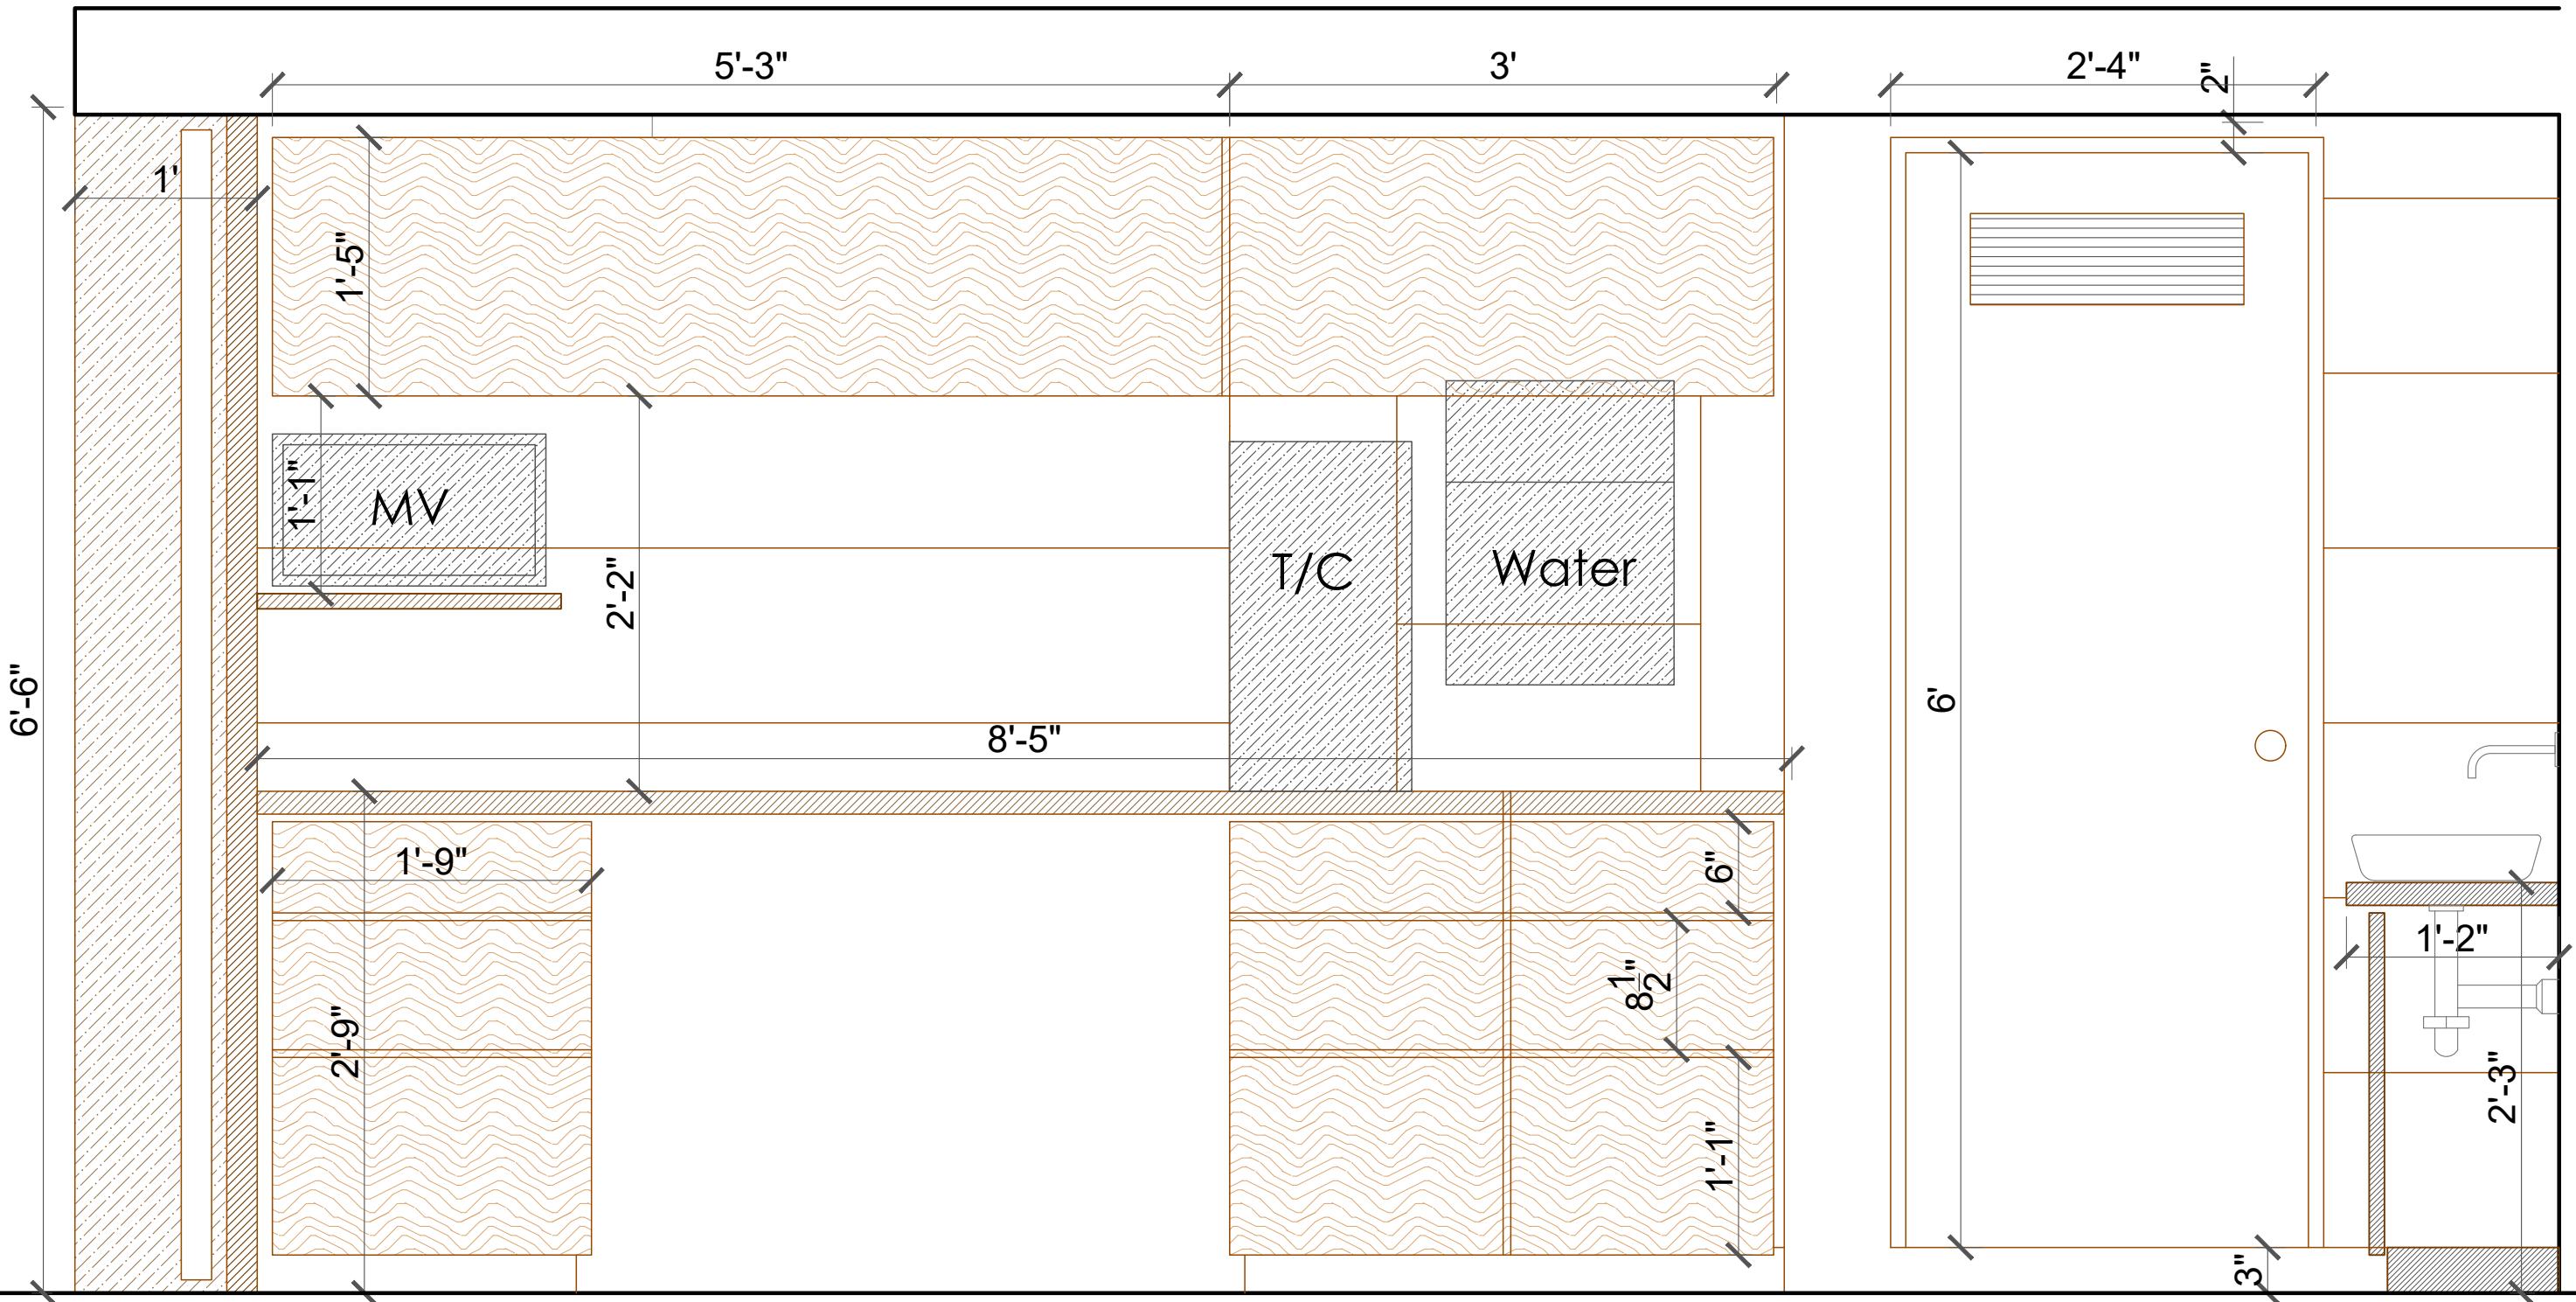



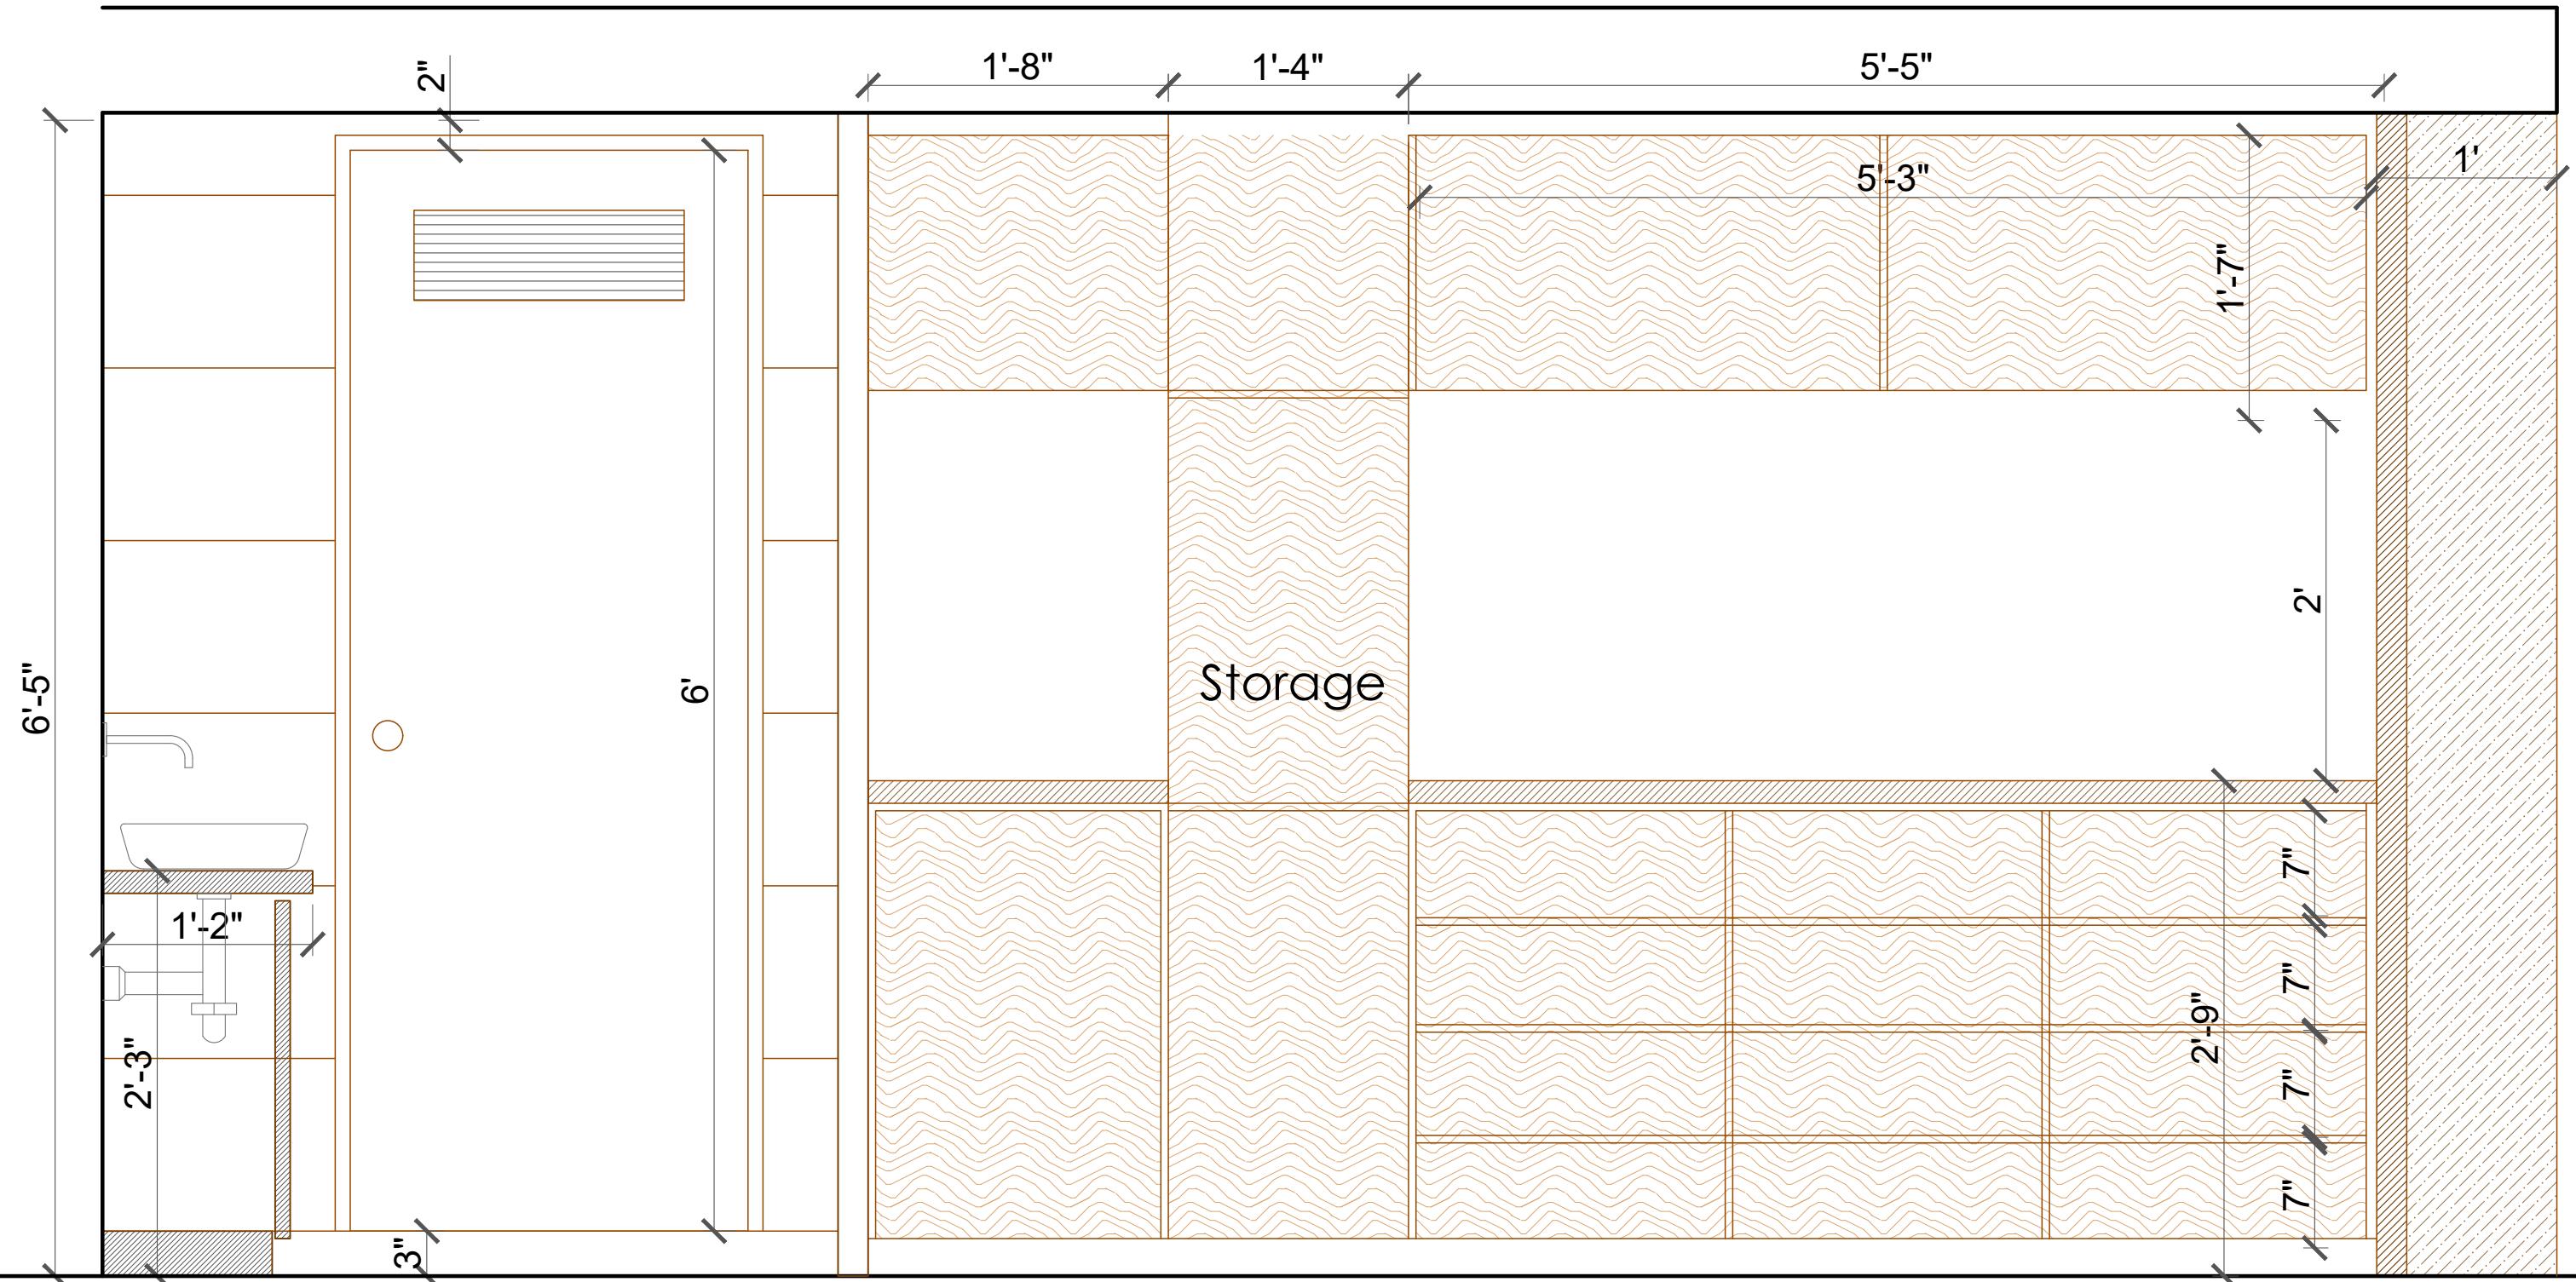



<b>VISHAL SOLANKI ASSOCIATES</b>	CLIENT : <i>Autoflow</i>		Type	GA Dwg	Rev	R1
svdesign.v@gmail.com   9920351604	Interior at New Panvel	WEST ELEVATION : 02	D no	IK.EL.03	Date	11-01-2019



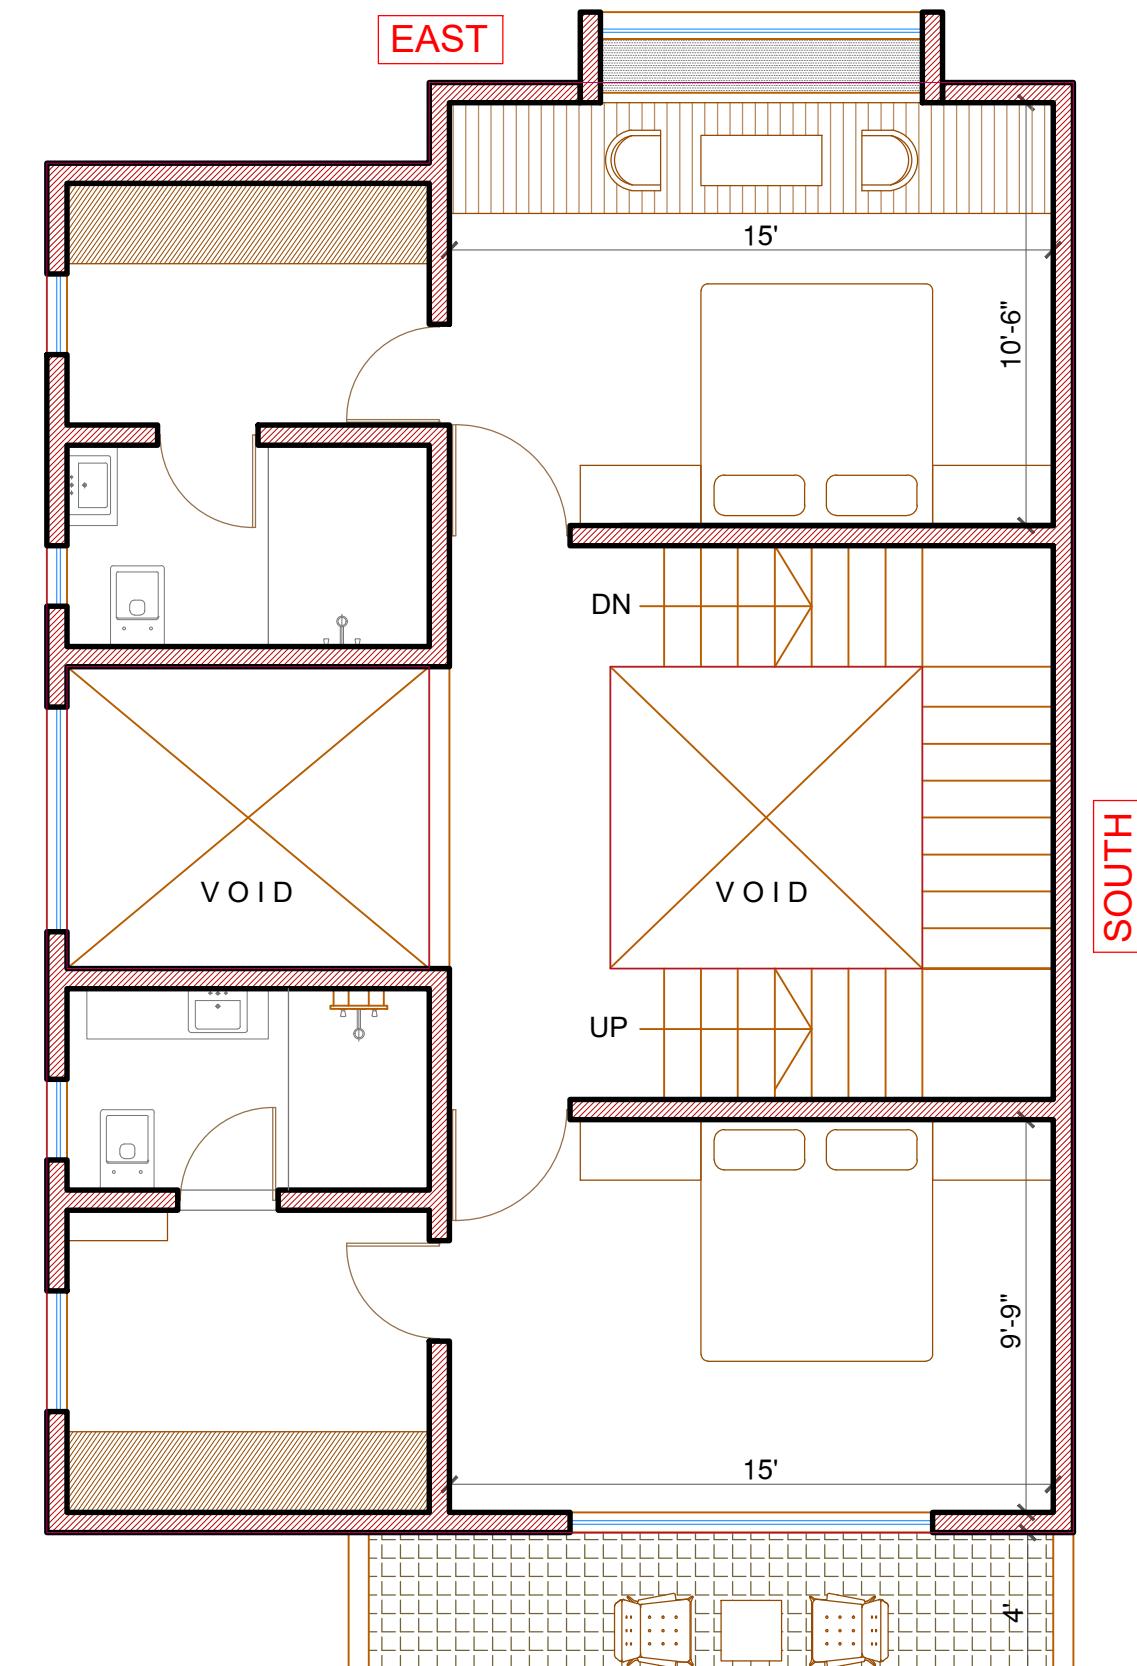
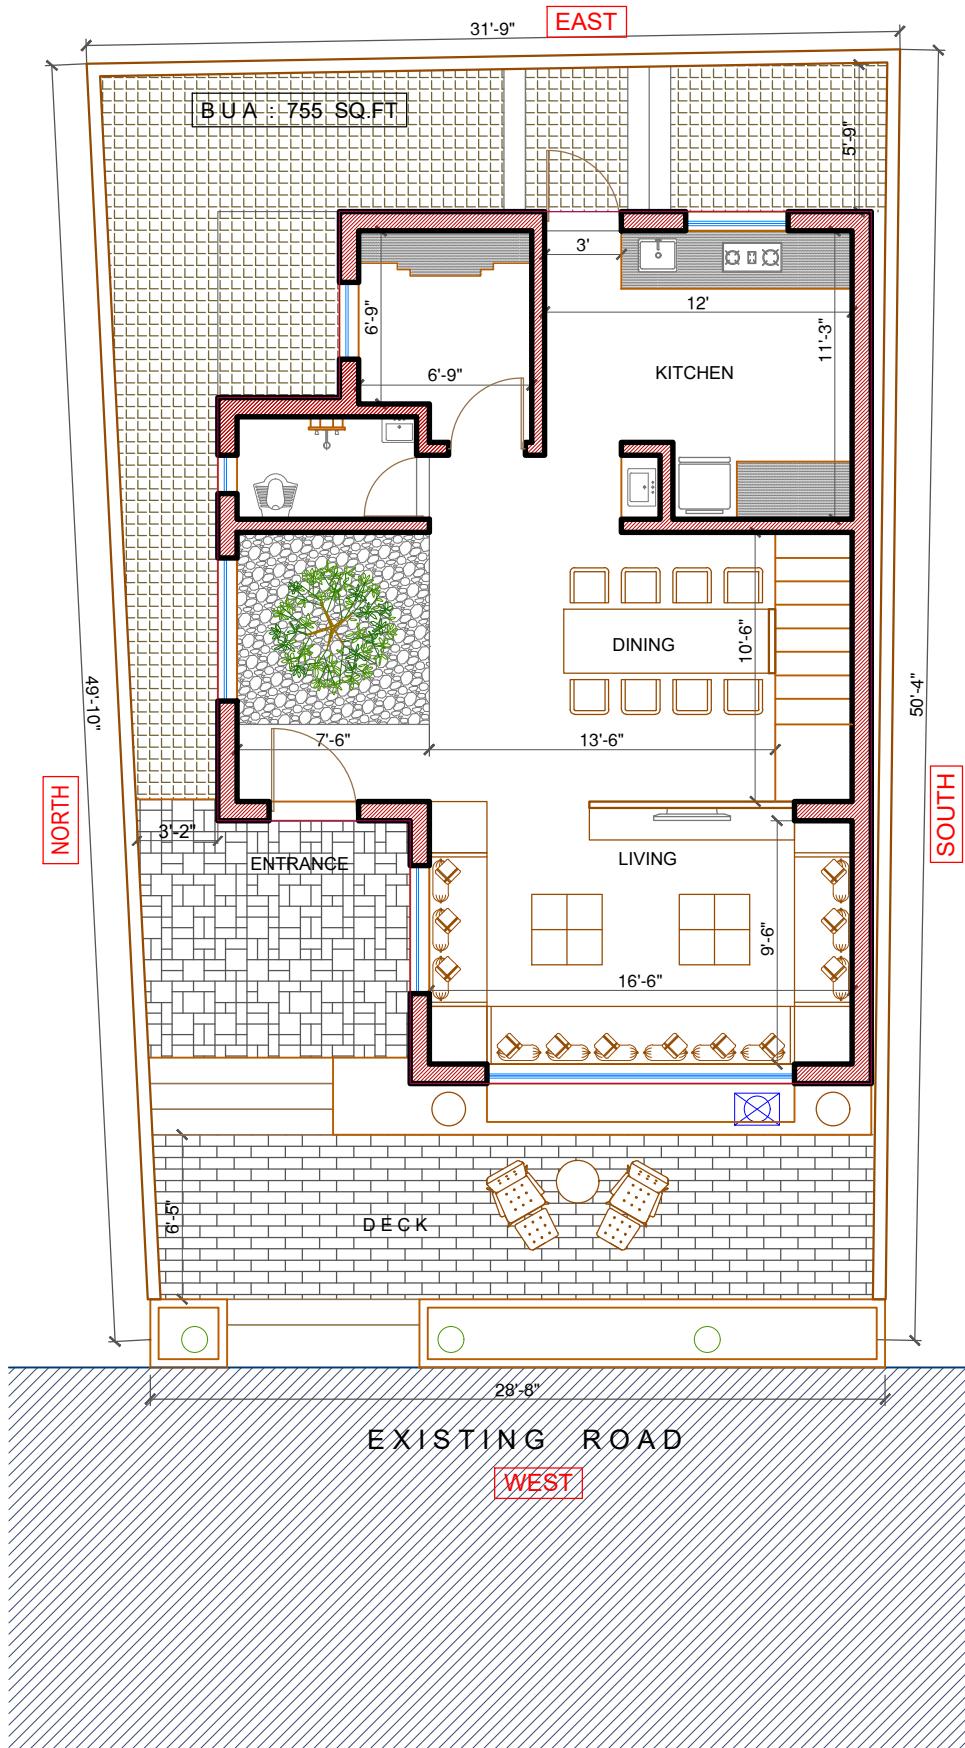


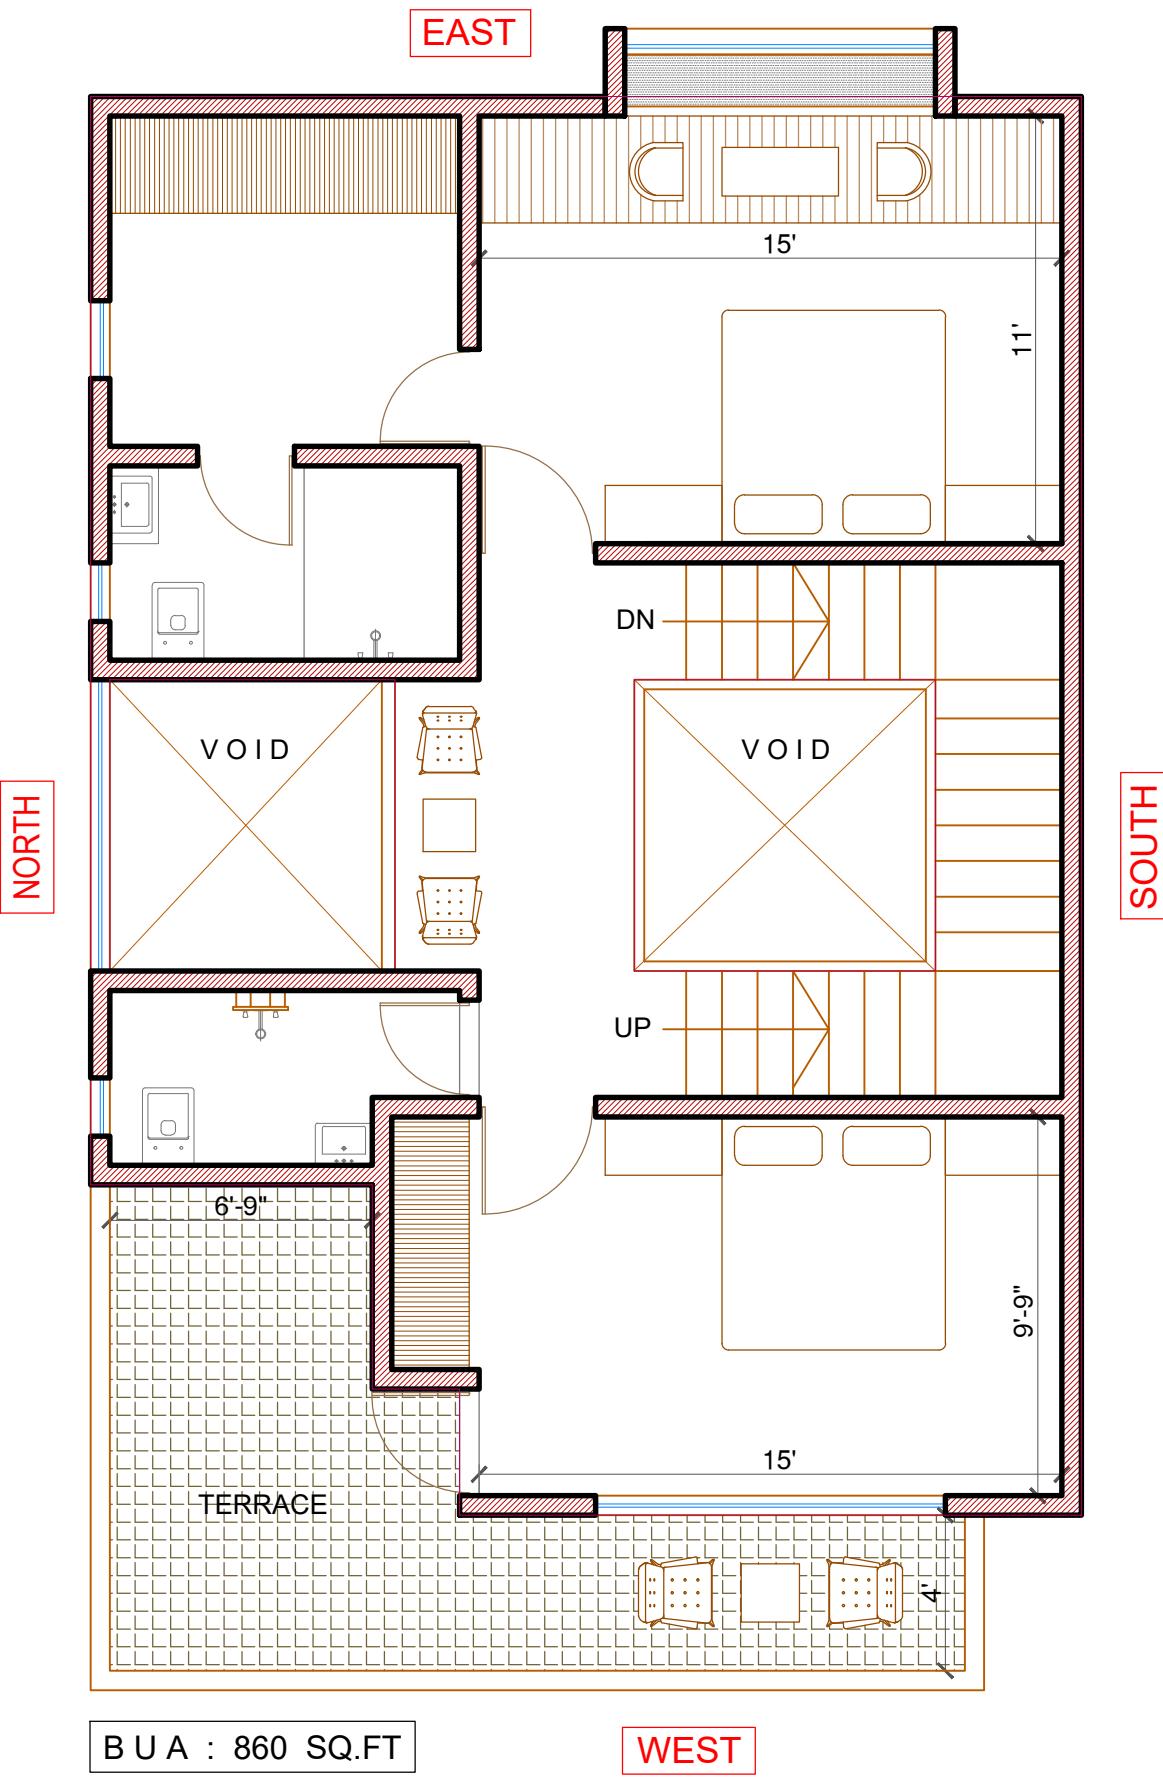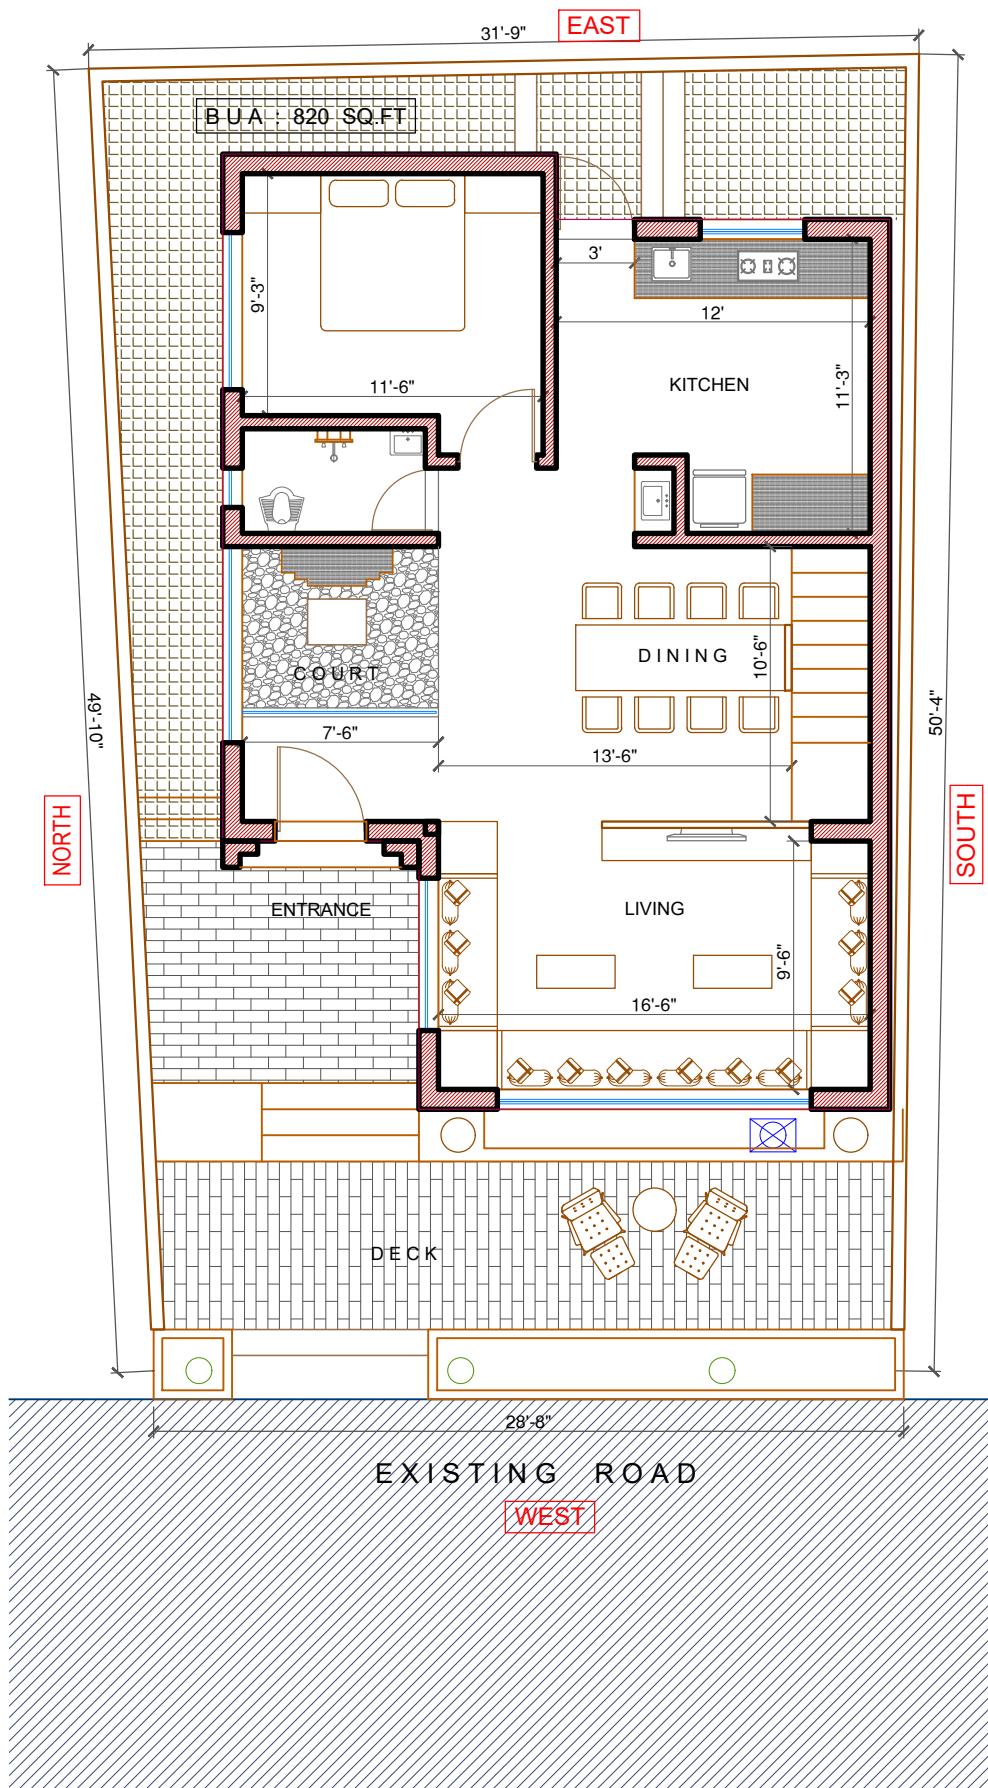

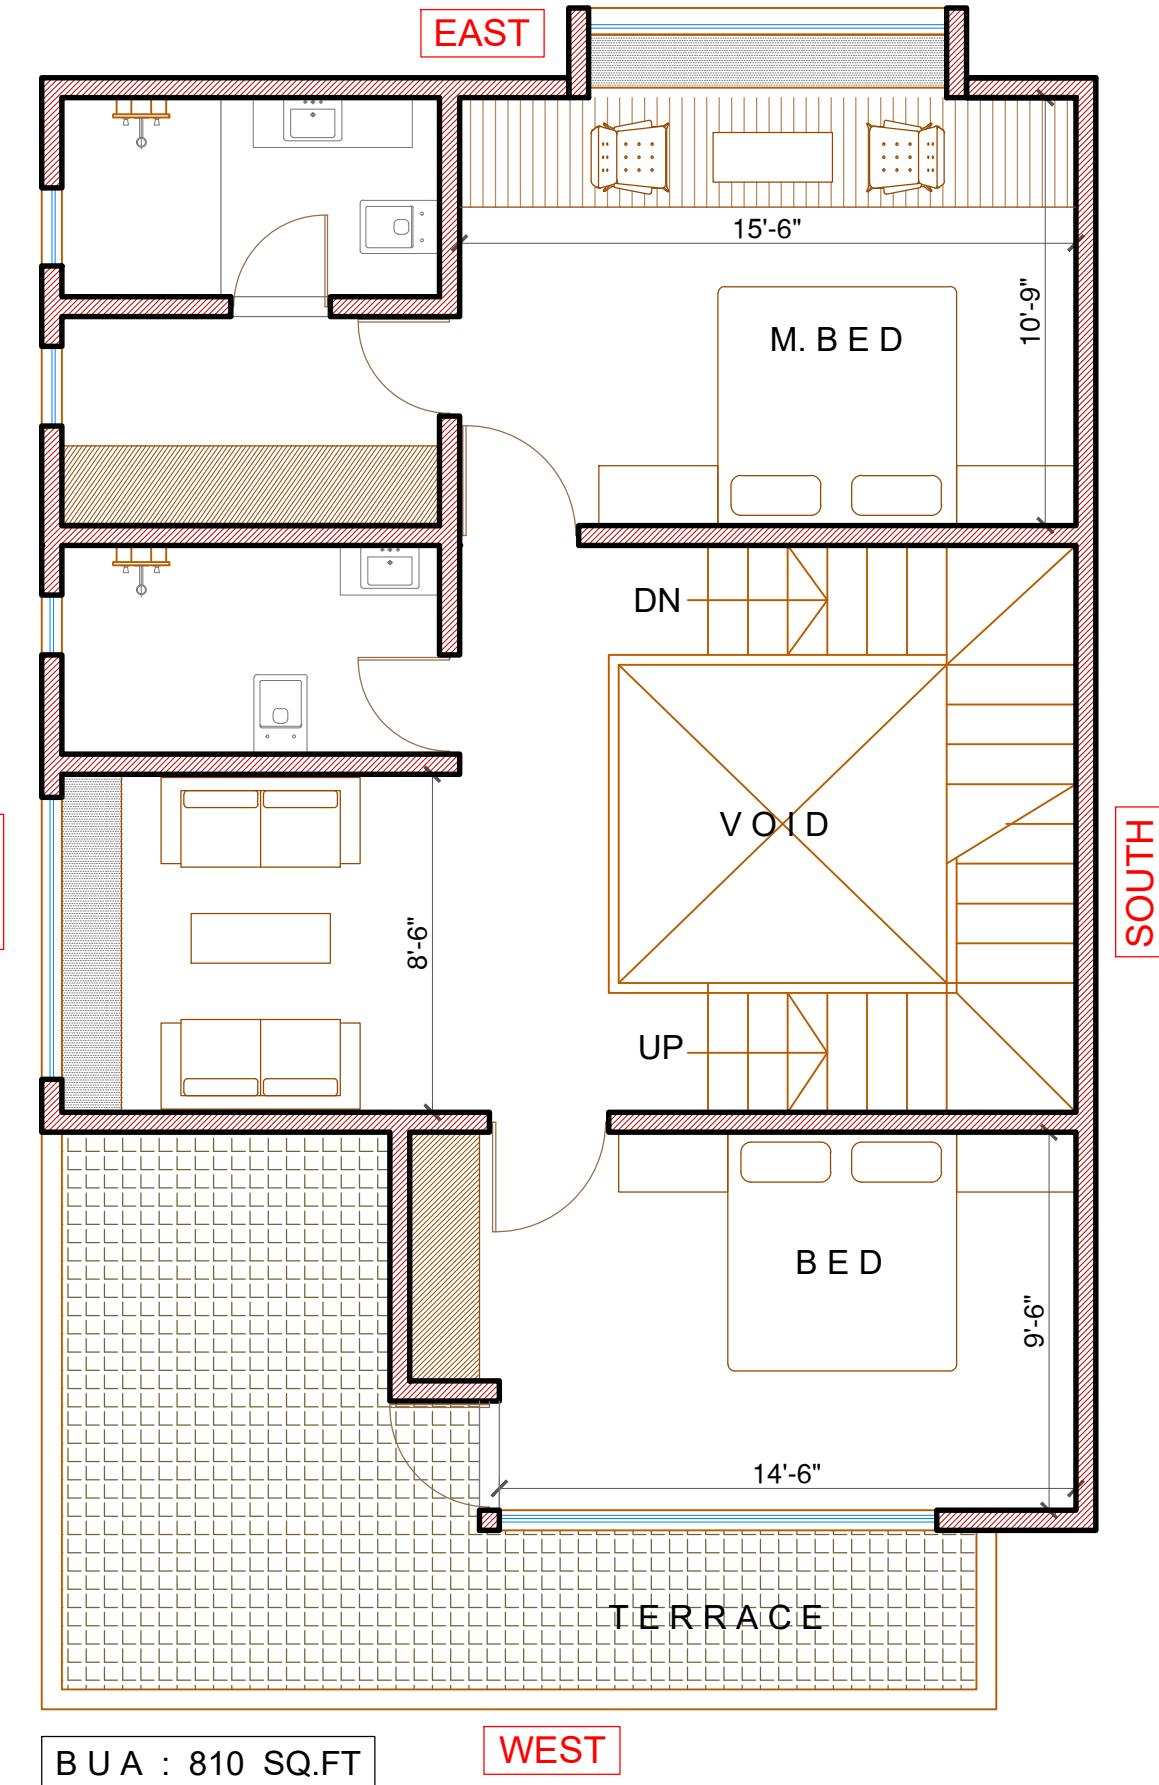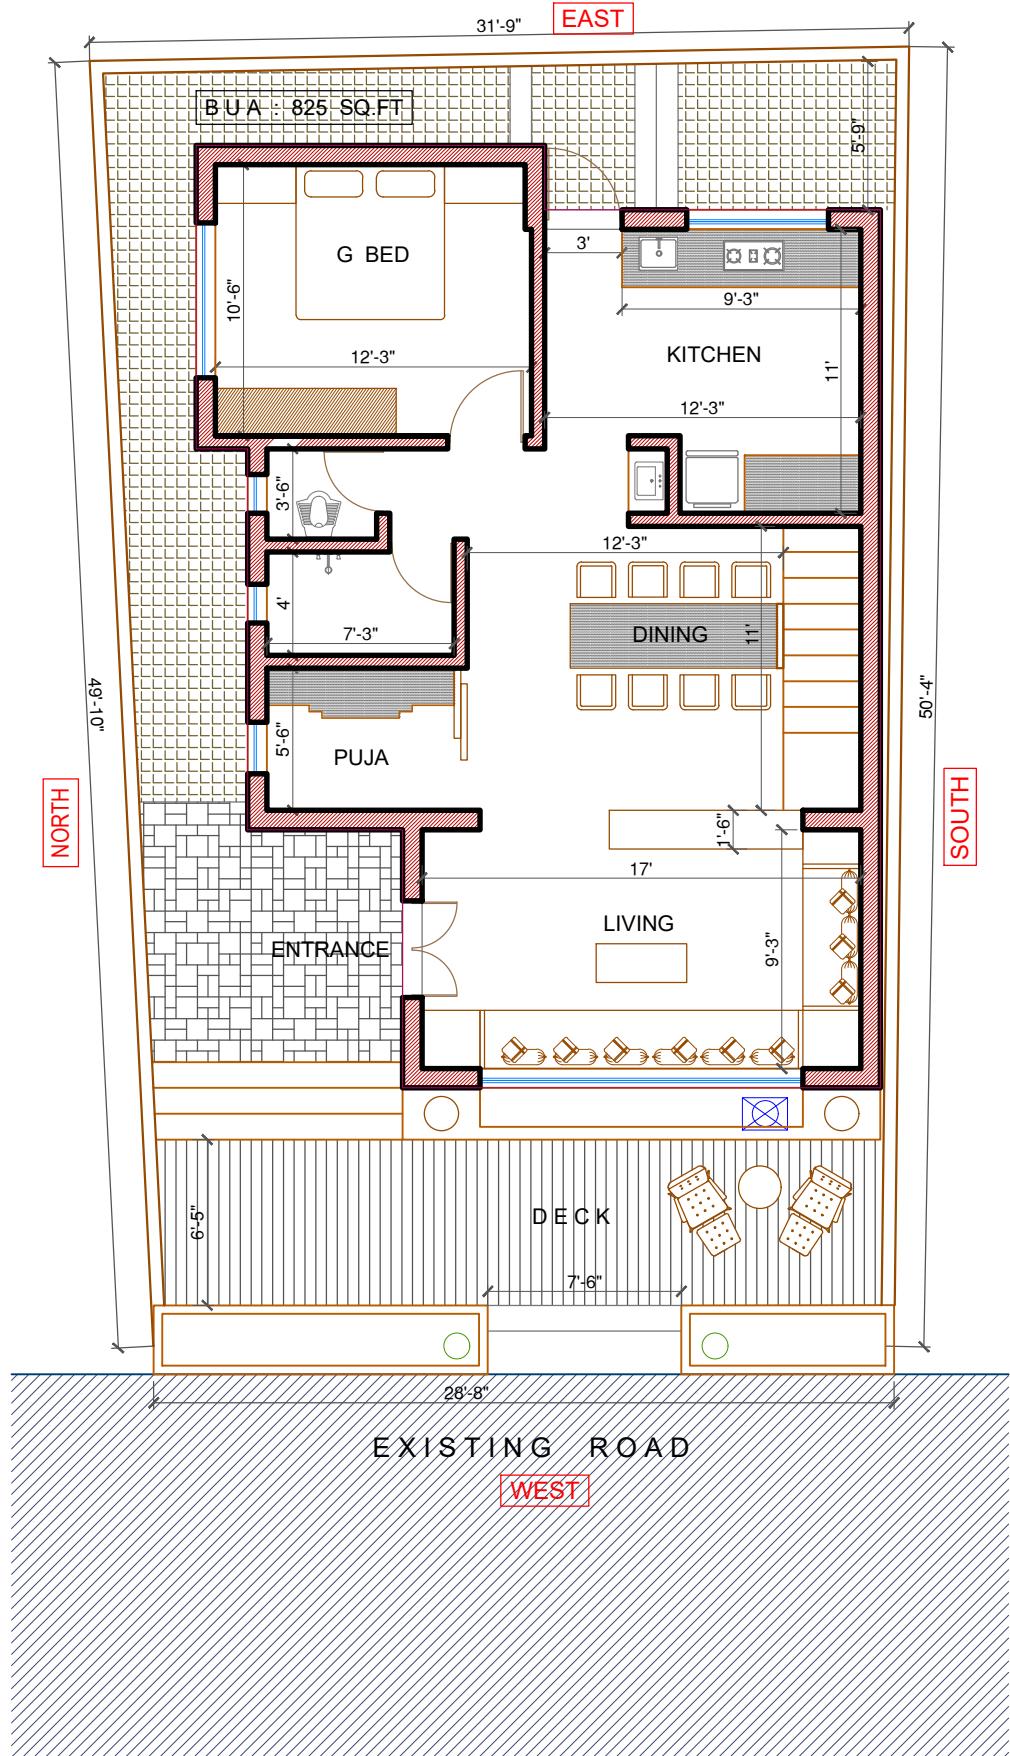

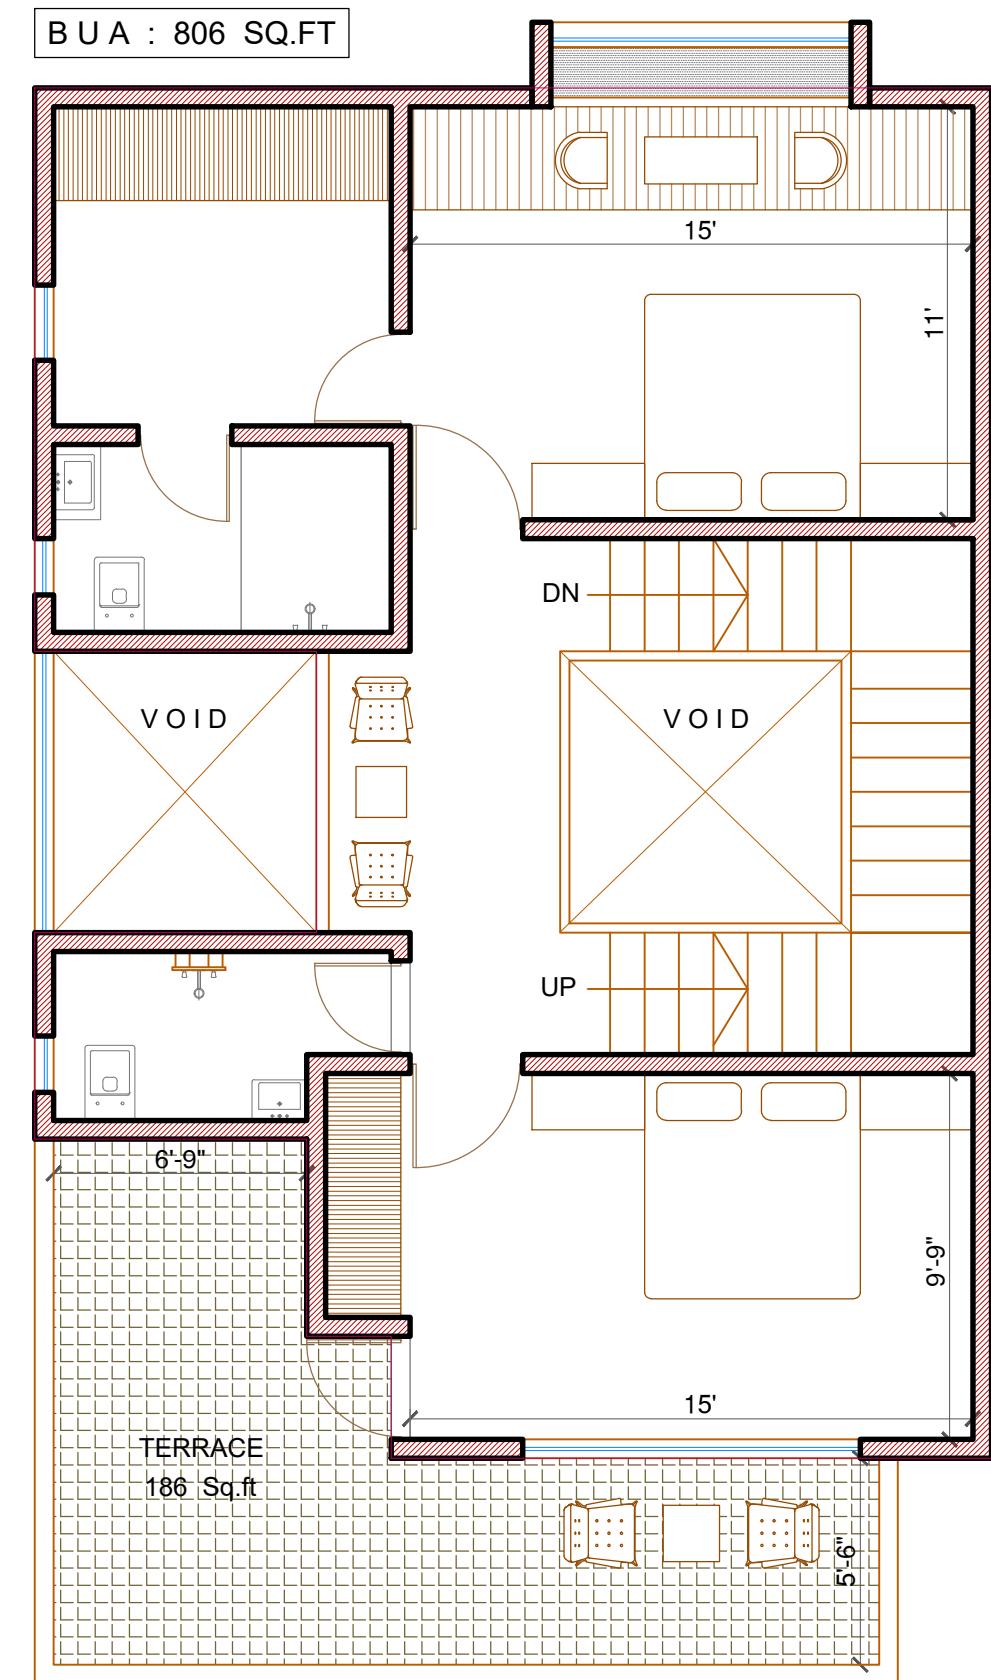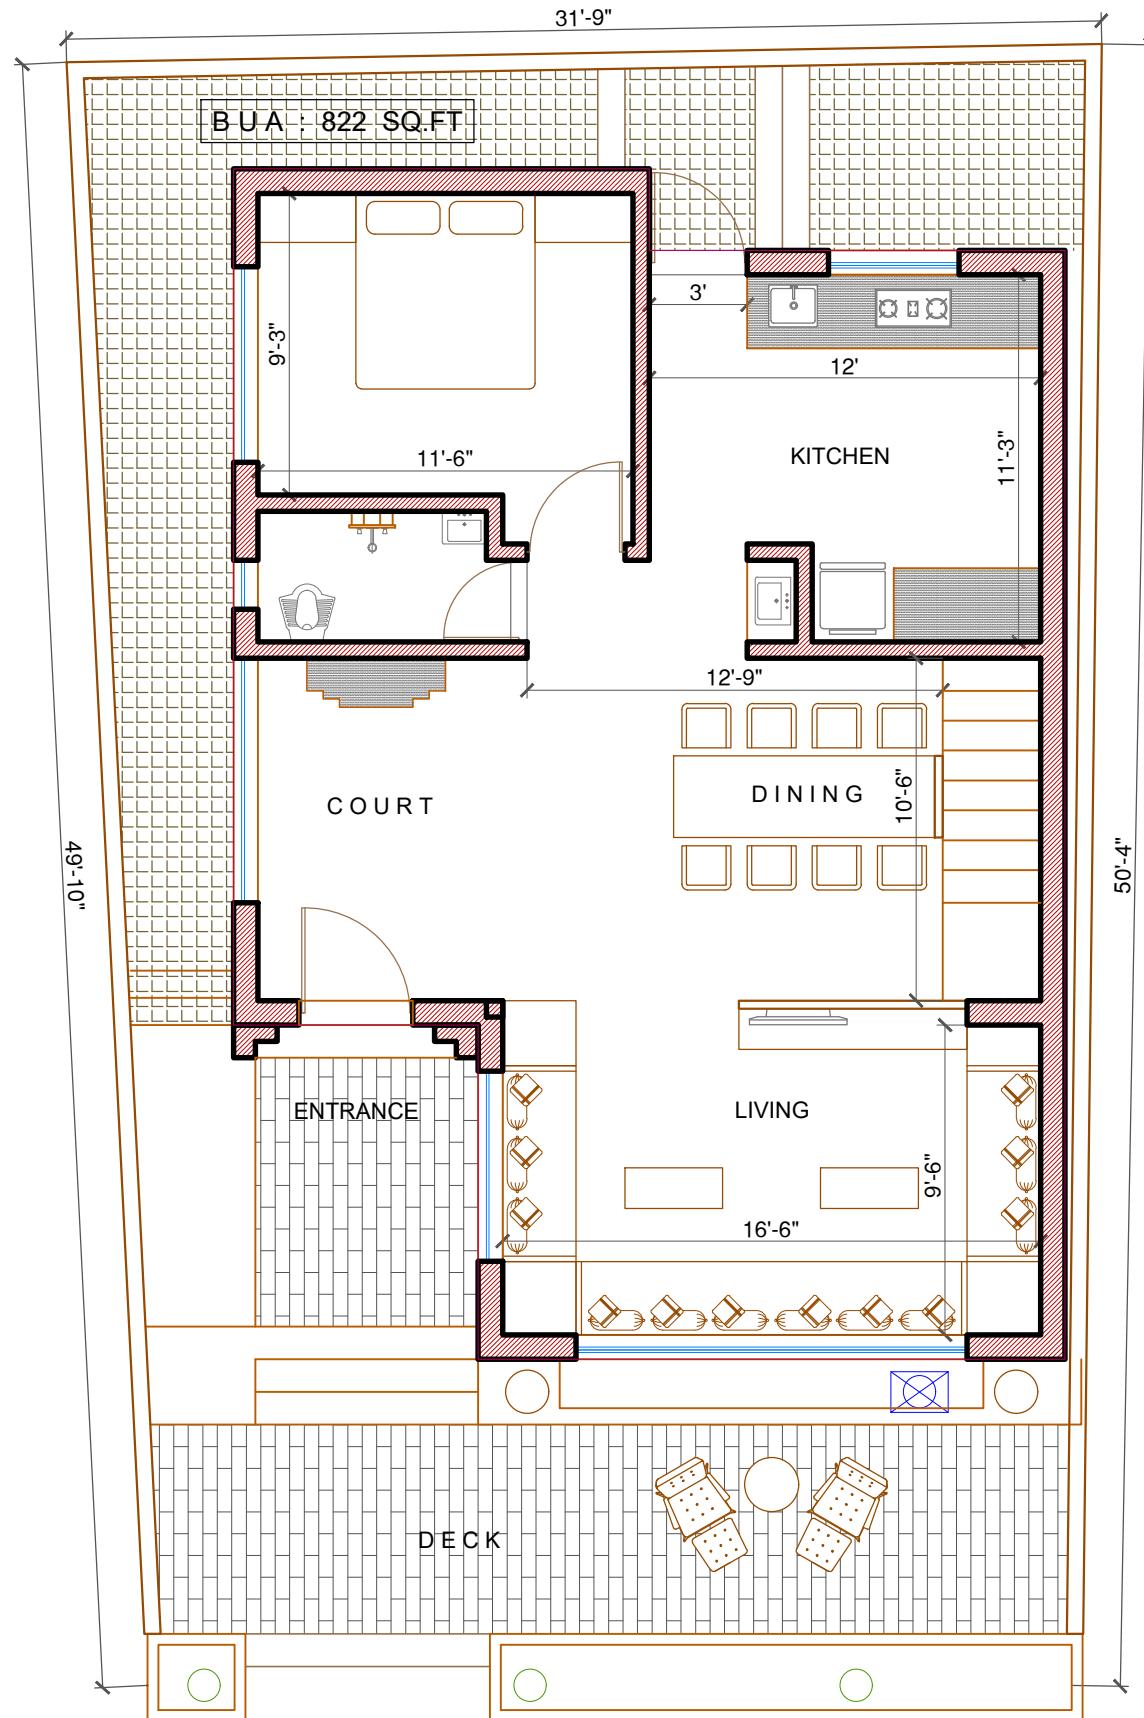

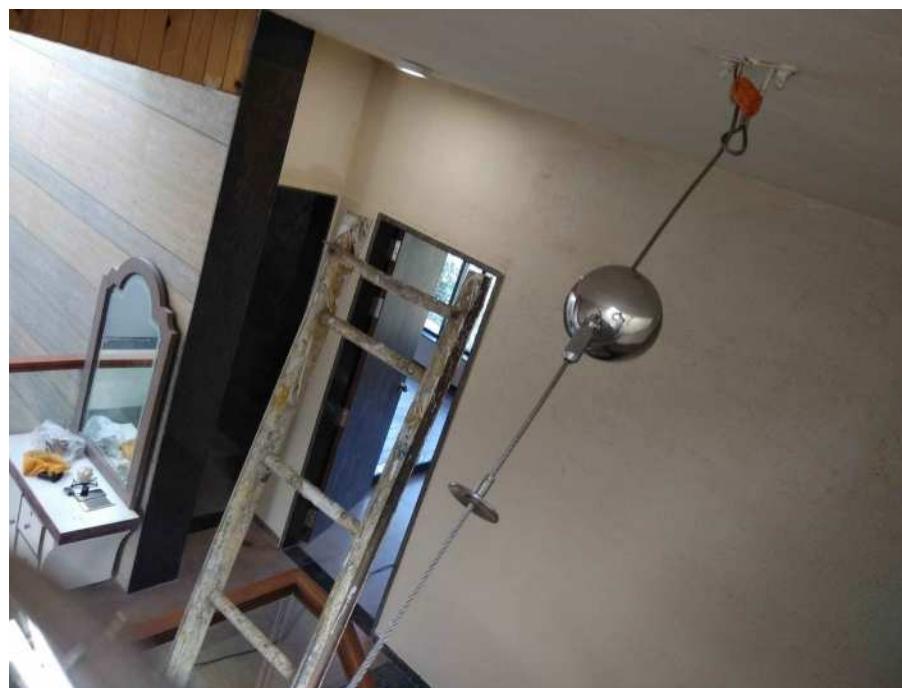

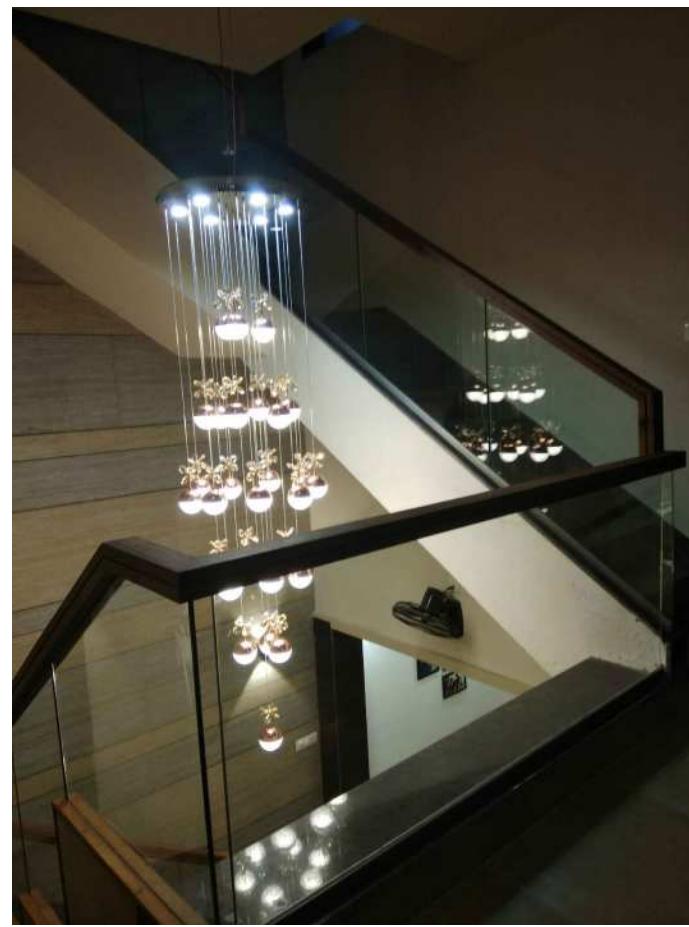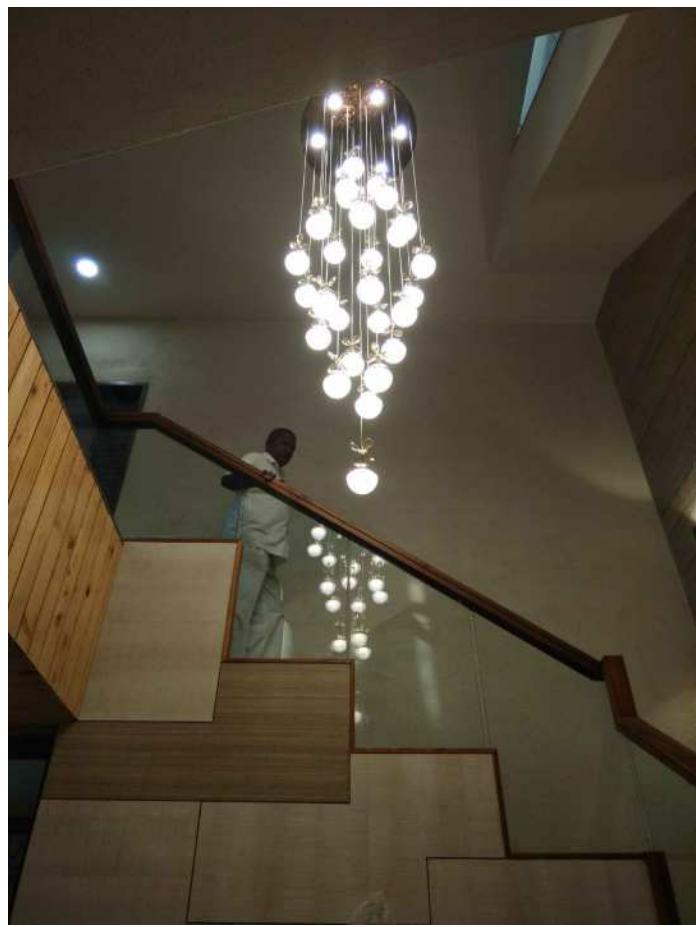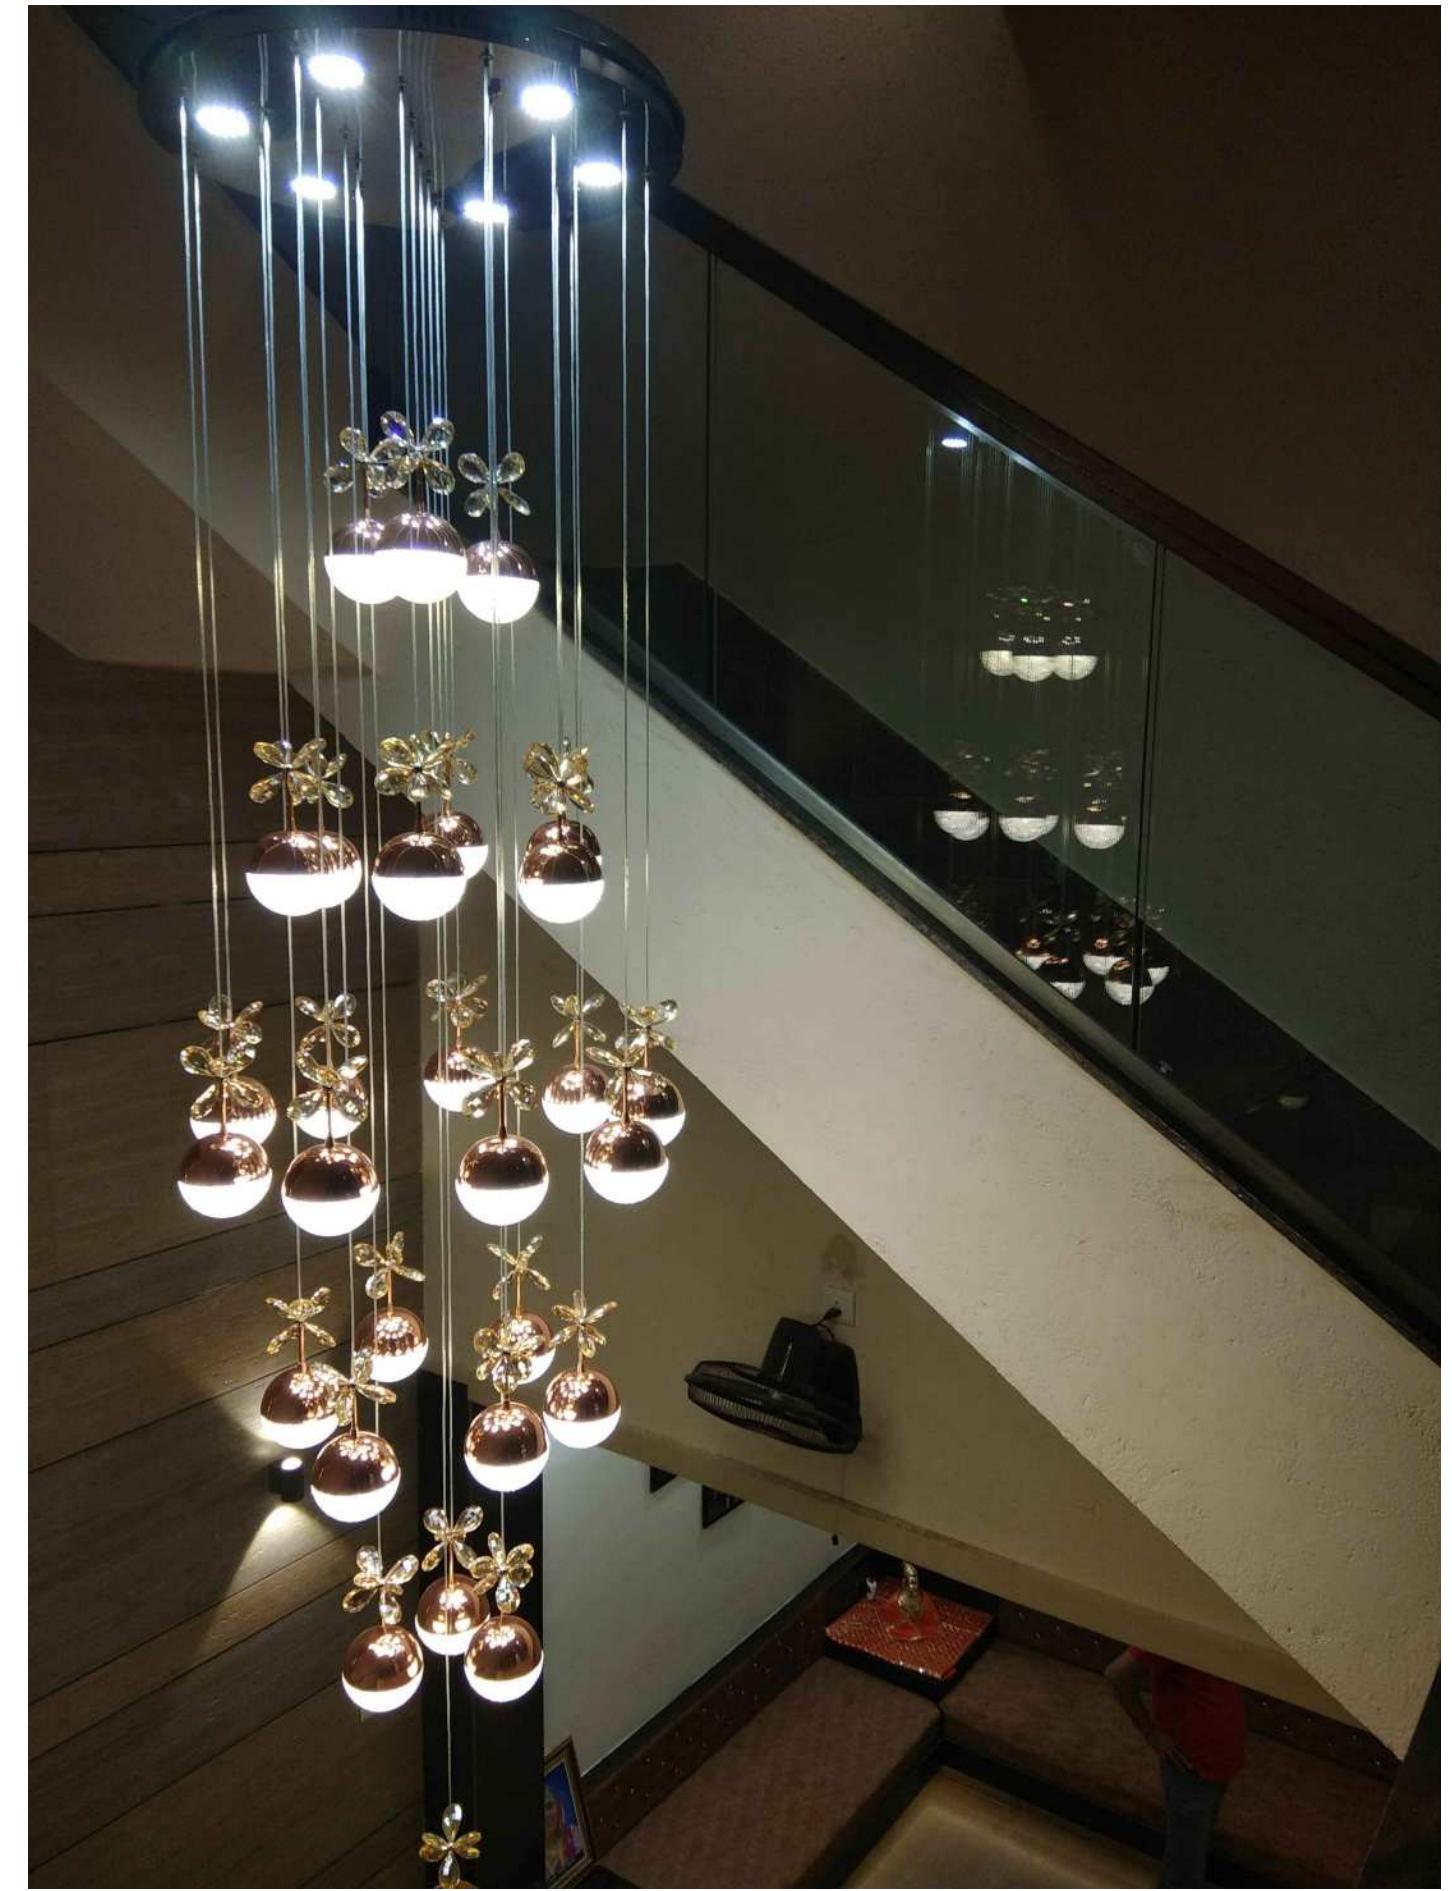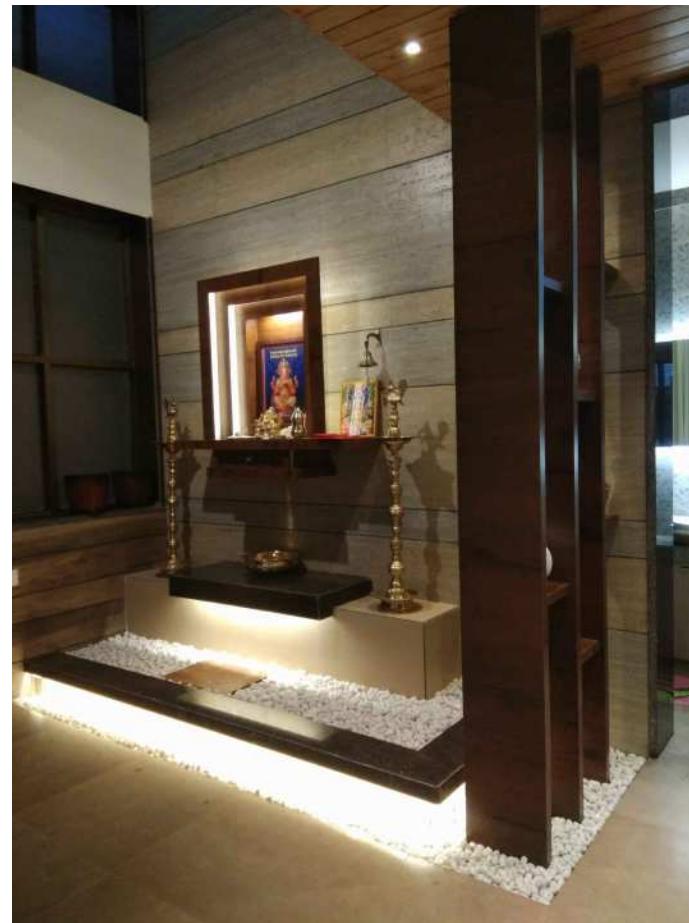

**VISHAL SOLANKI ASSOCIATES**


svdesign.v@gmail.com | 9920351604

Client : Mr. ARVIND UPADHYE


Proposed Bungalow Interior

Final Finished Work Photos

ASHIYA IQBAL KHAN

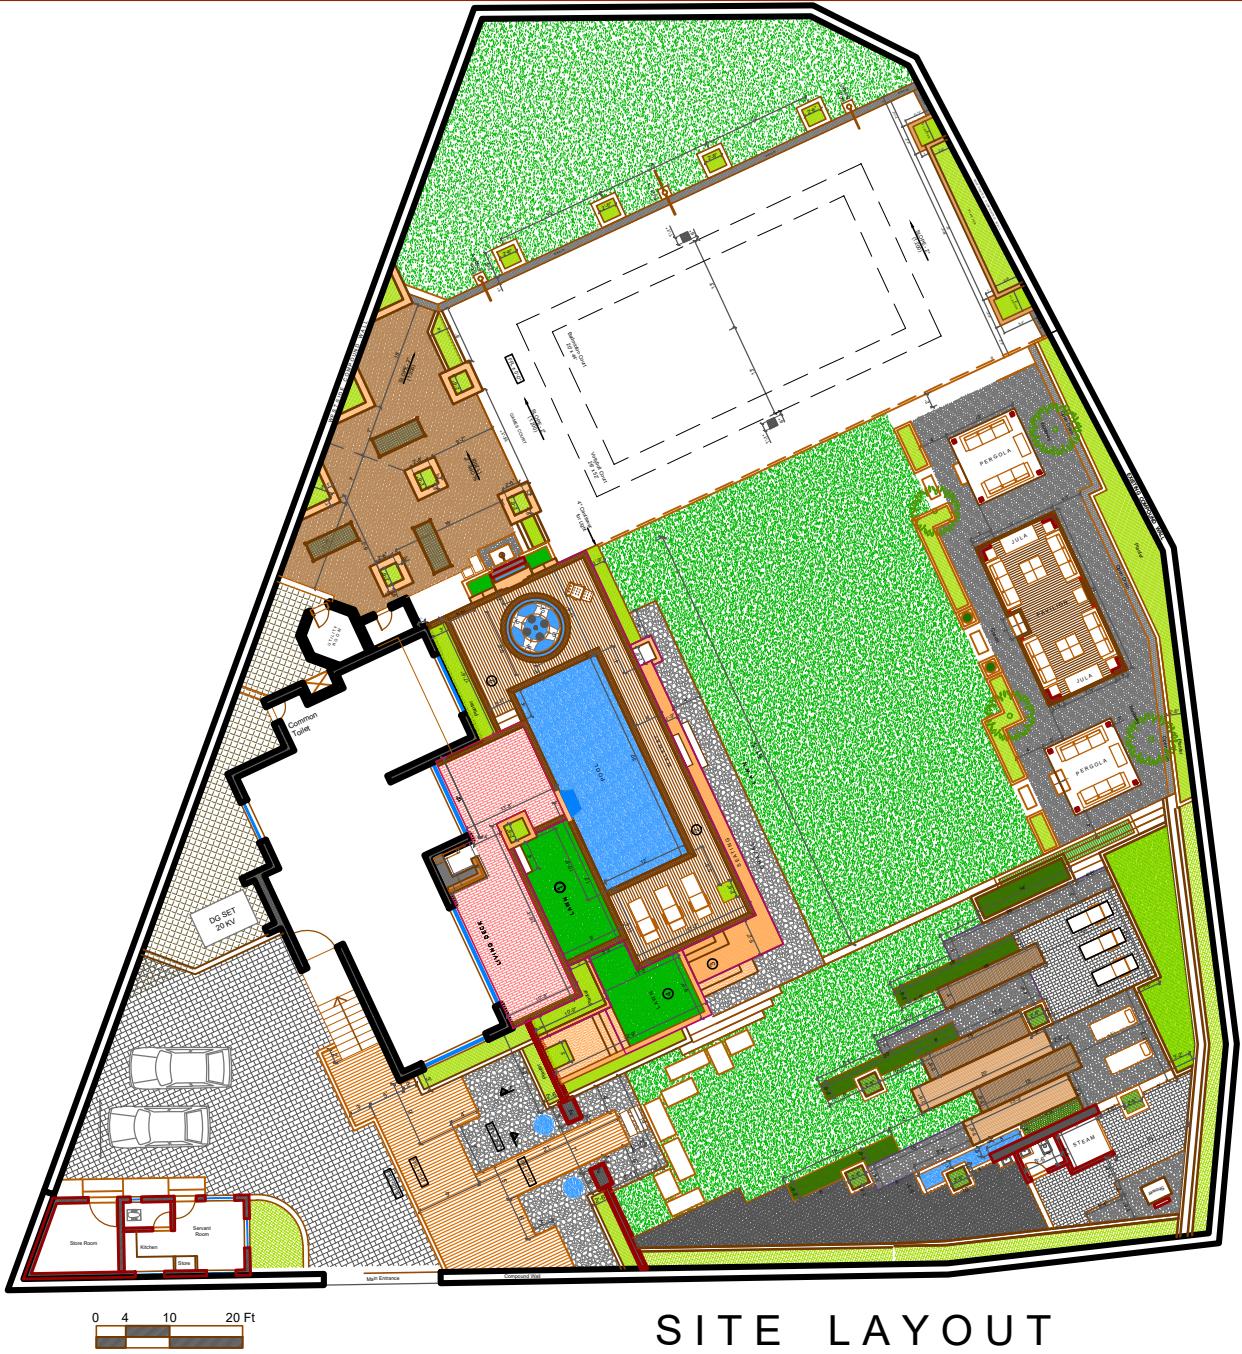

SITE LAYOUT

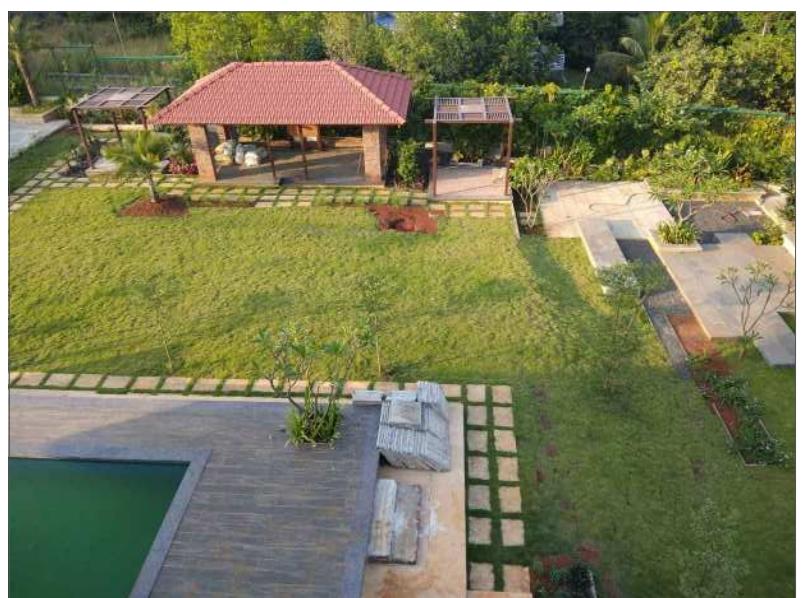

**VISHAL SOLANKI ASSOCIATES**

svdesign.v@gmail.com | 9920351604

Client : SUNEEL RAJPUT

Proposed Landscape Garden at Karjat



SITE VISIT





Stamp





Sign






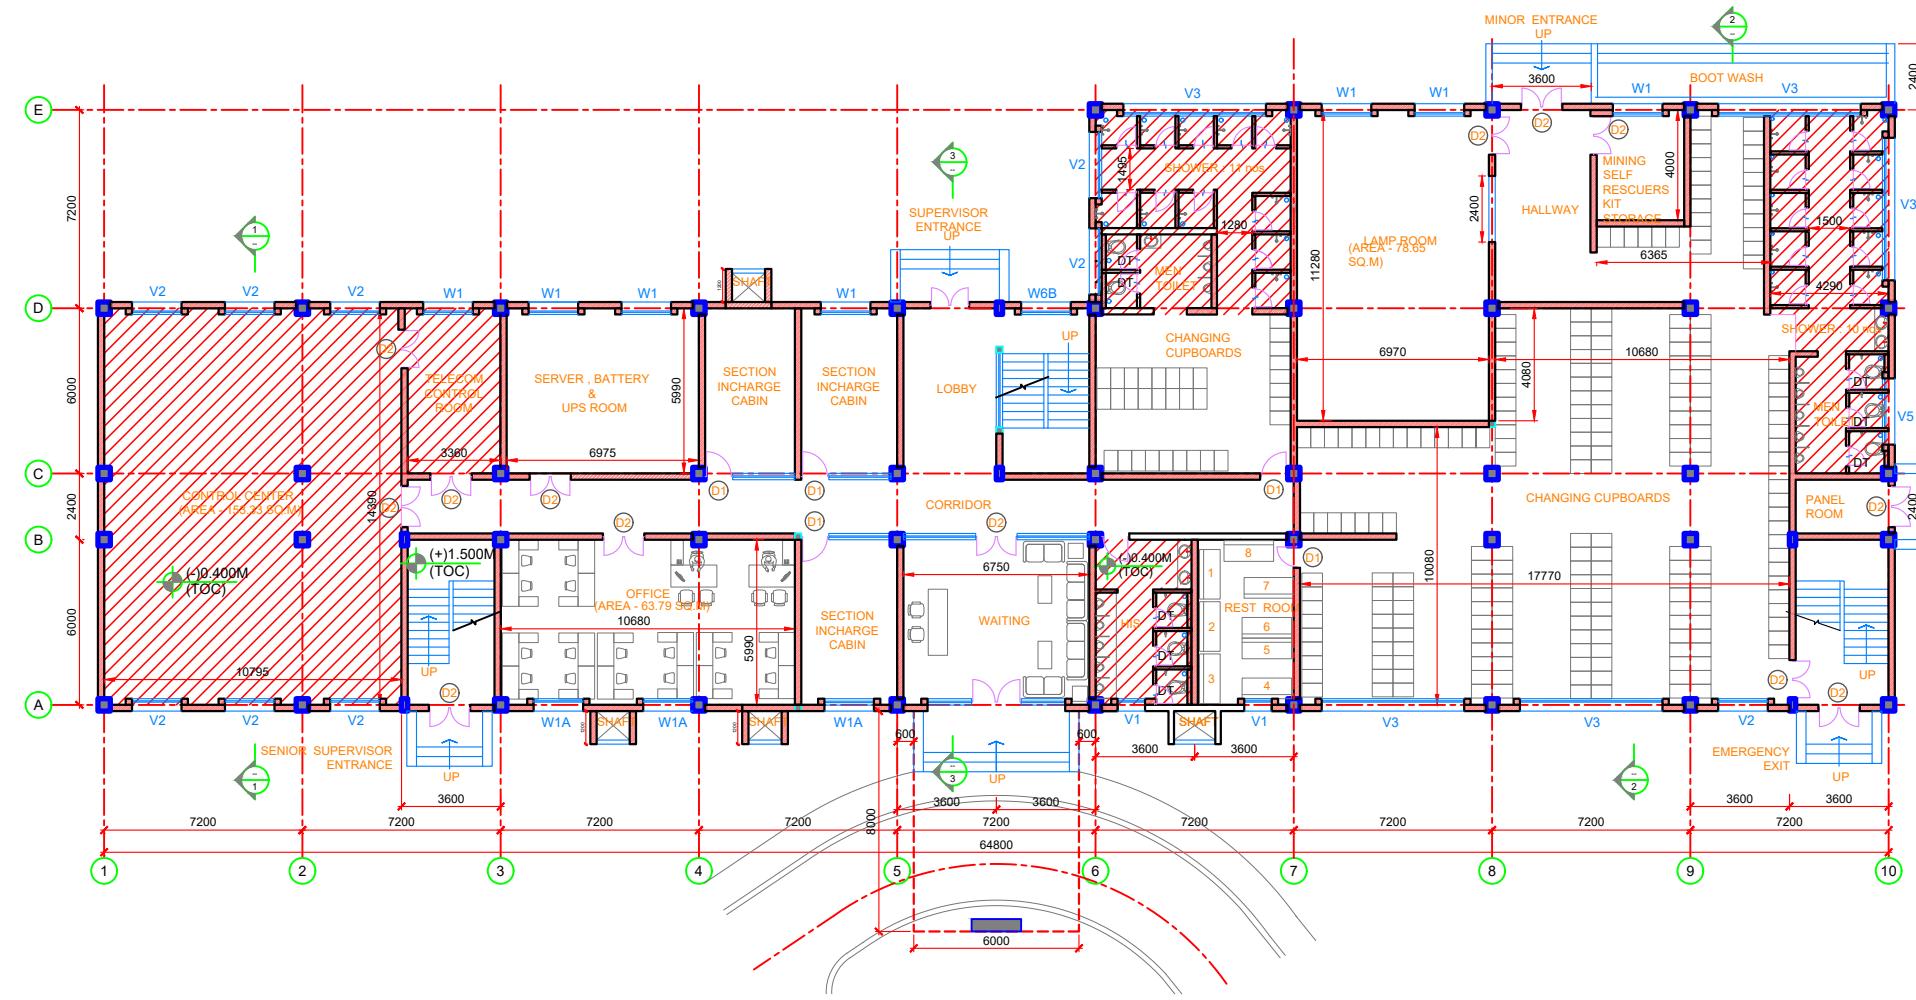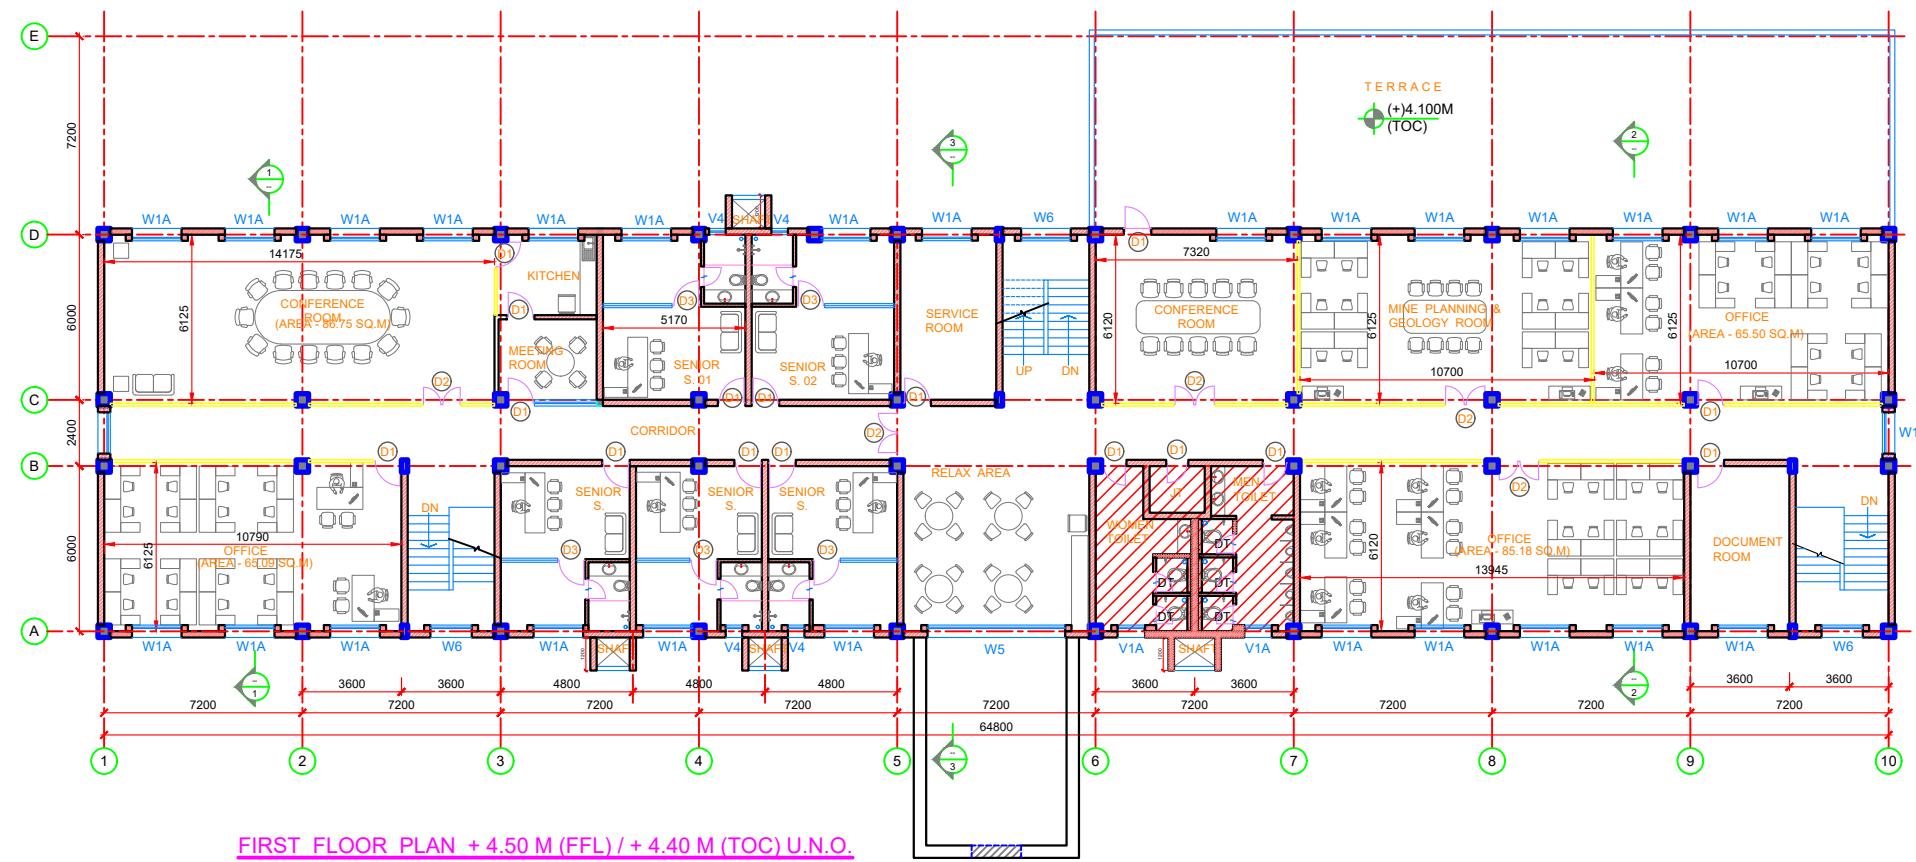


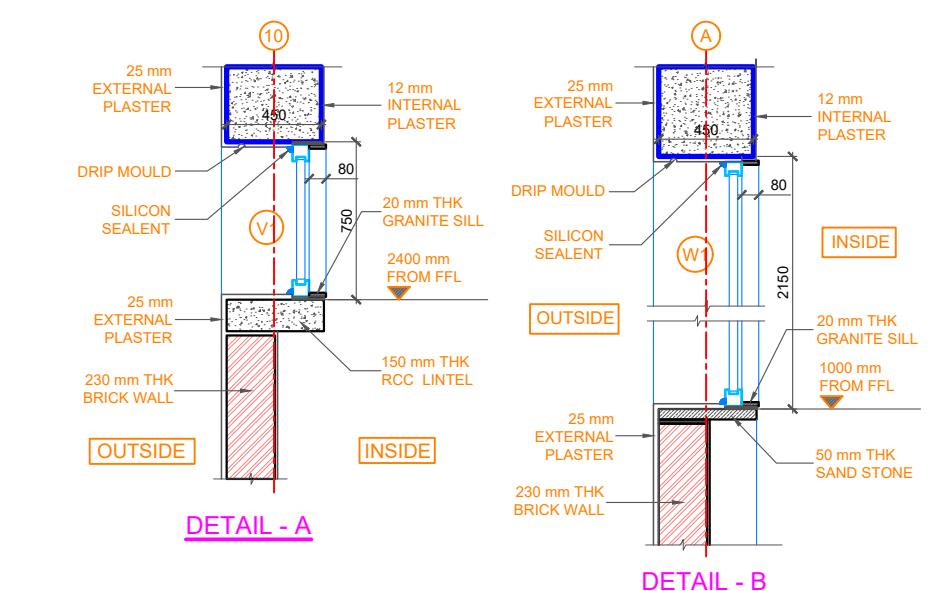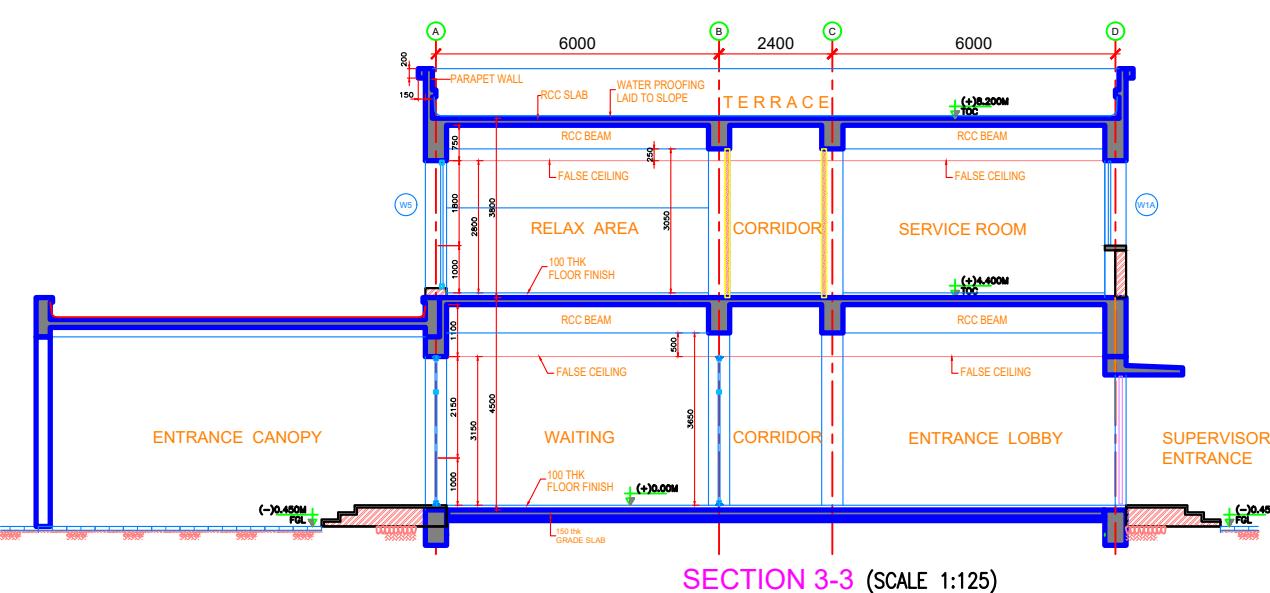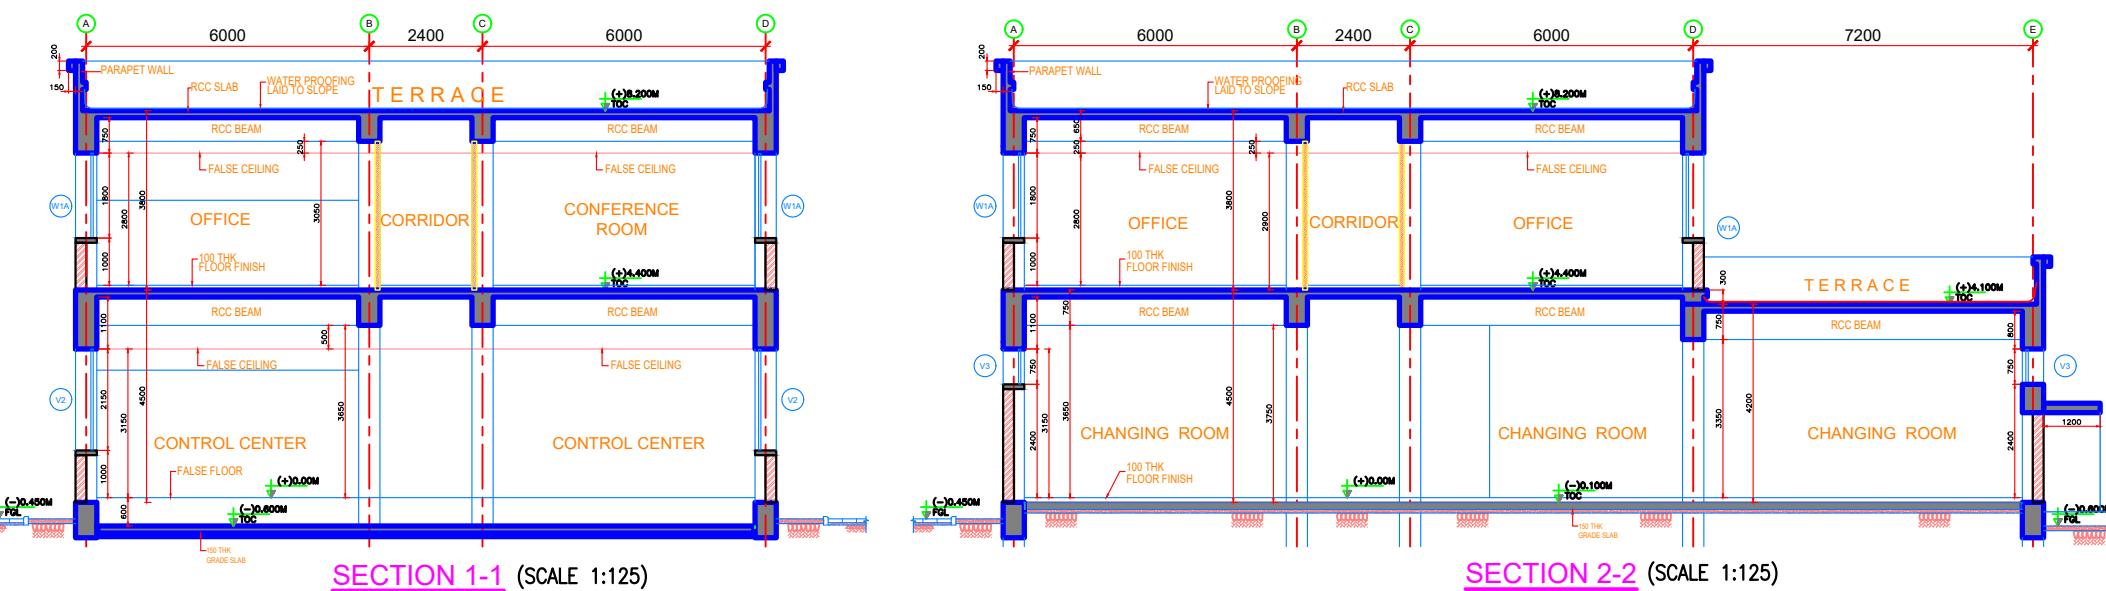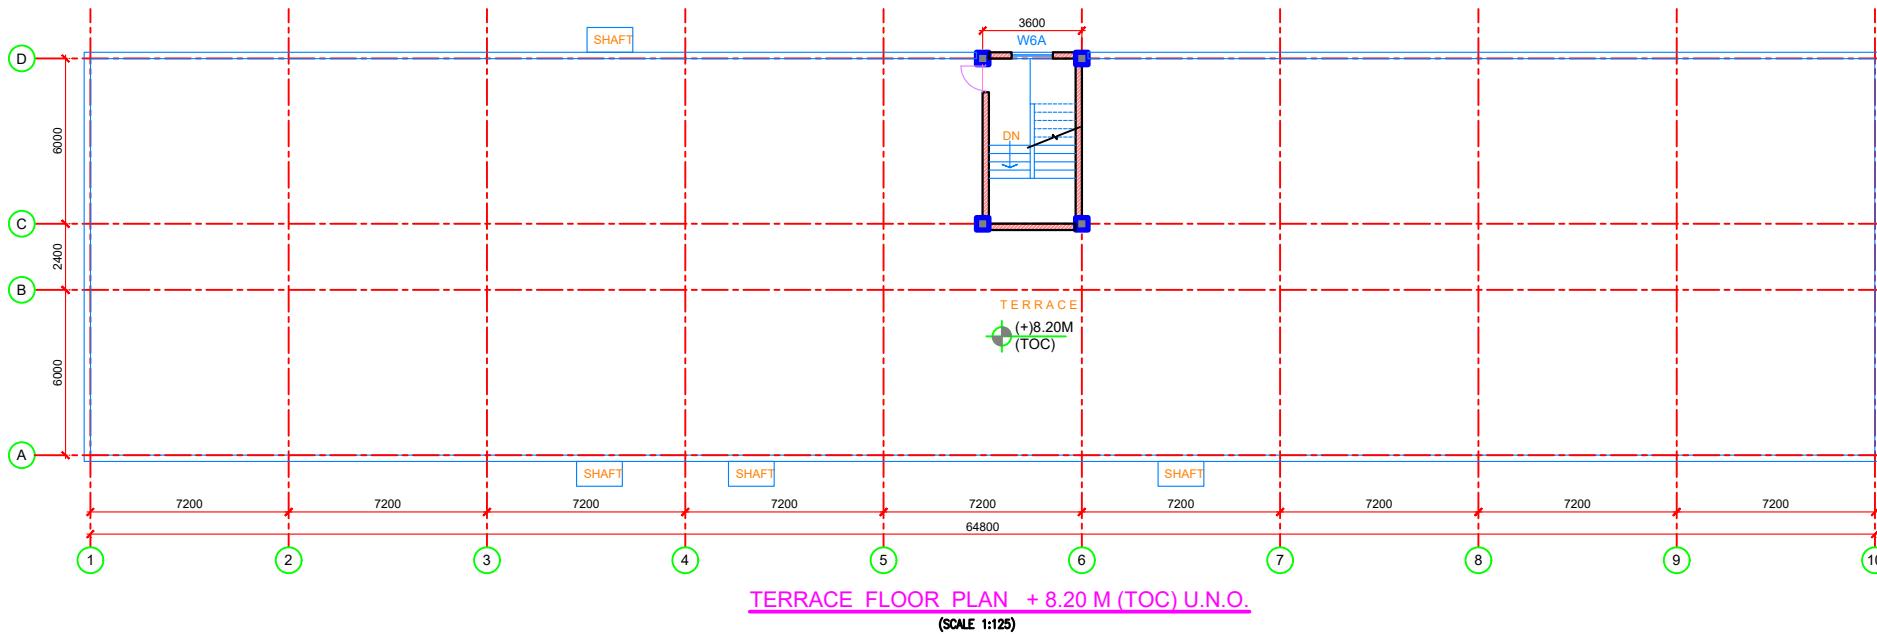

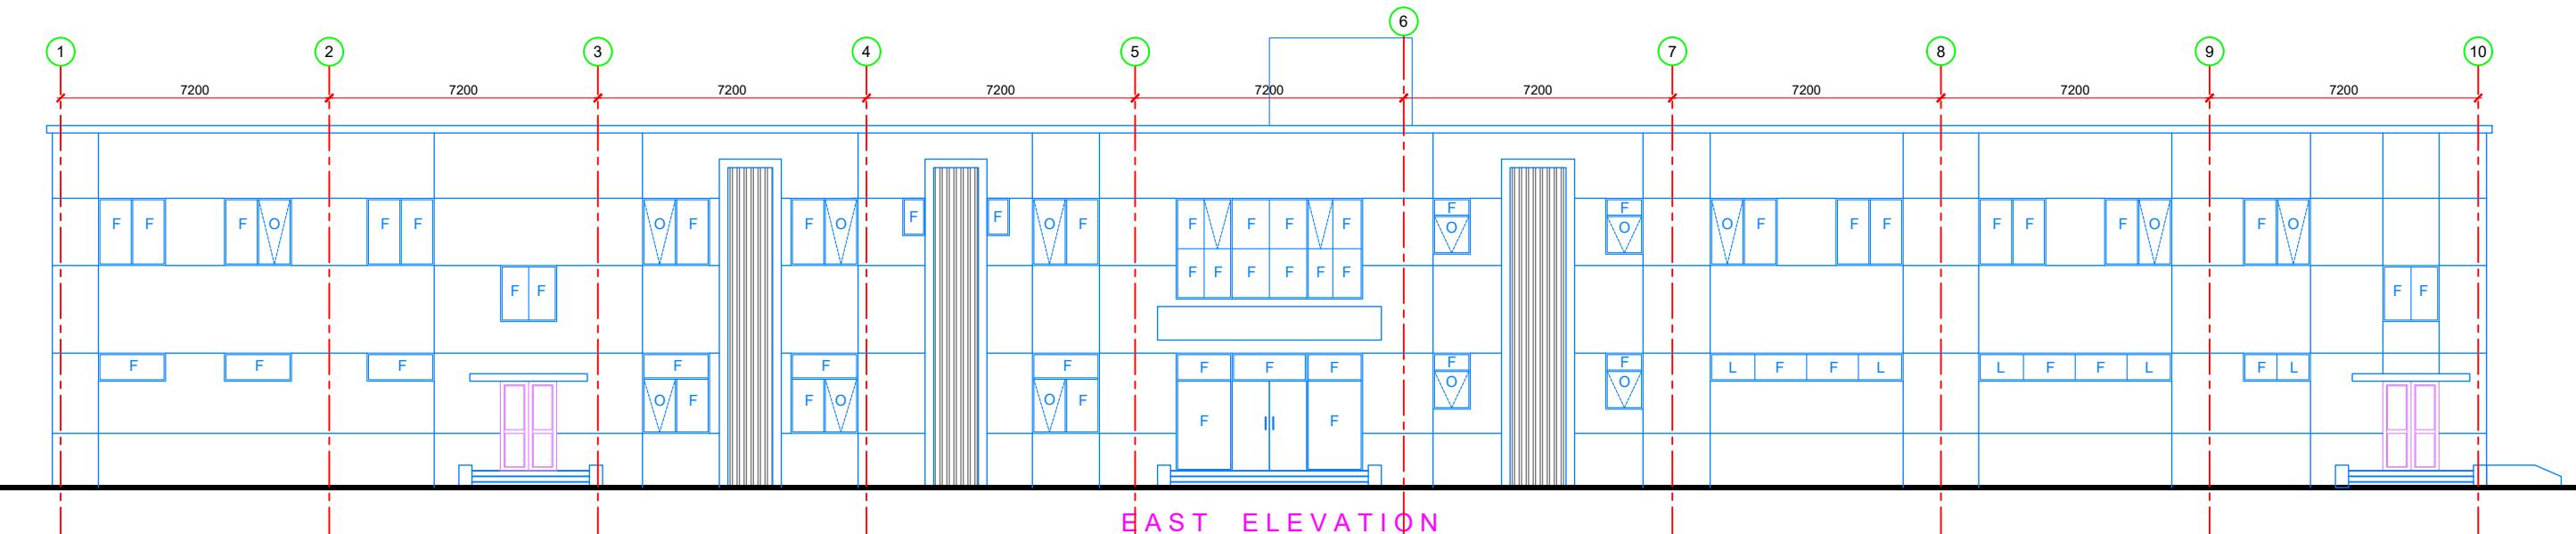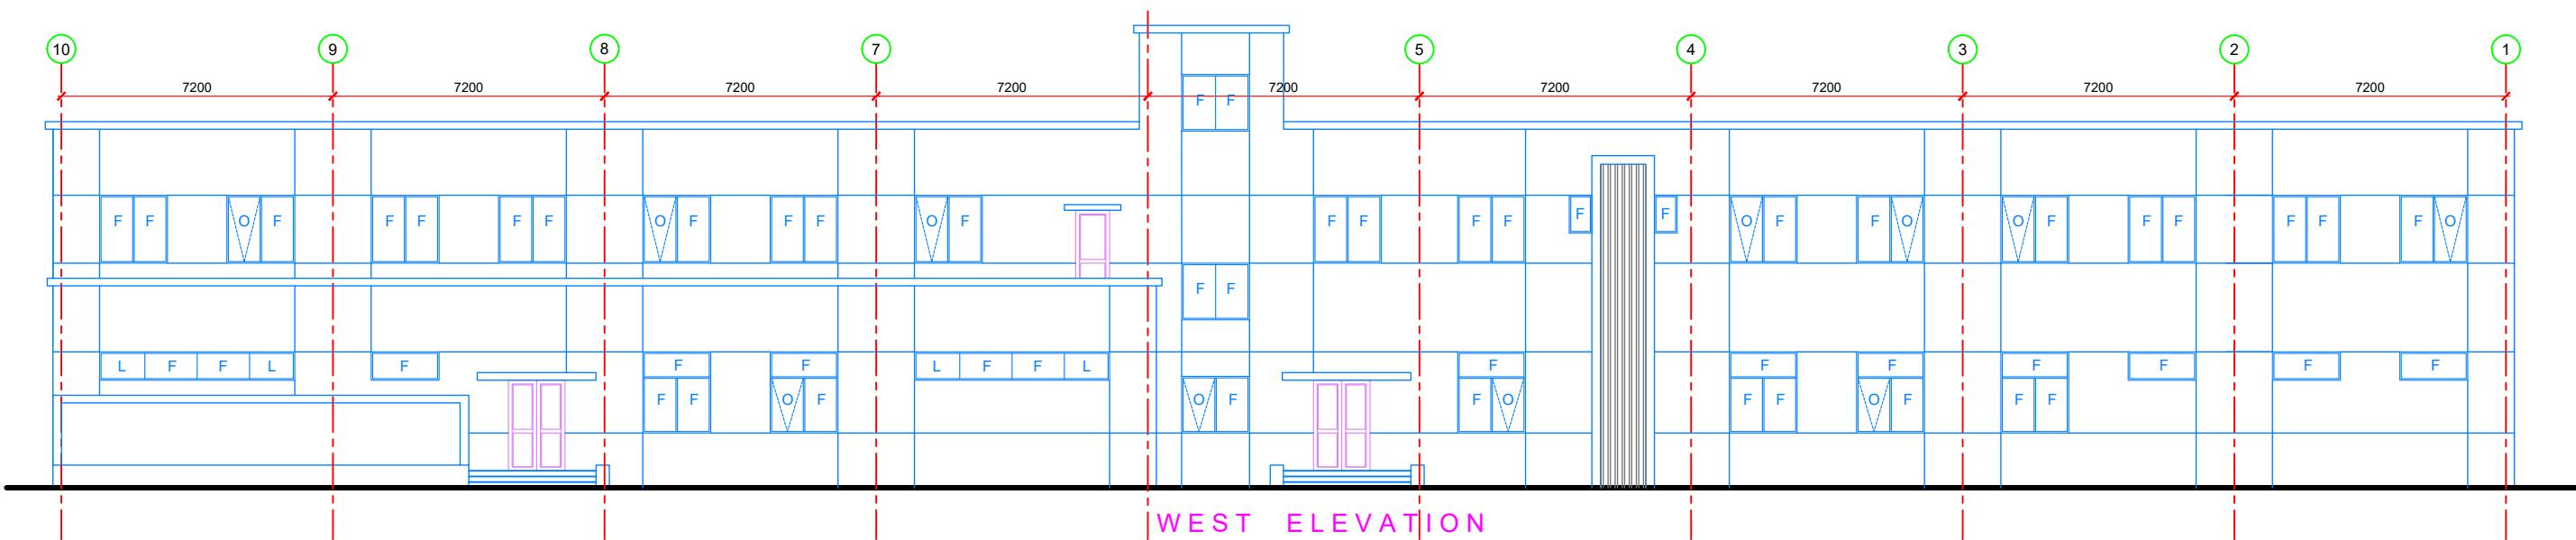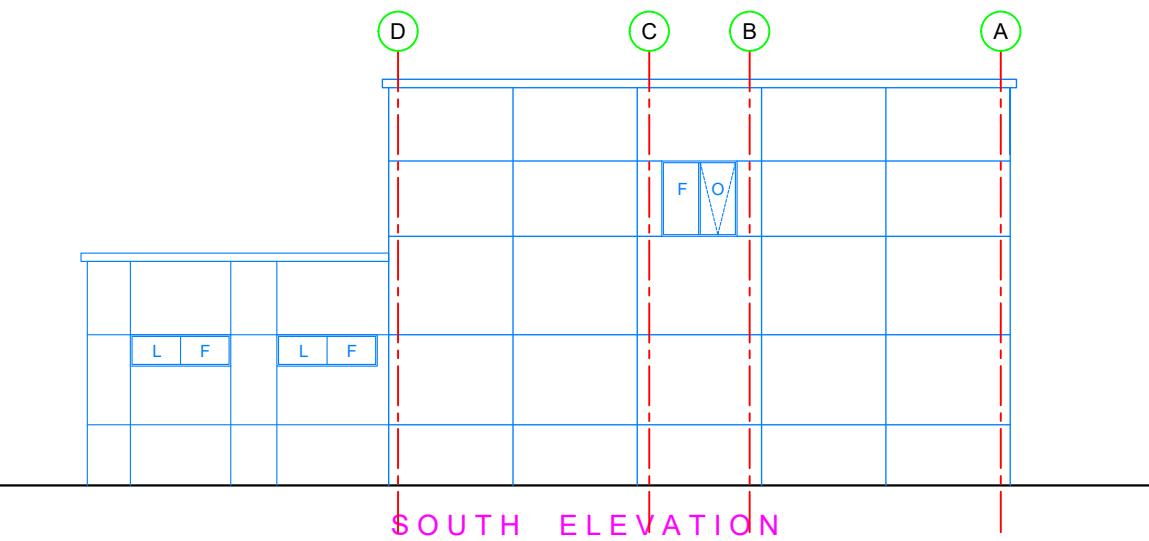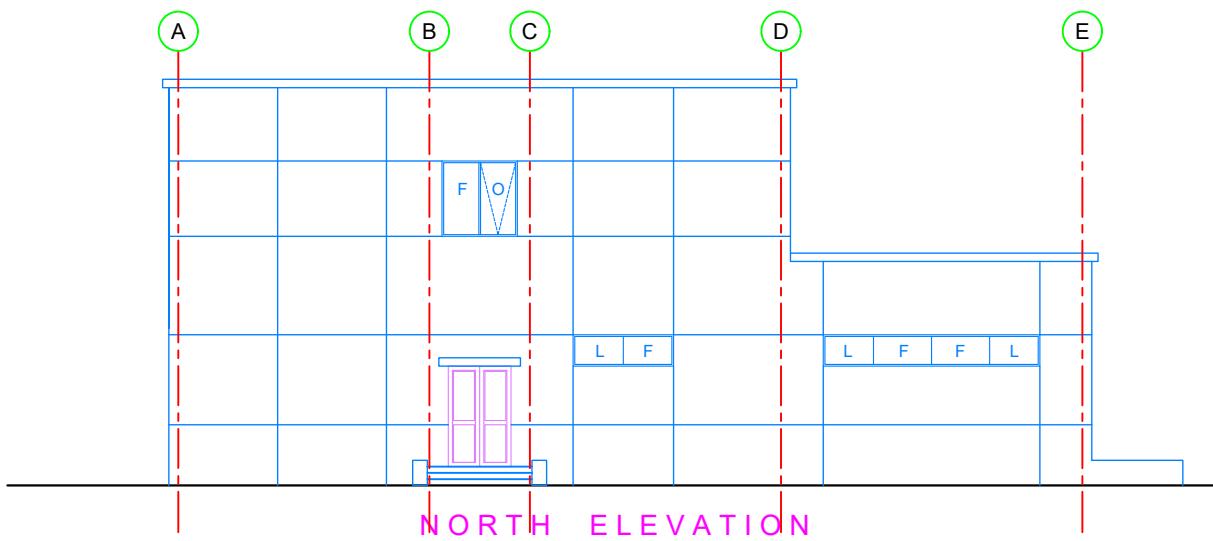

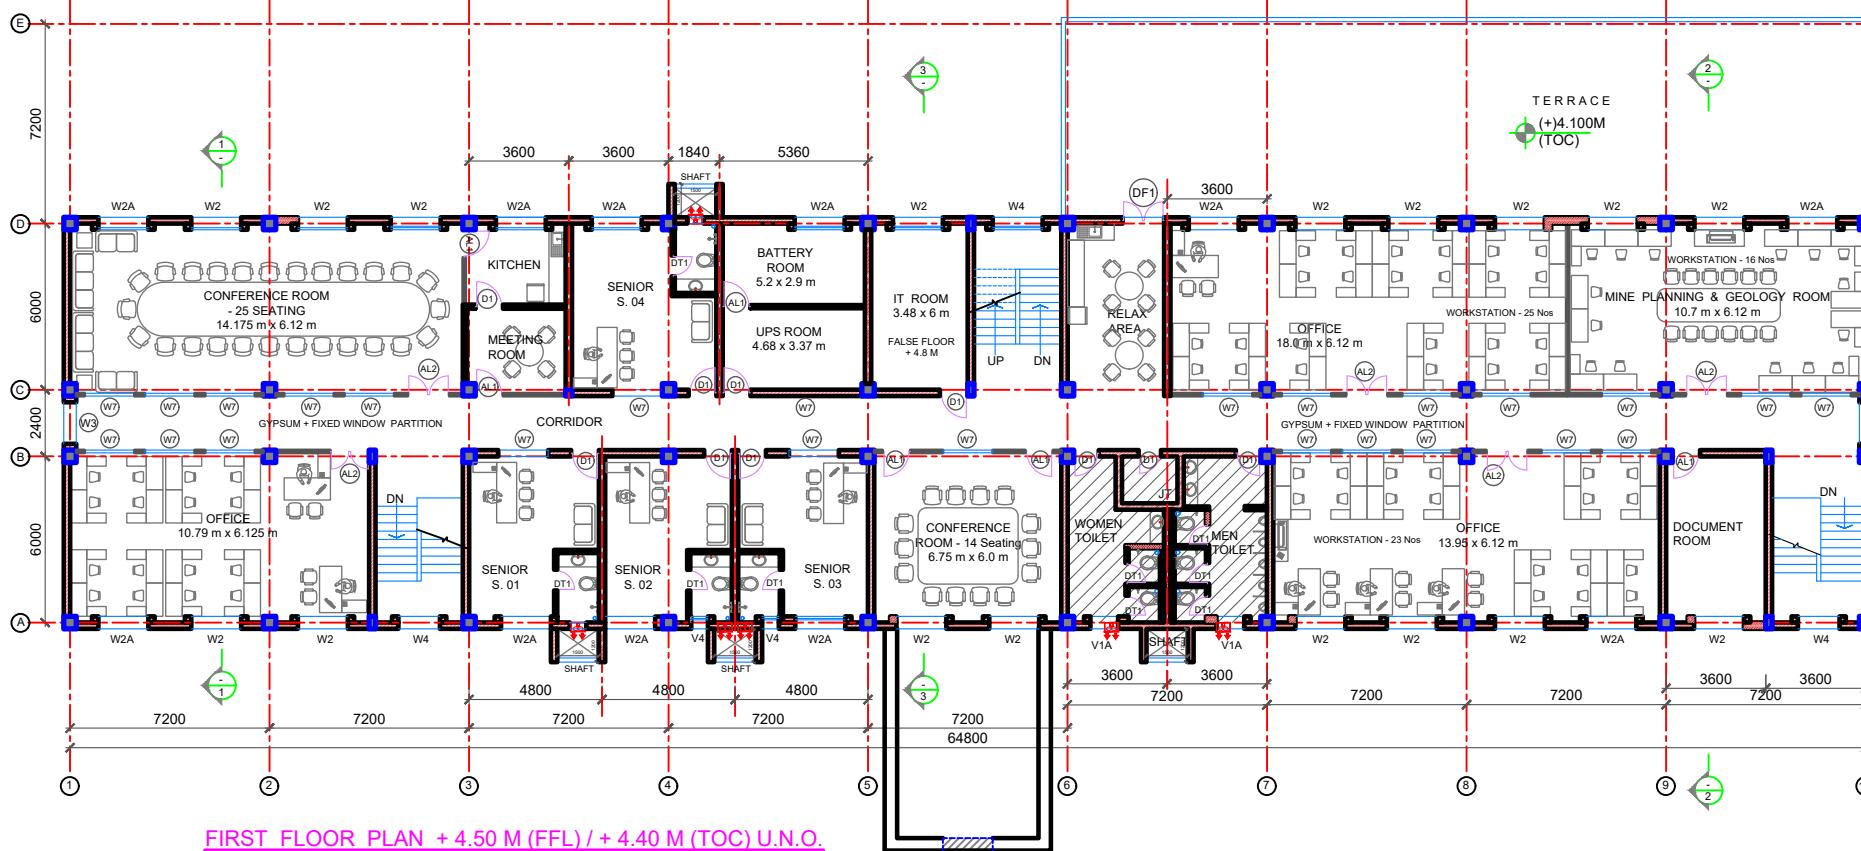

FIRST FLOOR PLAN + 4.50 M (FFL) / + 4.40 M (TOC) U.N.O.

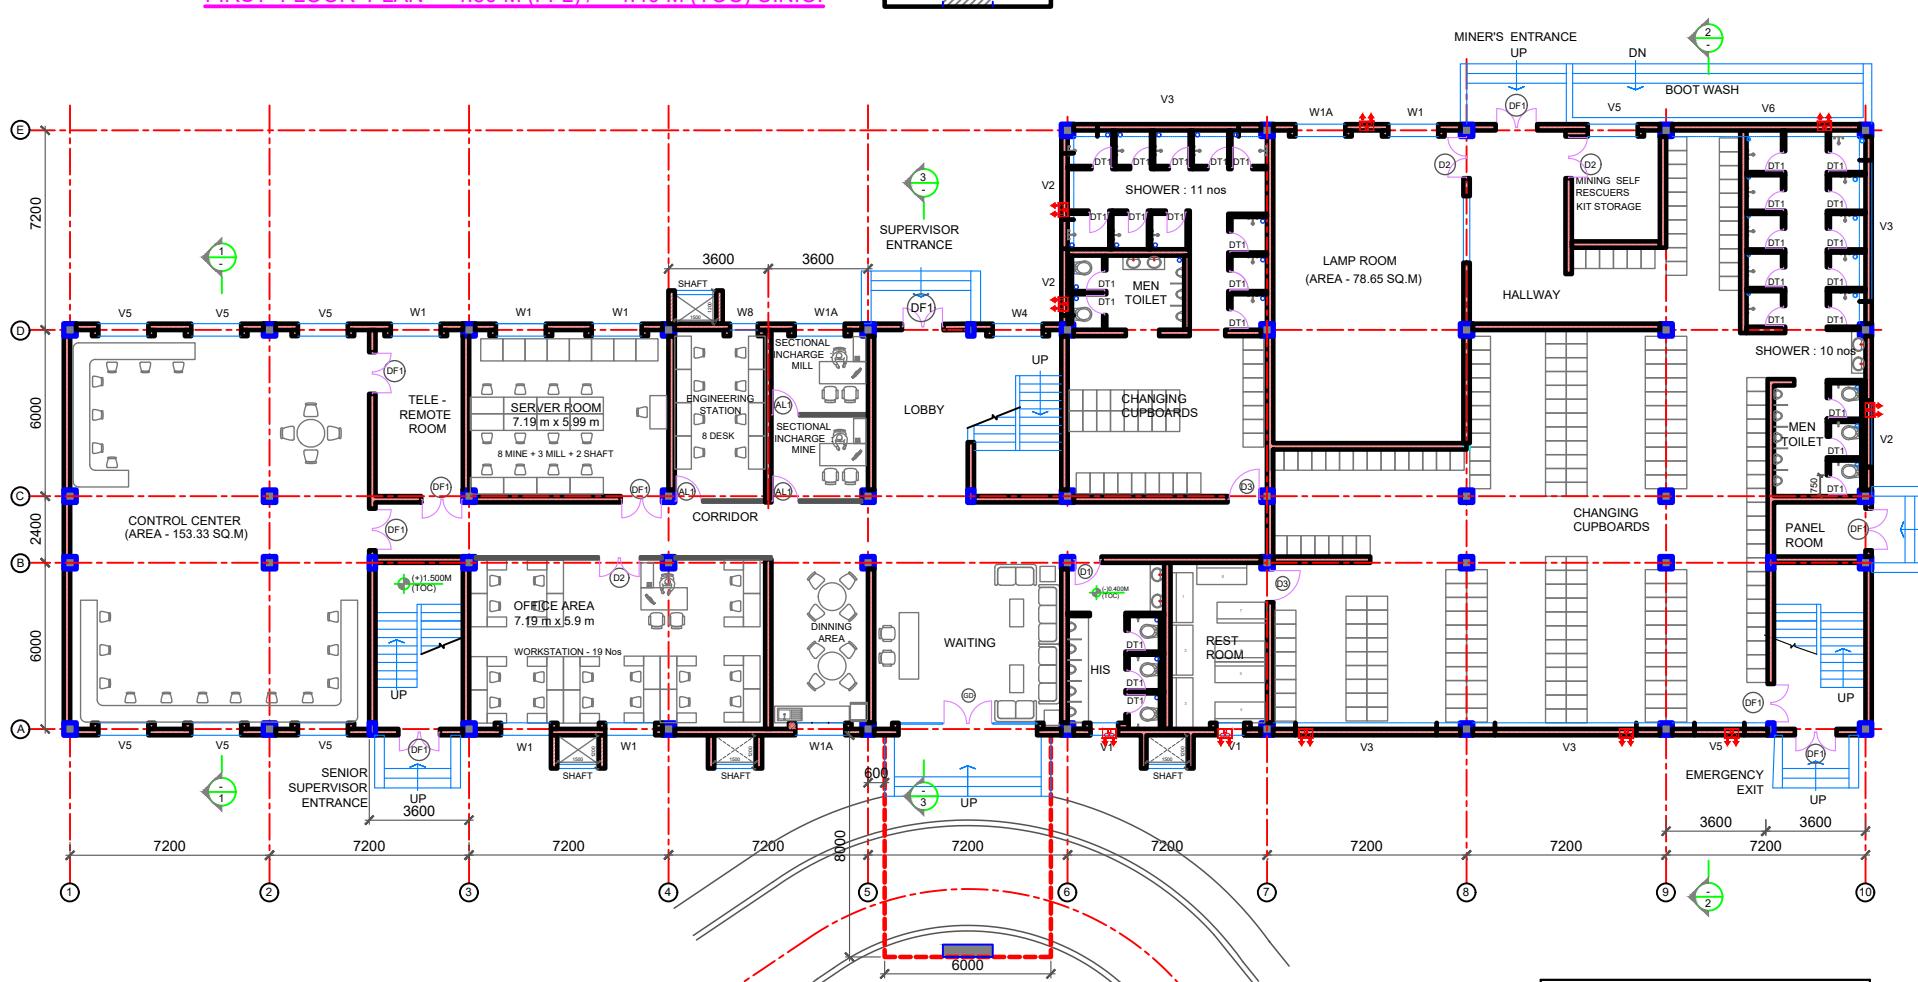

### OPTION - 1



GROUND FLOOR PLAN + 0.00 M (FFL) / -0.10 M (TOC) U.N.O.  
(SCALE 1:125)

#### DOOR & WINDOW SCHEDULE

No	SILL	WIDTH	HEIGHT	DESCRIPTION
W1	1000	1800	2150	Aluminium Fixed Window
V1	1650	1000	1500	Aluminium Fixed Window - Louvers
V1A	1300	1000	1500	Aluminium Fixed Window - Louvers
W2	1000	1800	1800	Aluminium Fixed Window
V2	2400	5100	750	Aluminium Fixed Window - Louvers
W3	1000	1500	1800	Aluminium Fixed + Openable Window
V3	1800	600	1000	Aluminium Fixed Window
V4	2400	1800	750	Aluminium Fixed Window - Louvers
V5	2400	1800	750	Aluminium Fixed Window - Louvers
V6	2400	6750	750	Aluminium Fixed Window - Louvers

#### DOOR & WINDOW SCHEDULE

No	SILL	WIDTH	HEIGHT	DESCRIPTION
D1	1000	2400	General Purpose Steel Door	
D2	1500	2400	General Purpose Steel Door	
D3	1200	2400	General Purpose Steel Door	
DF1	1500	2400	Fire Rated HMP5 Door	
DT1	750	2100	General Purpose Metal Door	
AL1	1000	2400	Aluminium Half Glazed Door	
AL2	1500	2400	Aluminium Half Glazed Door	
GD	1800	2400	Glass Door	



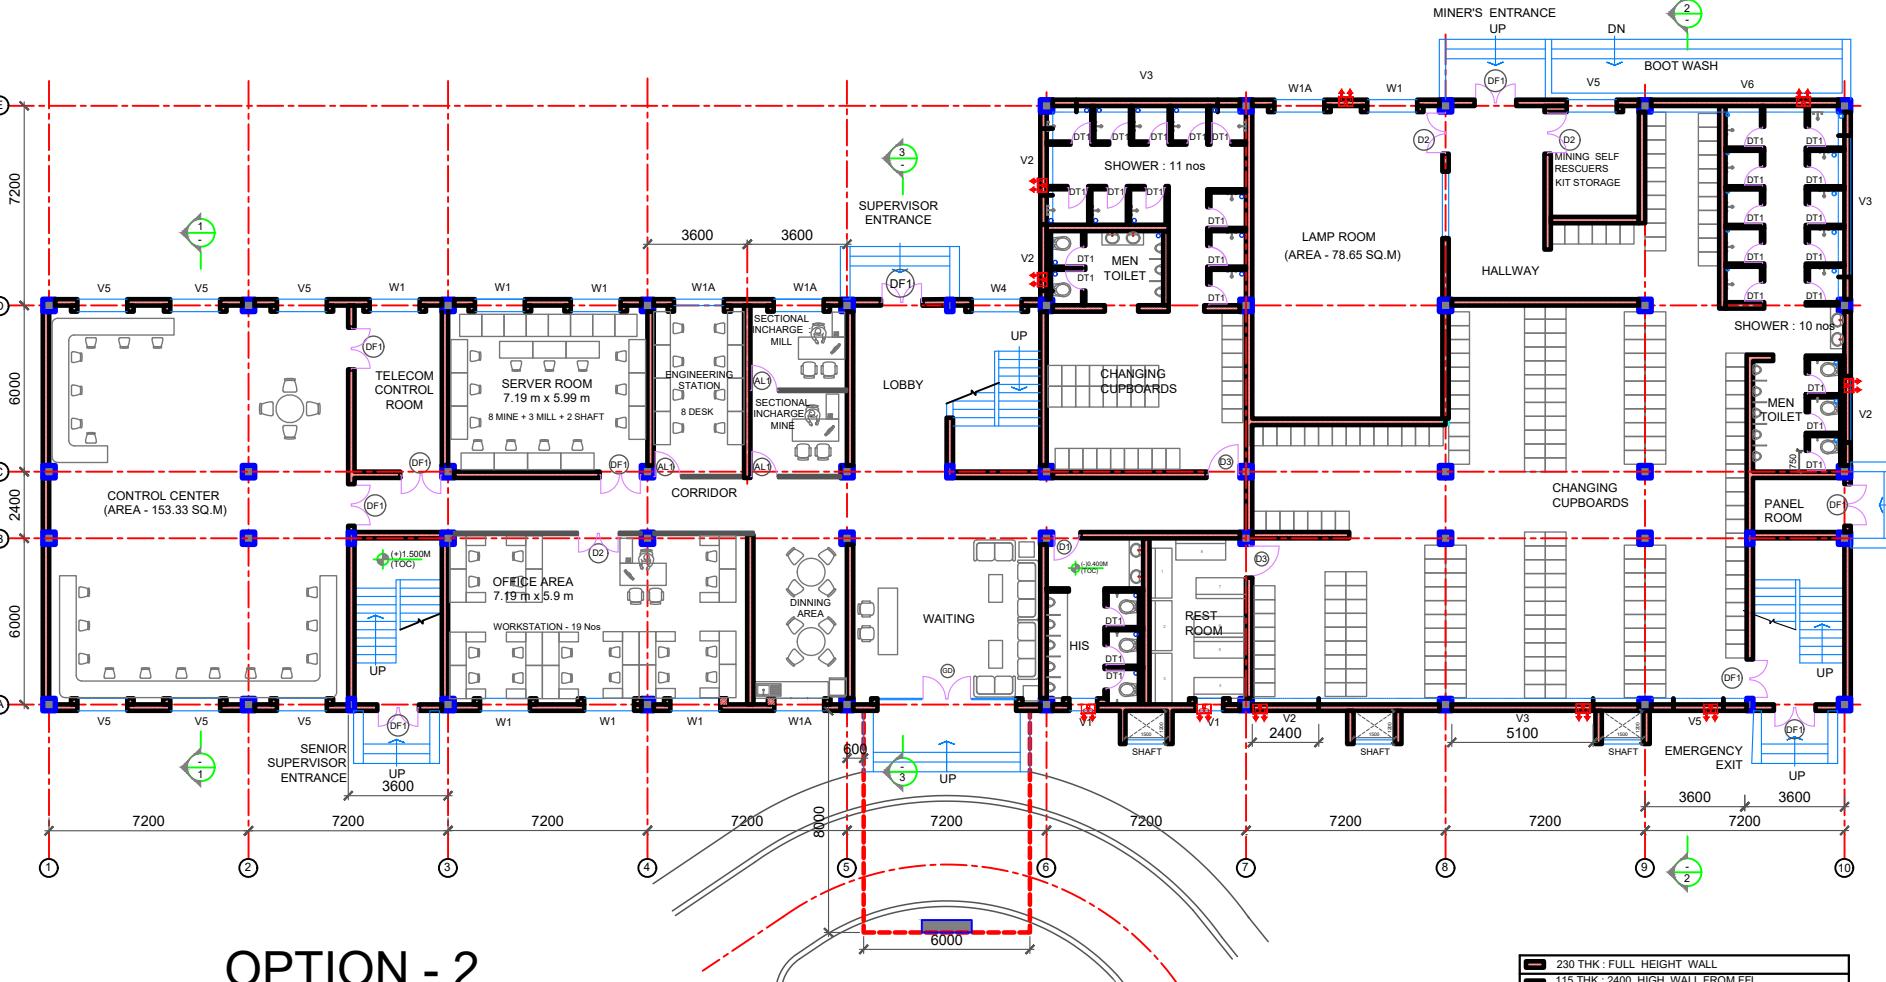
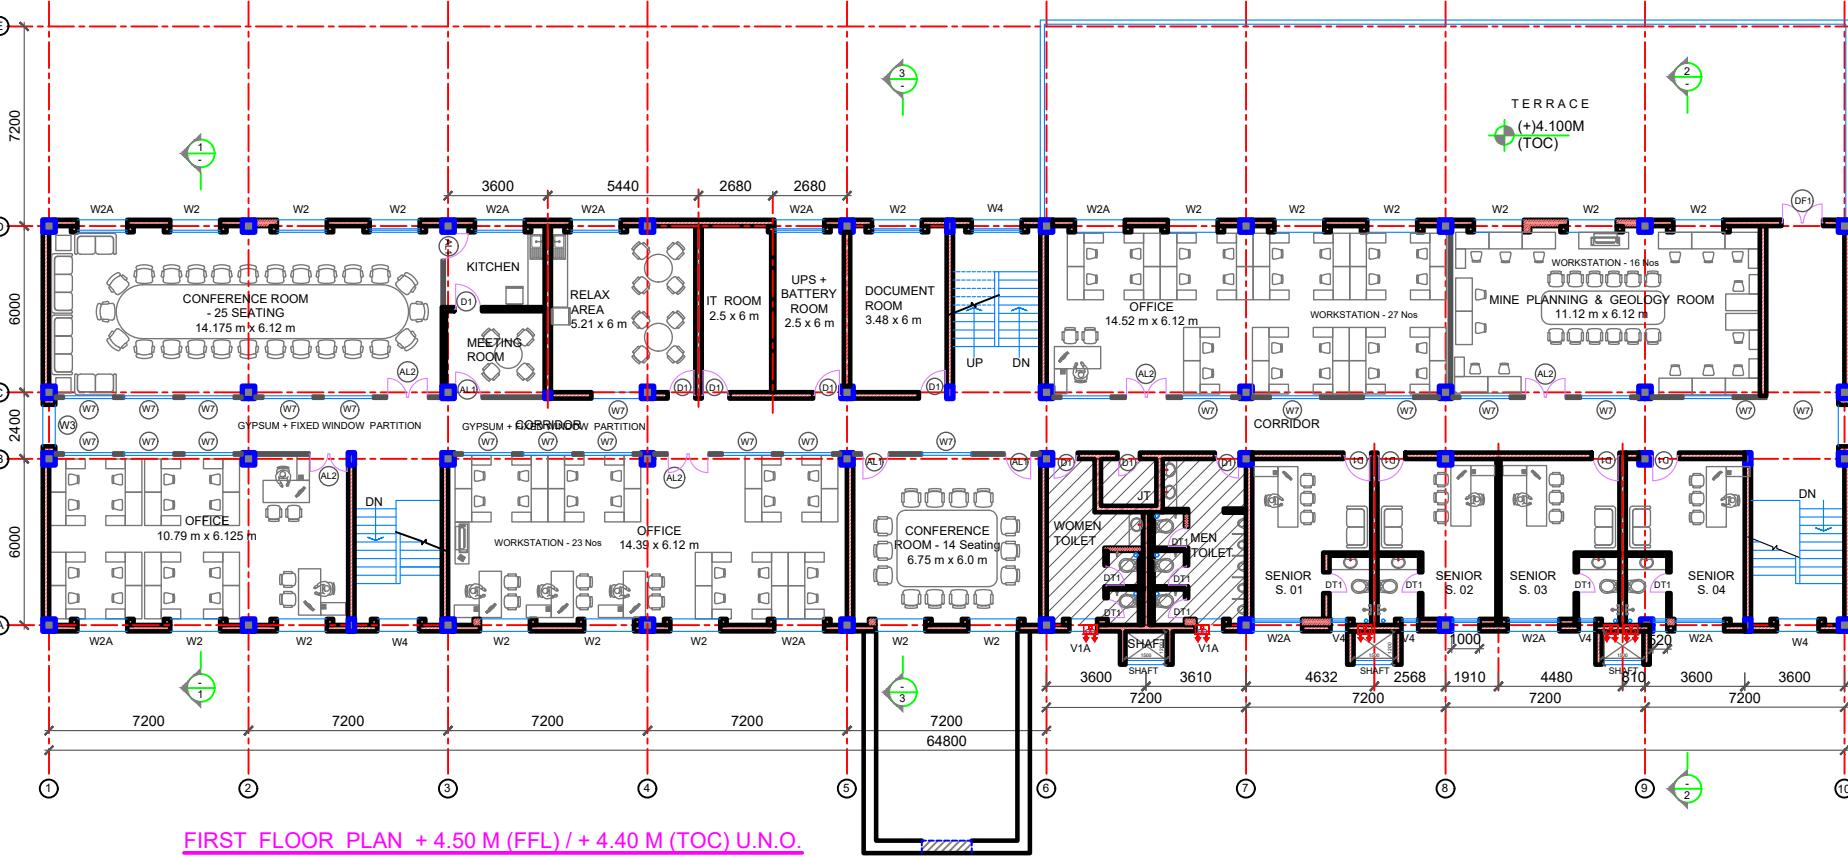


DOOR & WINDOW SCHEDULE

No	SILL	WIDTH	HEIGHT	DESCRIPTION
W1	1000	1800	2150	Aluminium Fixed Window
V1	1650	1000	1500	Aluminium Fixed Window - Louvers
V1A	1300	1000	1500	Aluminium Fixed Window - Louvers
W2	1000	1800	1800	Aluminium Fixed Window
V2	2400	1000	750	Aluminium Fixed Window
W3	1000	1500	1800	Aluminium Fixed + Openable Window
V4	1800	600	1000	Aluminium Fixed Window
W4	950	1800	1500	Aluminium Fixed Window
W5	2400	1800	750	Aluminium Fixed Window - Louvers
W6	600	1500	1500	Aluminium Fixed Window
W7	1000	1800	1500	Aluminium Fixed Window
W8	1000	1000	2150	Aluminium Fixed Window

DOOR & WINDOW SCHEDULE



No	SILL	WIDTH	HEIGHT	DESCRIPTION
D1	1000	2400	2400	General Purpose Steel Door
D2	1500	2400	2400	General Purpose Steel Door
D3	1200	2400	2400	General Purpose Steel Door
DF1	1500	2400	2400	Fire Rated HMP5 Door
DT1	750	2100	2100	General Purpose Metal Door
AL1	1000	2400	2400	Aluminium Half Glazed Door
AL2	1500	2400	2400	Aluminium Half Glazed Door
GD	1800	2400	2400	Glass Door

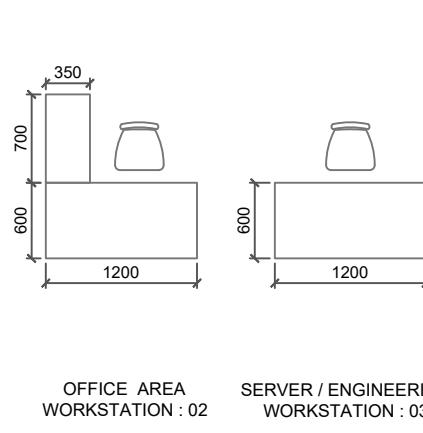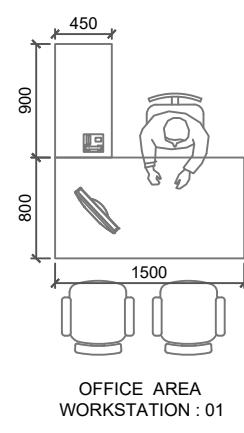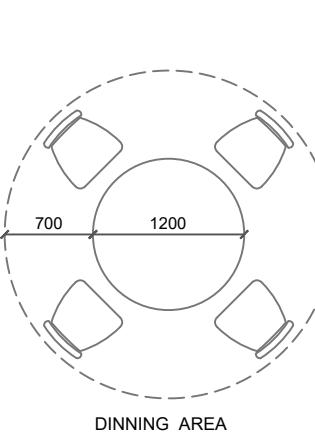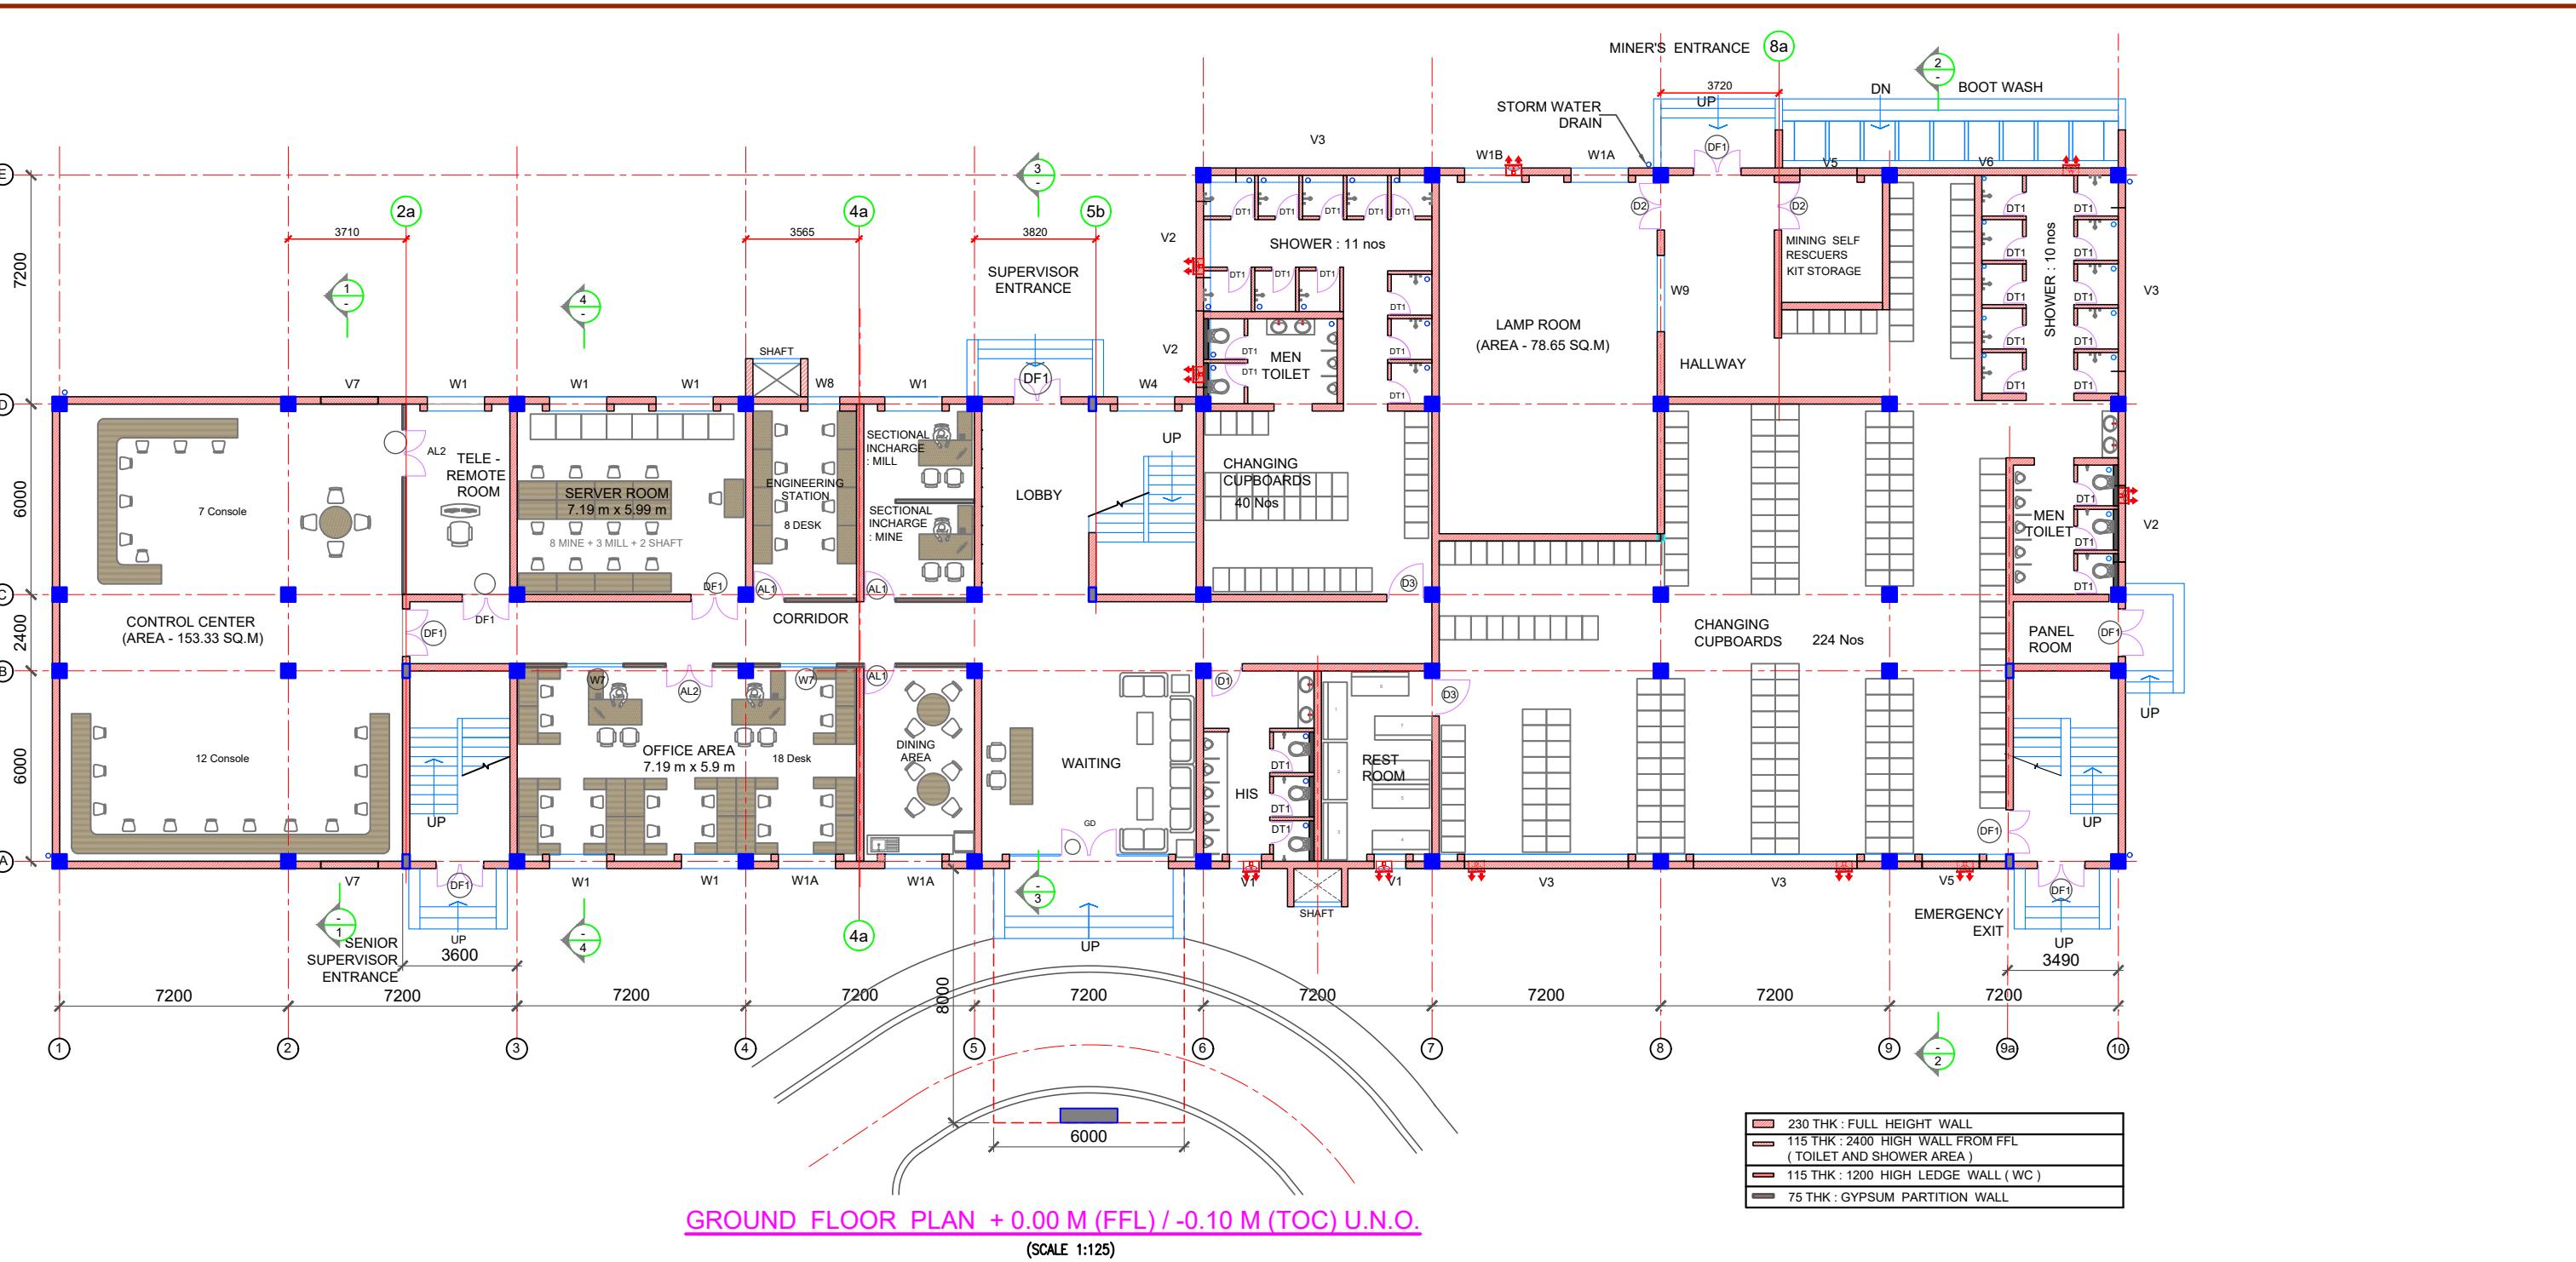

WINDOW SCHEDULE				
No	SILL	WIDTH	HEIGHT	DESCRIPTION
W1	1000	1800	2150	Aluminium Fixed Window
W1A	1000	1800	2150	Aluminium Sliding Window
W1B	1000	1800	2150	Aluminium Fixed / Exhaust
W2	1000	1800	1800	Aluminium Fixed Window
W2A	1000	1800	1800	Aluminium Sliding Window
W3	1000	1500	1800	Aluminium Sliding Window
W4	950	1800	1500	Aluminium Fixed Window
W4A	900	1800	1500	Aluminium Sliding Window
W7	1000	1800	1500	Aluminium Fixed Window
W8	1000	1000	2150	Aluminium Fixed Window
W9	1000	2400	2350	Aluminium Fixed Window

VENTILATOR SCHEDULE				
No	SILL	WIDTH	HEIGHT	DESCRIPTION
V1	1650	1000	1500	Aluminium Fixed Window - Louvers
V1A	1300	1000	1500	Aluminium Fixed Window - Louvers
V2	2400	2400	750	Aluminium Fixed Window
V3	2400	5150	750	Aluminium Fixed Window - Louvers
V4	1800	600	1000	Aluminium Fixed Window
V5	2400	1800	750	Aluminium Fixed Window - Louvers
V6	2400	6750	750	Aluminium Fixed Window - Louvers
V7	2400	1800	750	Aluminium Fixed Window


DOOR SCHEDULE			
No	WIDTH	HEIGHT	DESCRIPTION
D1	1000	2400	General Purpose Steel Door
D2	1500	2400	General Purpose Steel Door
D3	1200	2400	General Purpose Steel Door
DF1	1500	2400	Fire Rated HMPs Door
DT1	750	2100	General Purpose Metal Door
AL1	1000	2400	Aluminium Half Glazed Door
AL2	1500	2400	Aluminium Half Glazed Door
GD	1800	2400	Glass Door

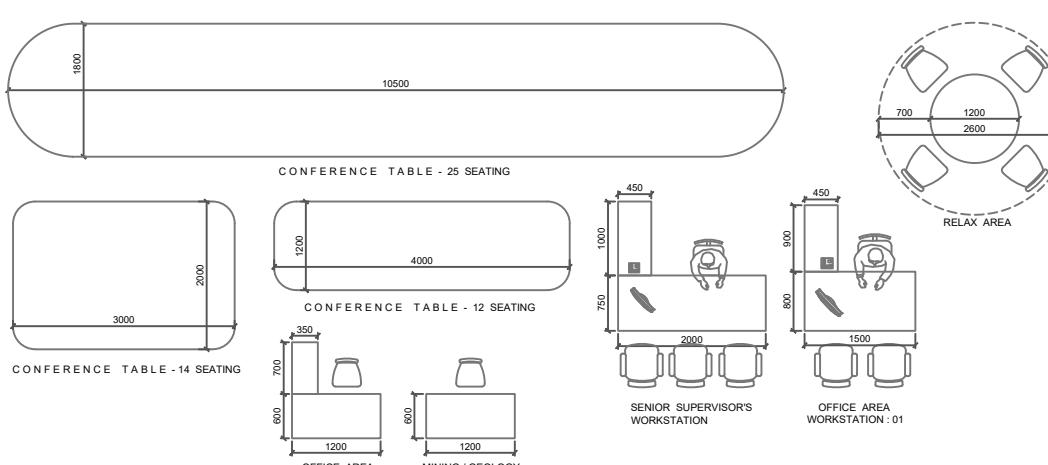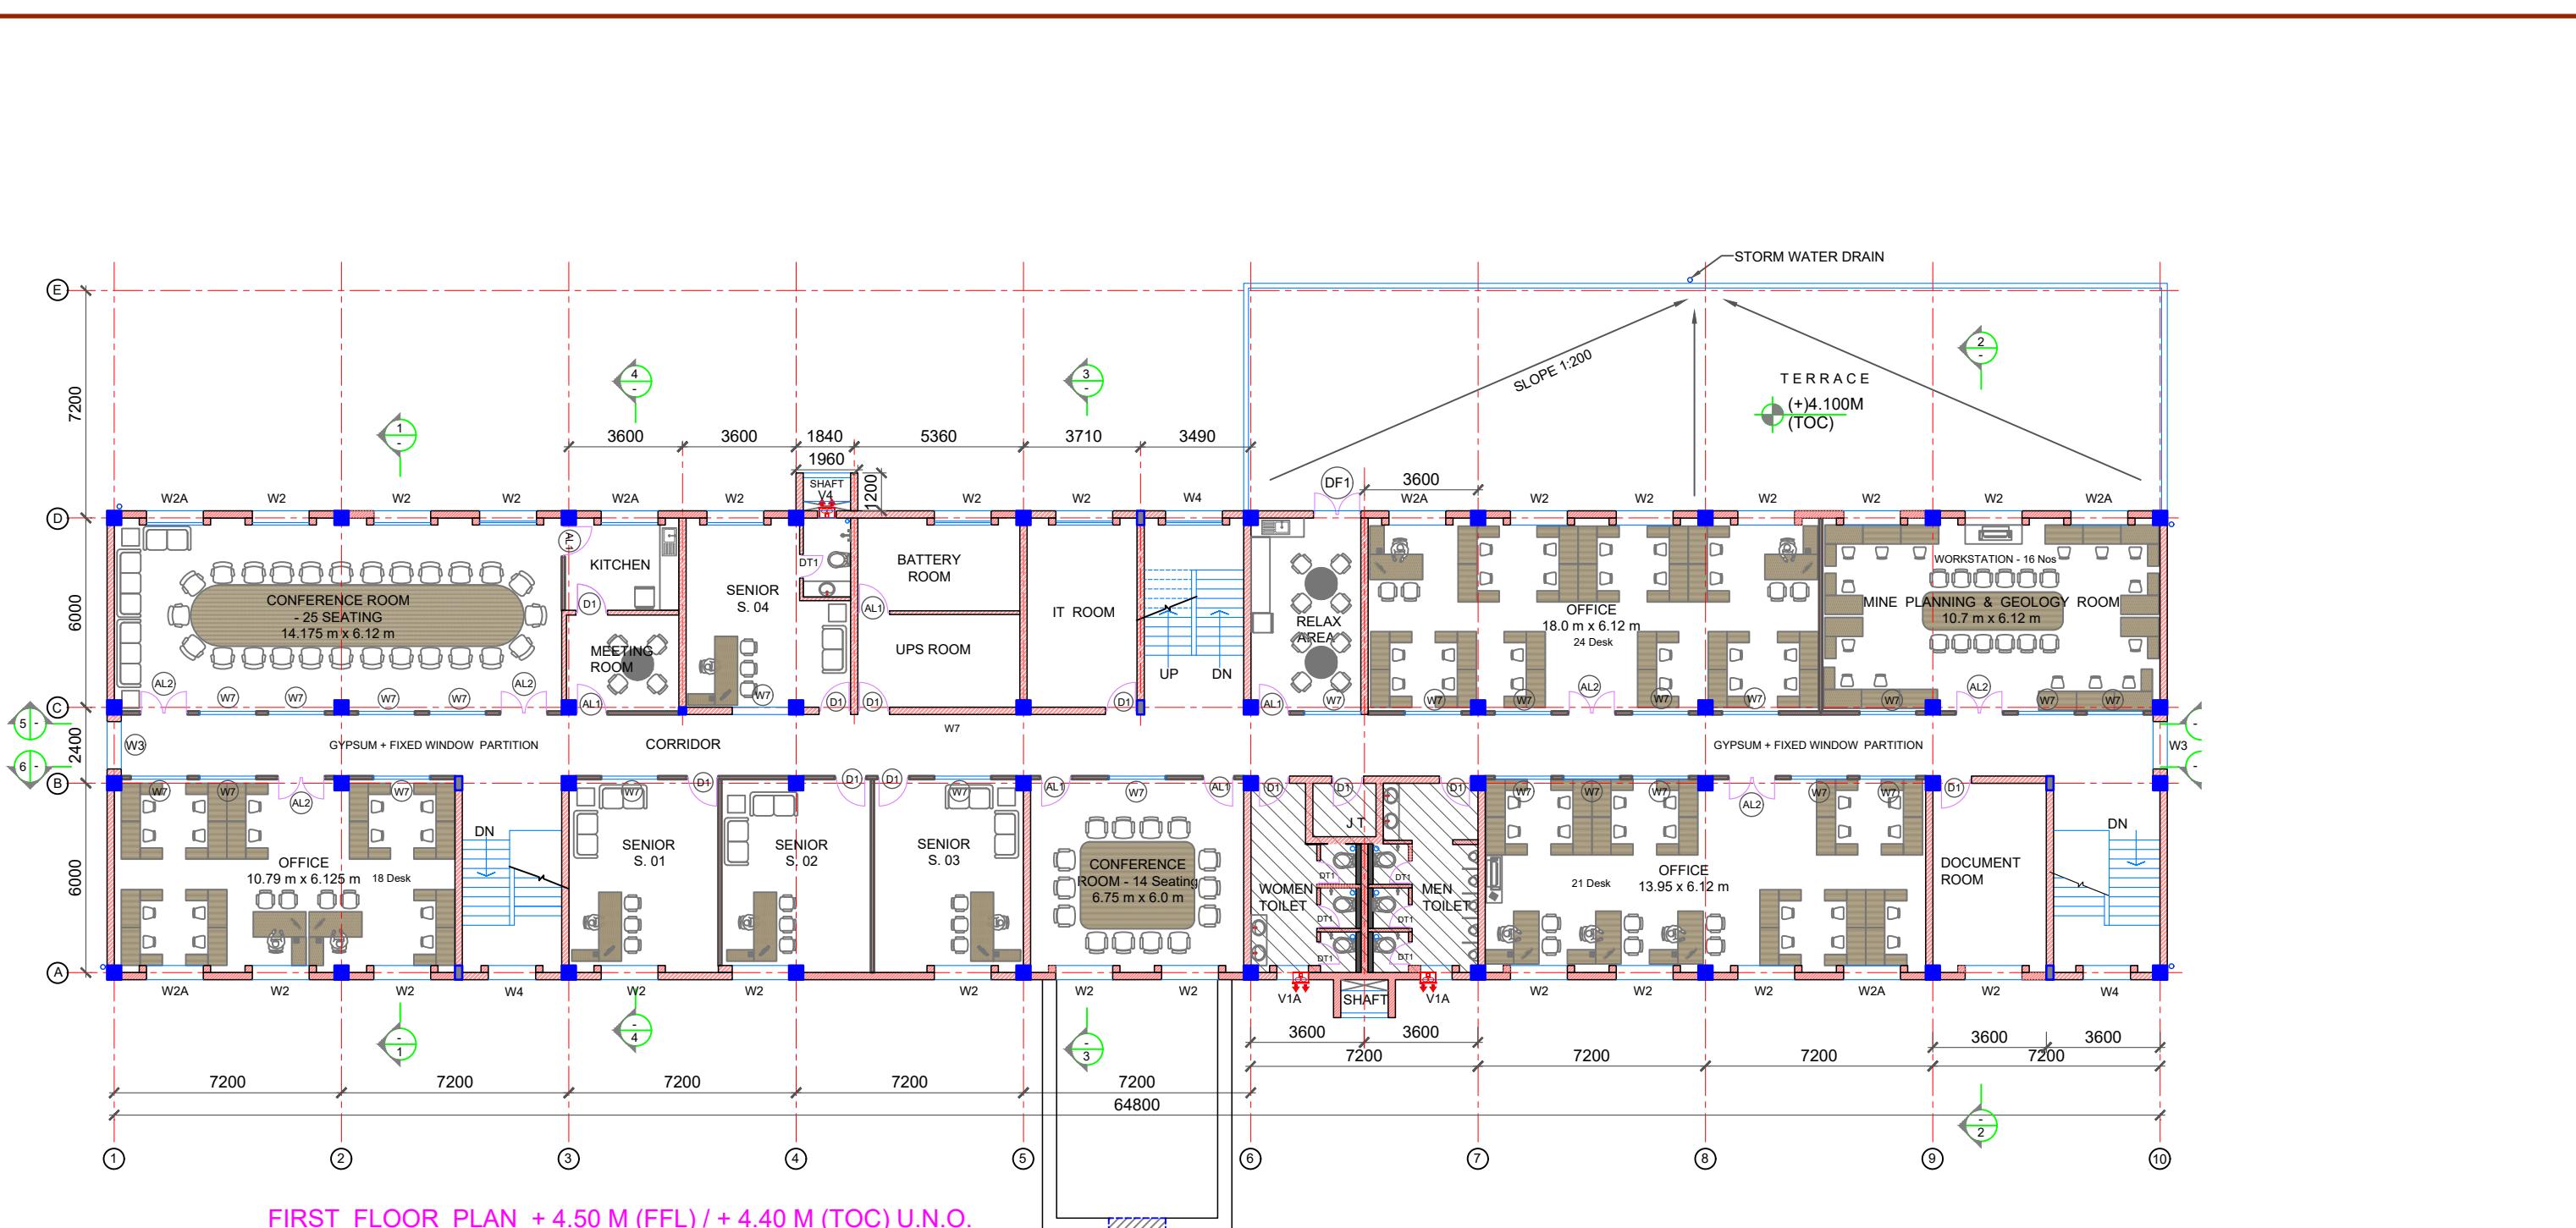

WINDOW SCHEDULE			
No	SILL	WIDTH	HEIGHT
W1	1000	1800	2150
W1A	1000	1800	2150
W1B	1000	1800	2150
W2	1000	1800	1800
W2A	1000	1800	1800
W3	1000	1500	1800
W4	950	1800	1500
W4A	900	1800	1500
W7	1000	1800	1500
W8	1000	1000	2150
W9	1000	2400	2350

VENTILATOR SCHEDULE			
No	SILL	WIDTH	HEIGHT
V1	1650	1000	1500
V1A	1300	1000	1500
V2	2400	2400	750
V3	2400	5150	750
V4	1800	600	1000
V5	2400	1800	750
V6	2400	6750	750
V7	2400	1800	750

DOOR SCHEDULE		
No	WIDTH	HEIGHT
D1	1000	2400
D2	1500	2400
D3	1200	2400
DF1	1500	2400
DT1	750	2100
AL1	1000	2400
AL2	1500	2400
GD	1800	2400

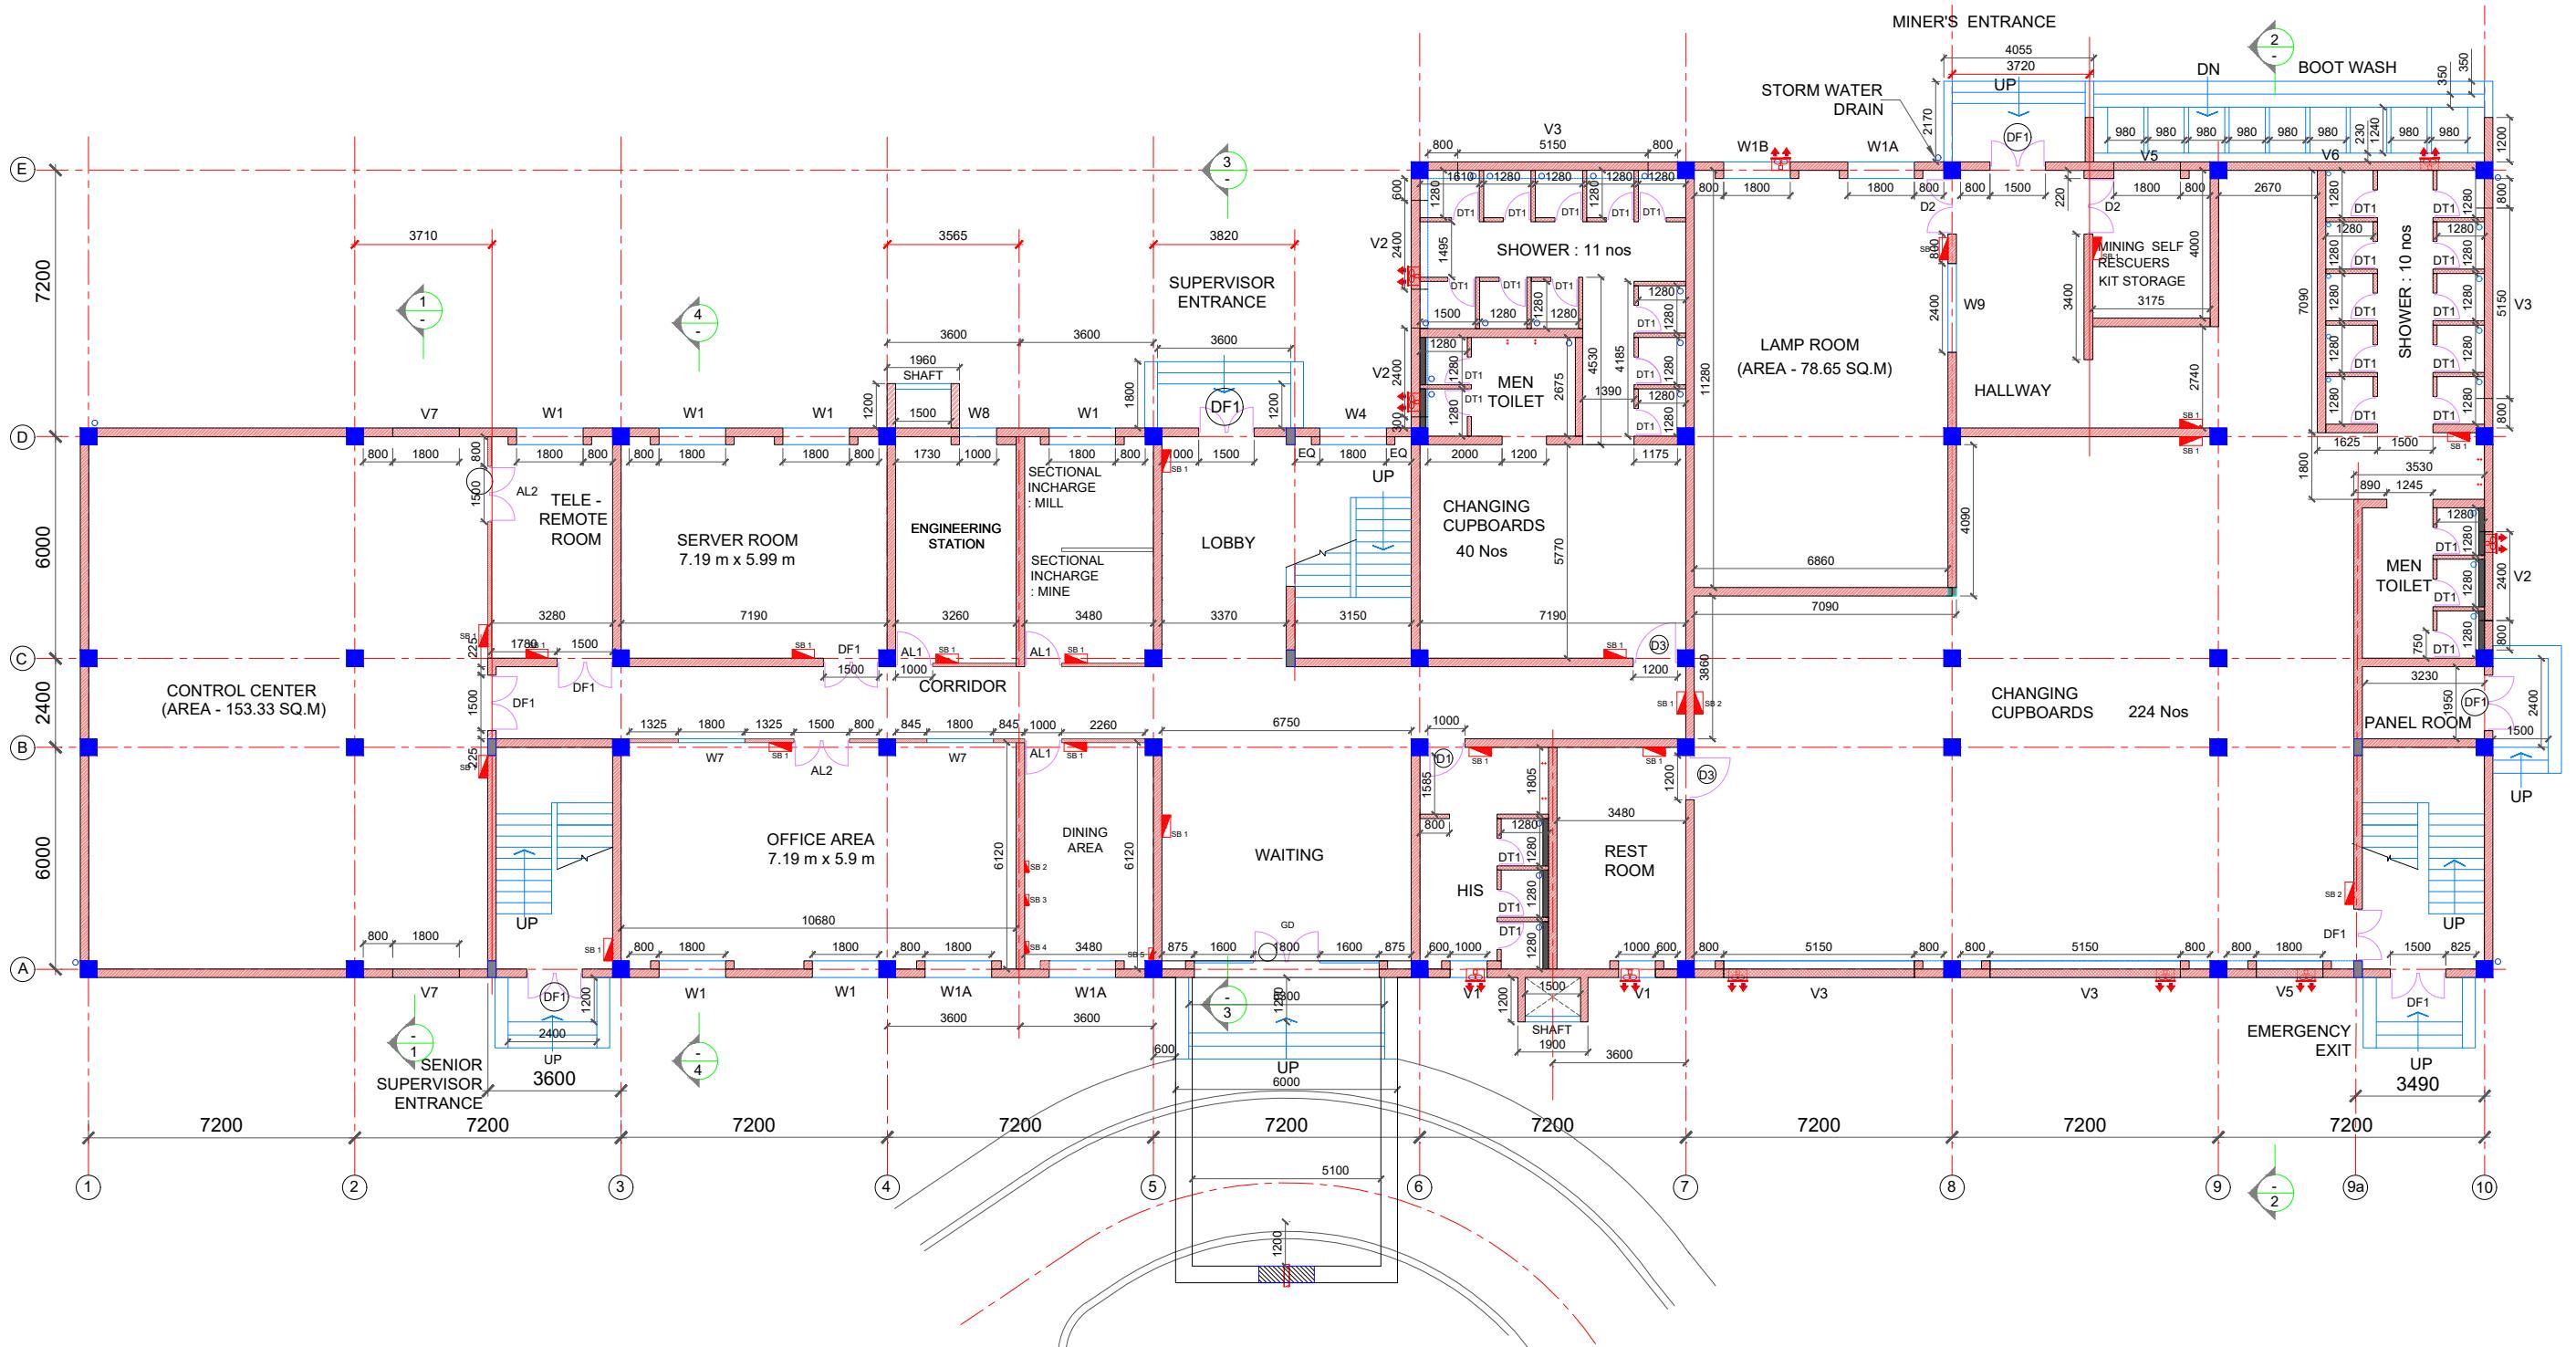


GROUND FLOOR PLAN + 0.00 M (FFL) / -0.10 M (TOC) U.N.O.

(SCALE 1:125)

WINDOW SCHEDULE				
No	SILL	WIDTH	HEIGHT	DESCRIPTION
W1	1000	1800	2150	Aluminium Fixed Window
W1A	1000	1800	2150	Aluminium Sliding Window
W1B	1000	1800	2150	Aluminium Fixed / Exhaust
W2	1000	1800	1800	Aluminium Fixed Window
W2A	1000	1800	1800	Aluminium Sliding Window
W3	1000	1500	1800	Aluminium Sliding Window
W4	950	1800	1500	Aluminium Fixed Window
W4A	900	1800	1500	Aluminium Sliding Window
W7	1000	1800	1500	Aluminium Fixed Window
W8	1000	1000	2150	Aluminium Fixed Window
W9	1000	2400	2350	Aluminium Fixed Window

VENTILATOR SCHEDULE				
No	SILL	WIDTH	HEIGHT	DESCRIPTION
V1	1650	1000	1500	Aluminium Fixed Window - Louvers
V1A	1300	1000	1500	Aluminium Fixed Window - Louvers
V2	2400	2400	750	Aluminium Fixed Window
V3	2400	5150	750	Aluminium Fixed Window - Louvers
V4	1800	600	1000	Aluminium Fixed Window
V5	2400	1800	750	Aluminium Fixed Window - Louvers
V6	2400	6750	750	Aluminium Fixed Window - Louvers
V7	2400	1800	750	Aluminium Fixed Window

DOOR SCHEDULE			
SL No	WIDTH	HEIGHT	DESCRIPTION
D1	1000	2400	General Purpose Steel Door
D2	1500	2400	General Purpose Steel Door
D3	1200	2400	General Purpose Steel Door
F1	1500	2400	Fire Rated HMPS Door
T1	750	2100	General Purpose Metal Door
L1	1000	2400	Aluminium Half Glazed Door
L2	1500	2400	Aluminium Half Glazed Door
G	1800	2400	Glass Door

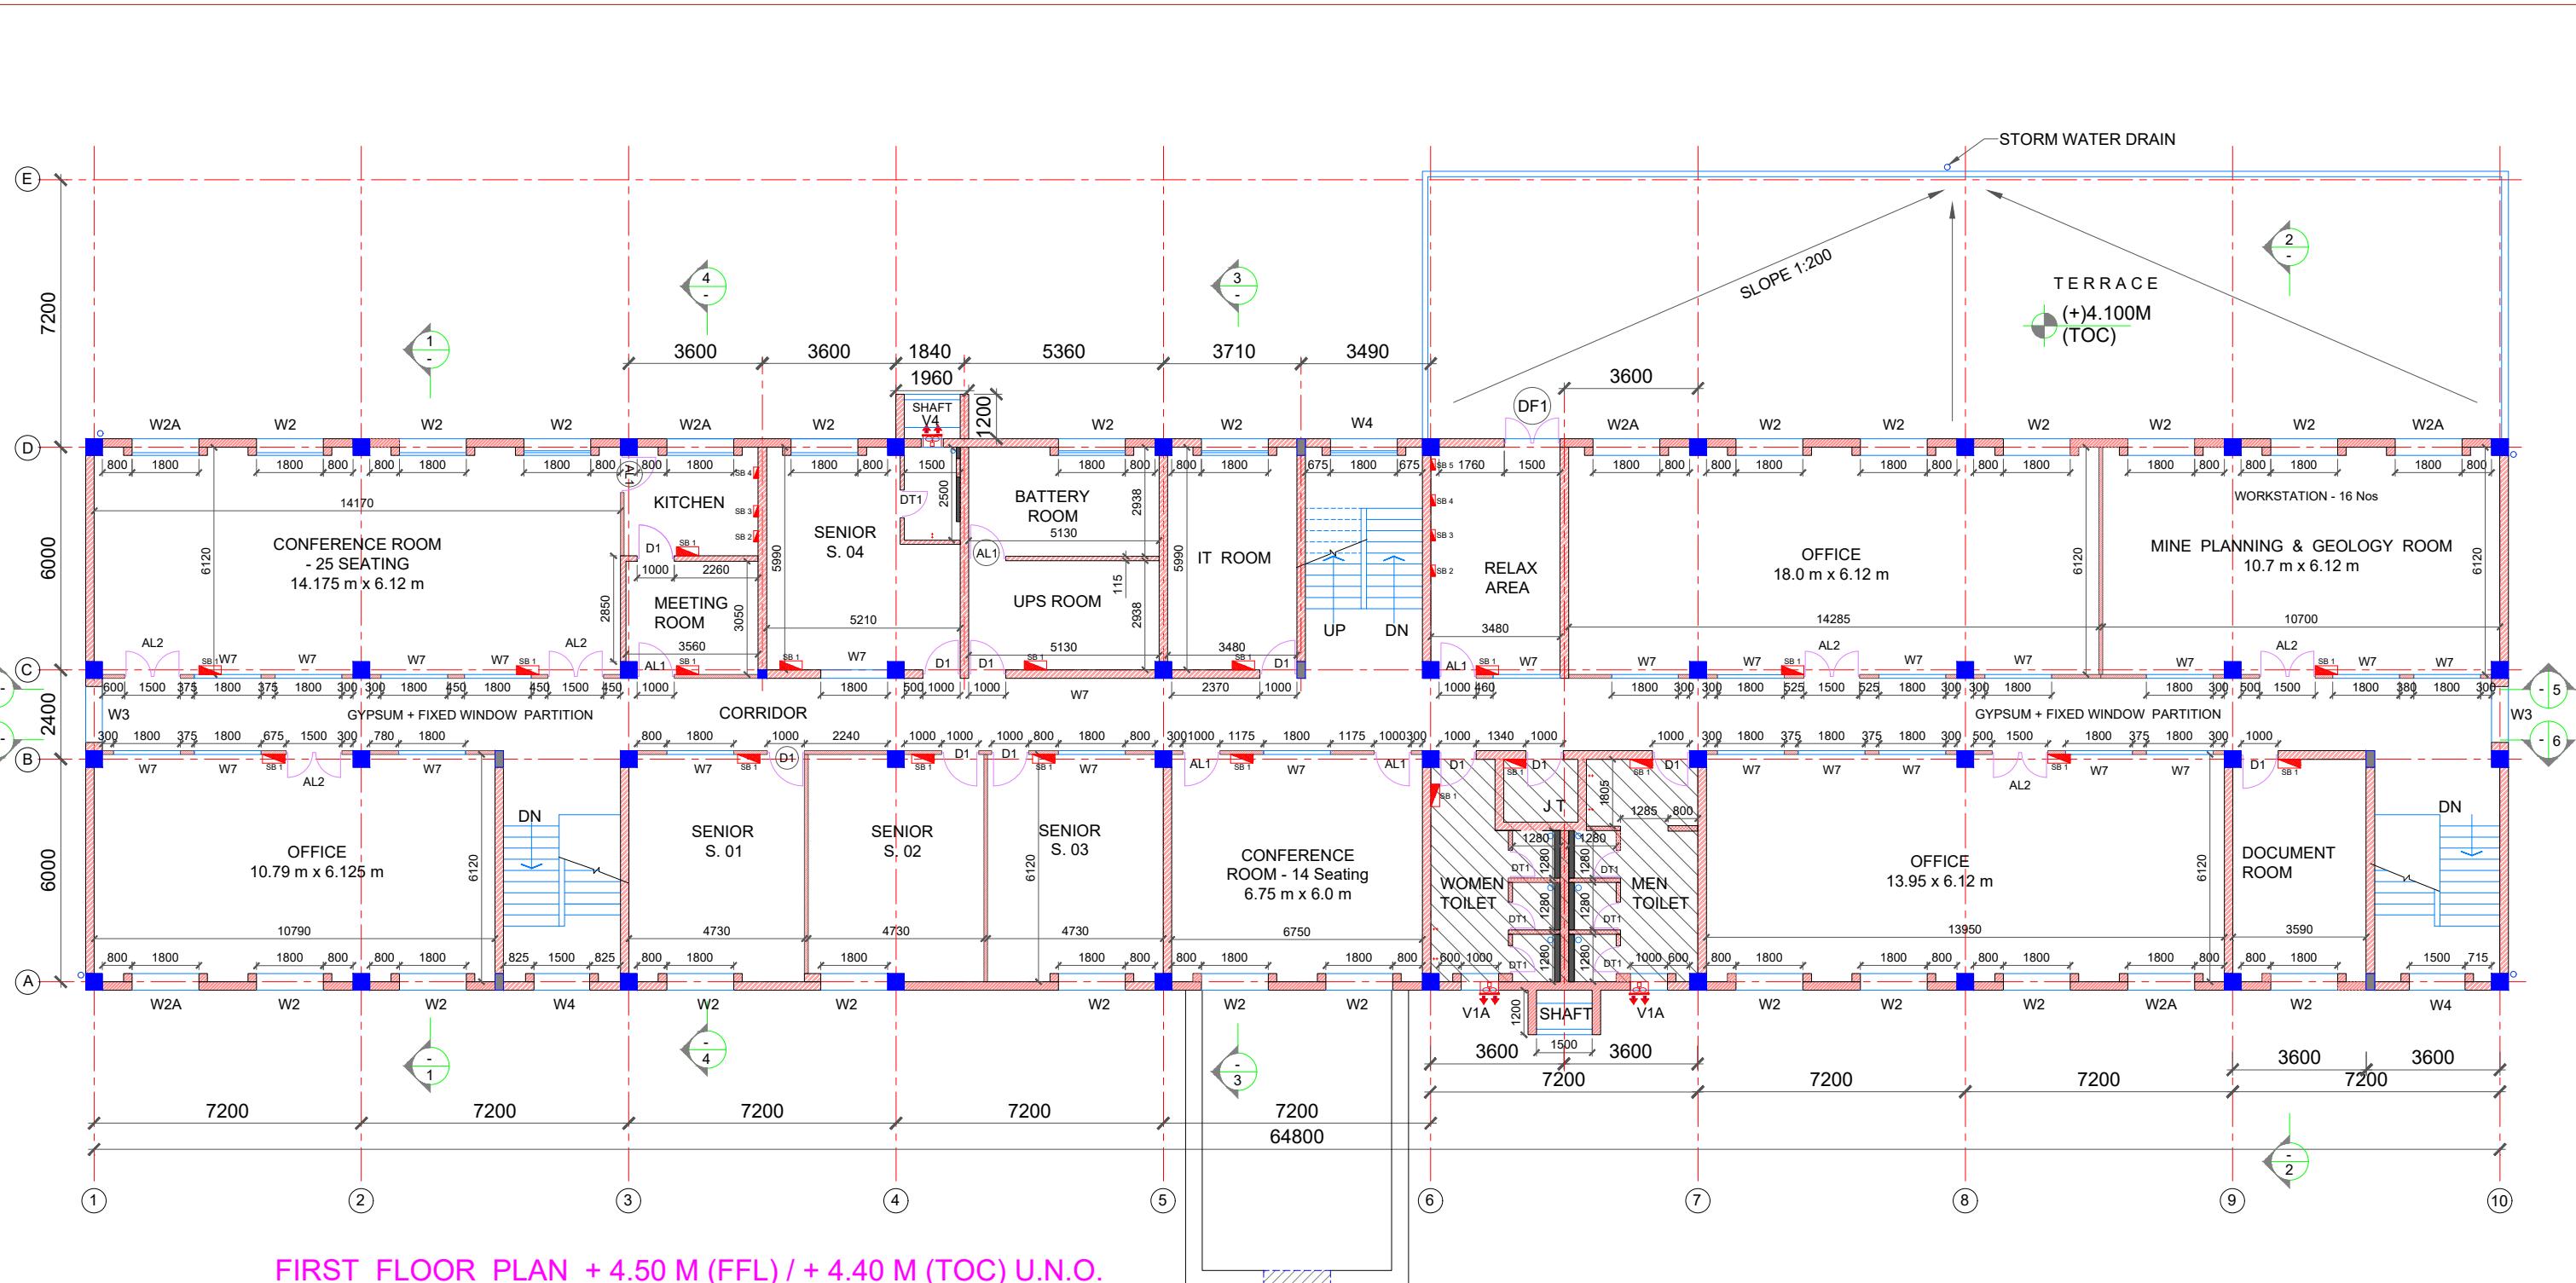


FIRST FLOOR PLAN + 4.50 M (FFL) / + 4.40 M (TOC) U.N.O.

WINDOW SCHEDULE			
No	SILL	WIDTH	HEIGHT
W1	1000	1800	2150
W1A	1000	1800	2150
W1B	1000	1800	2150
W2	1000	1800	1800
W2A	1000	1800	1800
W3	1000	1500	1800
W4	950	1800	1500
W4A	900	1800	1500
W7	1000	1800	1500
W8	1000	1000	2150
W9	1000	2400	2350

VENTILATOR SCHEDULE			
No	SILL	WIDTH	HEIGHT
V1	1650	1000	1500
V1A	1300	1000	1500
V2	2400	2400	750
V3	2400	5150	750
V4	1800	600	1000
V5	2400	1800	750
V6	2400	6750	750
V7	2400	1800	750

DOOR SCHEDULE		
No	WIDTH	HEIGHT
D1	1000	2400
D2	1500	2400
D3	1200	2400
DF1	1500	2400
DT1	750	2100
AL1	1000	2400
AL2	1500	2400
GD	1800	2400

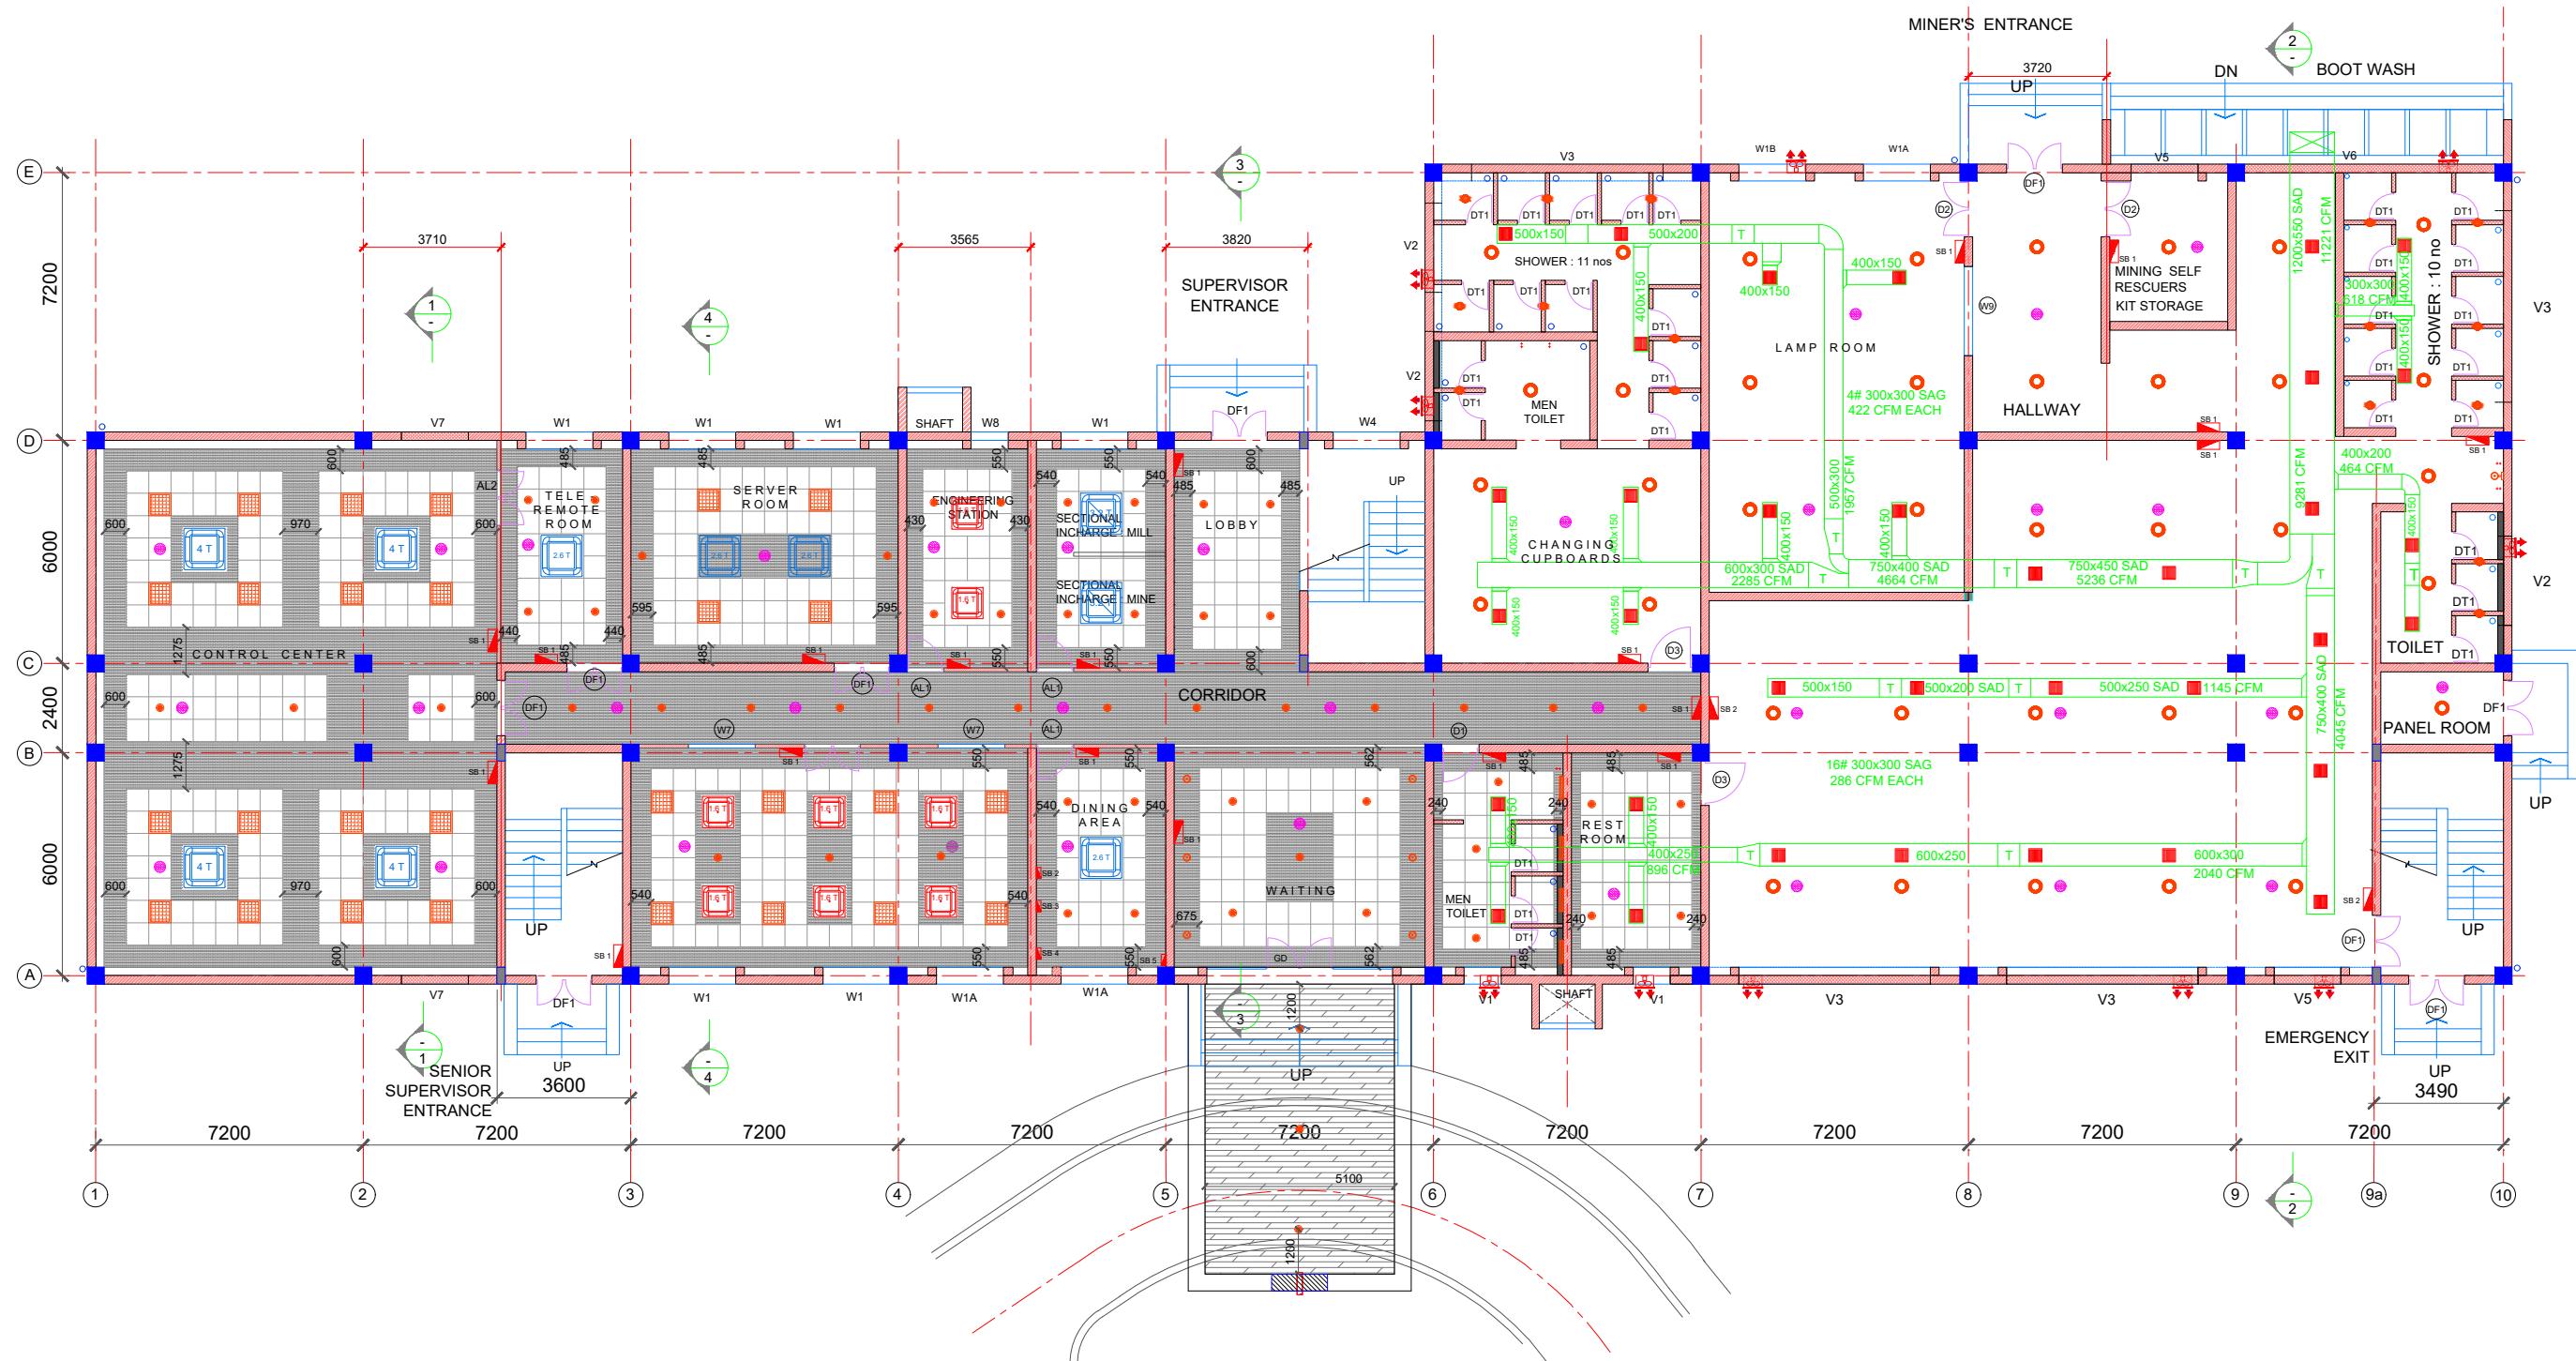



GROUND FLOOR PLAN + 0.00 M (FFL) / -0.10 M (TOC) U.N.O.

(SCALE 1:125)

	SHERA PANEL OF APPROVED COLOR + 3.450 M FROM FFL
	600 x 600 mm ARMSTRONG PANEL + 3.150 M FROM FFL
	GYPSUM PANEL + 3.200 M FROM FFL


NOTE : ALL GENERAL SWITCH BOARDS ARE AT 1500 mm FROM FFL

PRODUCT CODE	WATTAGE (W)	CATALOGUE REFERENCE	DESCRIPTION
112403	36 W	BCTBLR 36W FP WH	BAJAJ DOMINTO RECESSED MOUNTING 2' x 2' FLAT LED PANEL
112677	18 W	BPSLR 18W WH	BAJAJ RADIANCE RECESSED MOUNTING CIRCULAR LED FIXTURE
112372	6 W	BRDCSL 6W WH	BAJAJ KLOSS RECESSED MOUNTING COB LED FIXTURE
112405	5 W	BCLSB 05 WH	BAJAJ GREEN LED BATON 2100 mm FROM FFL
112810	30 W	BXTAP 30W LED WH	BAJAJ AMERIS PENDANT (SUSPENDED) LED FIXTURE 2800 mm FROM FFL
112545	18 W	BGSLO SLEEK SURFACE 18W WH RD	BAJAJ SLEEK RD ROUND SURFACE MOUNTING DOWNLIGHT

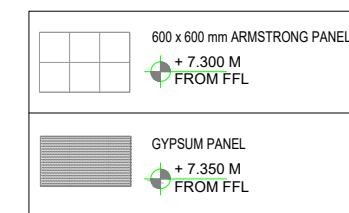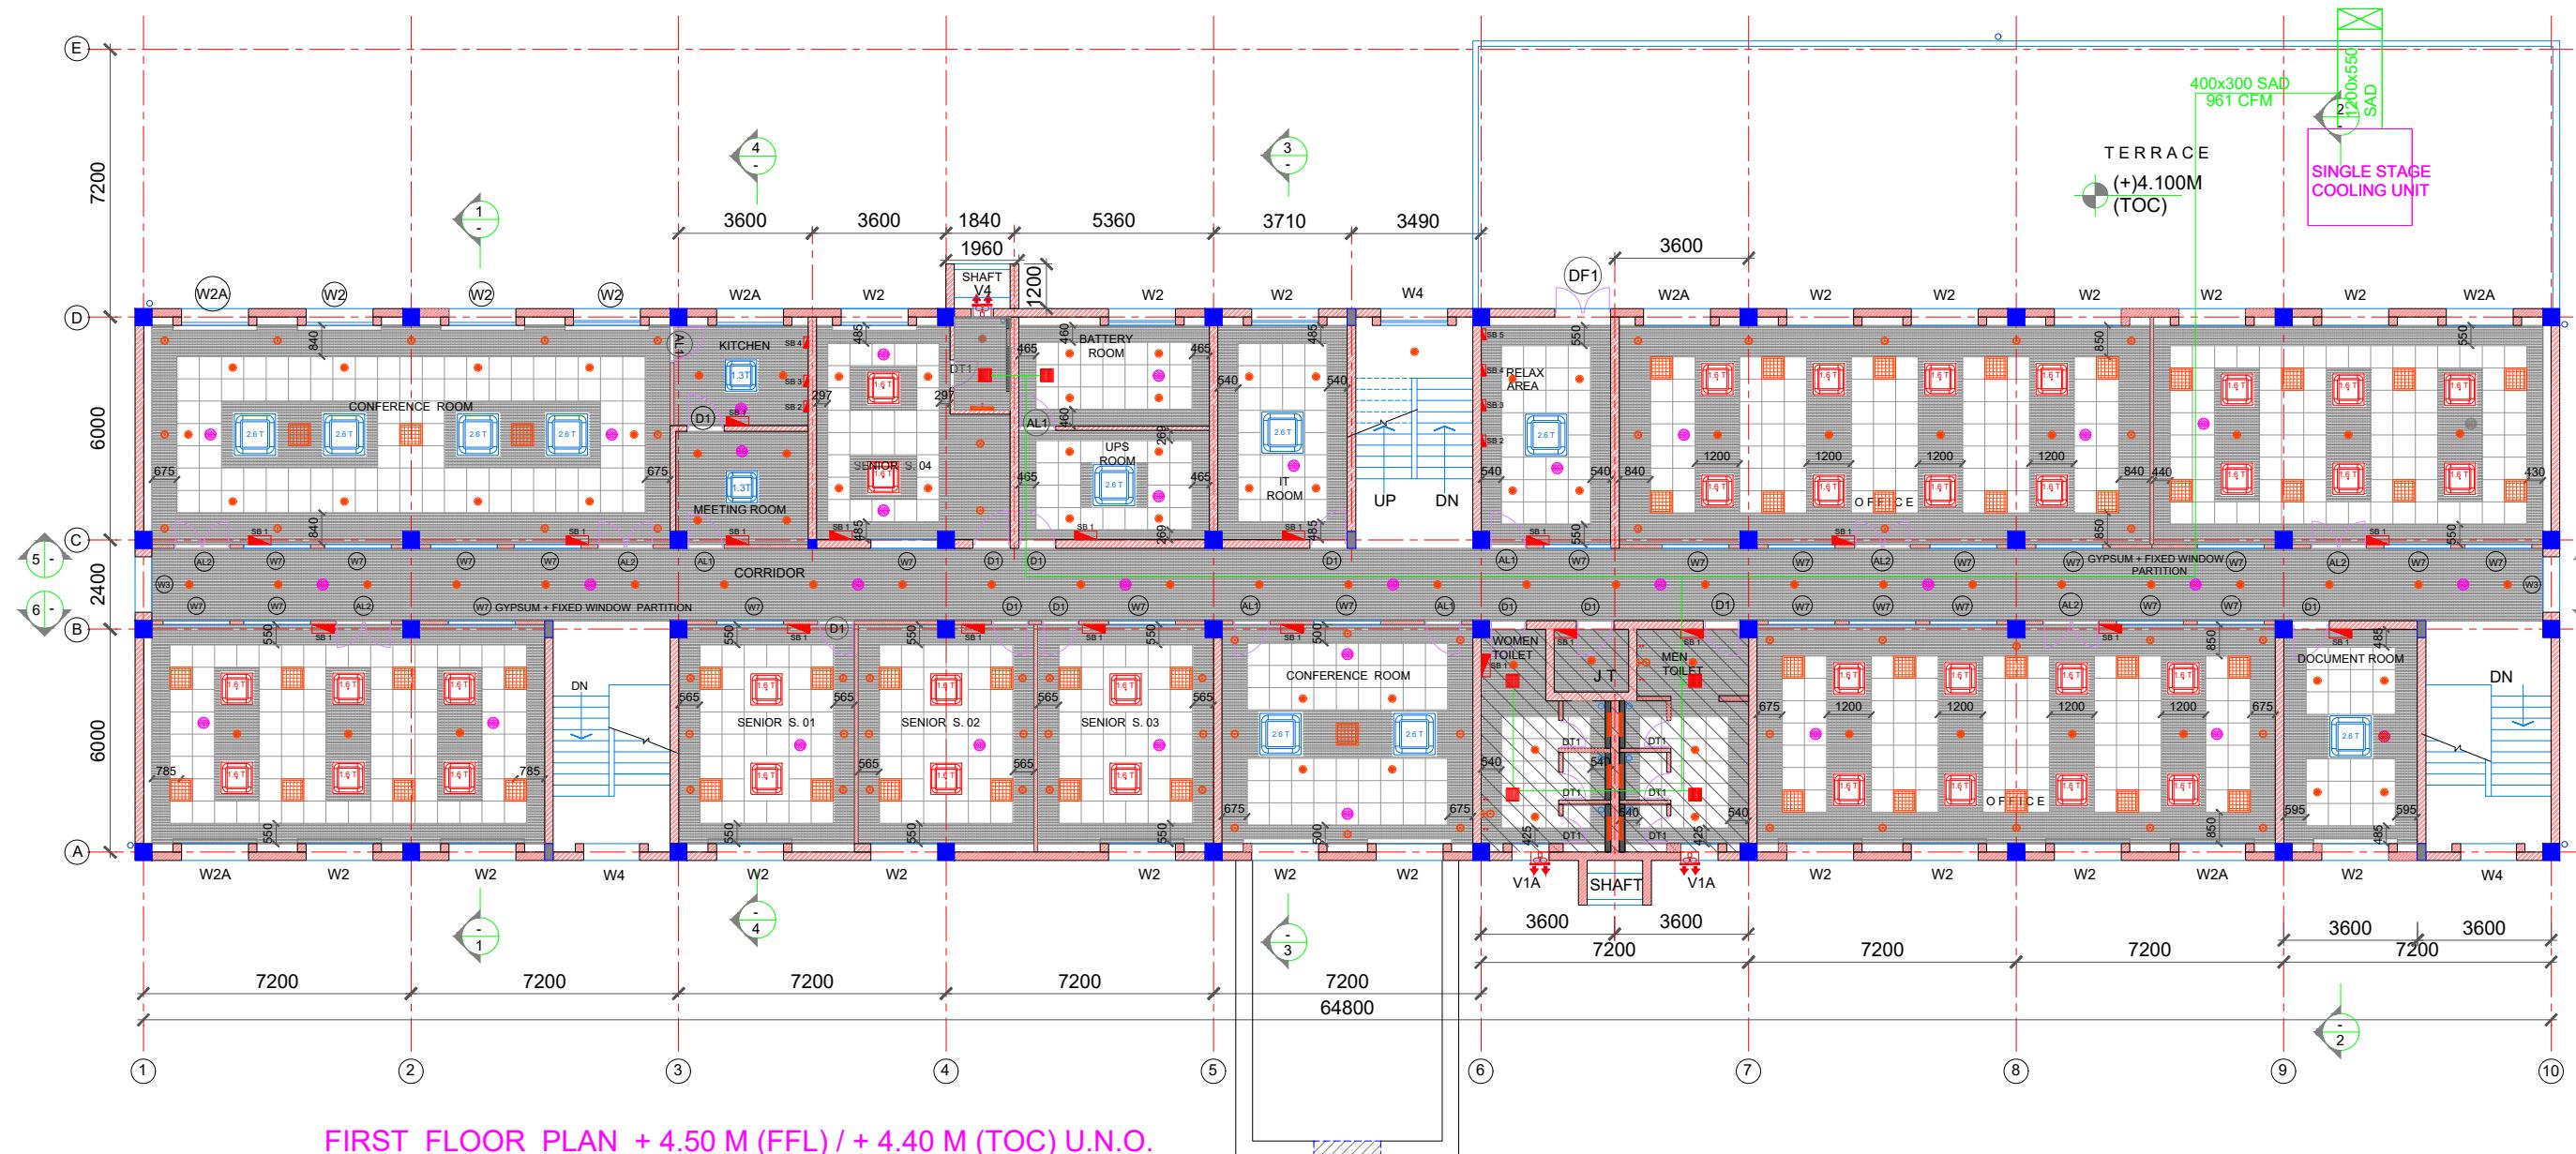



PRODUCT CODE	WATTAGE (W)	CATALOGUE REFERENCE	DESCRIPTION
112403	36 W	BCTBLR 36W FP WH	BAJAJ DOMINTO RECESSED MOUNTING 2' x 2' FLAT LED PANEL
112677	18 W	BPSLR 18W WH	BAJAJ RADIANCE RECESSED MOUNTING CIRCULAR LED FIXTURE
112372	6 W	BRDCSL 6W WH	BAJAJ KLOSS RECESSED MOUNTING COB LED FIXTURE
112405	5 W	BCLSB 05 WH	BAJAJ GREEN LED BATON 2100 mm FROM FFL

NOTE : ALL GENERAL SWITCH BOARDS ARE AT 1500 mm FROM FFL

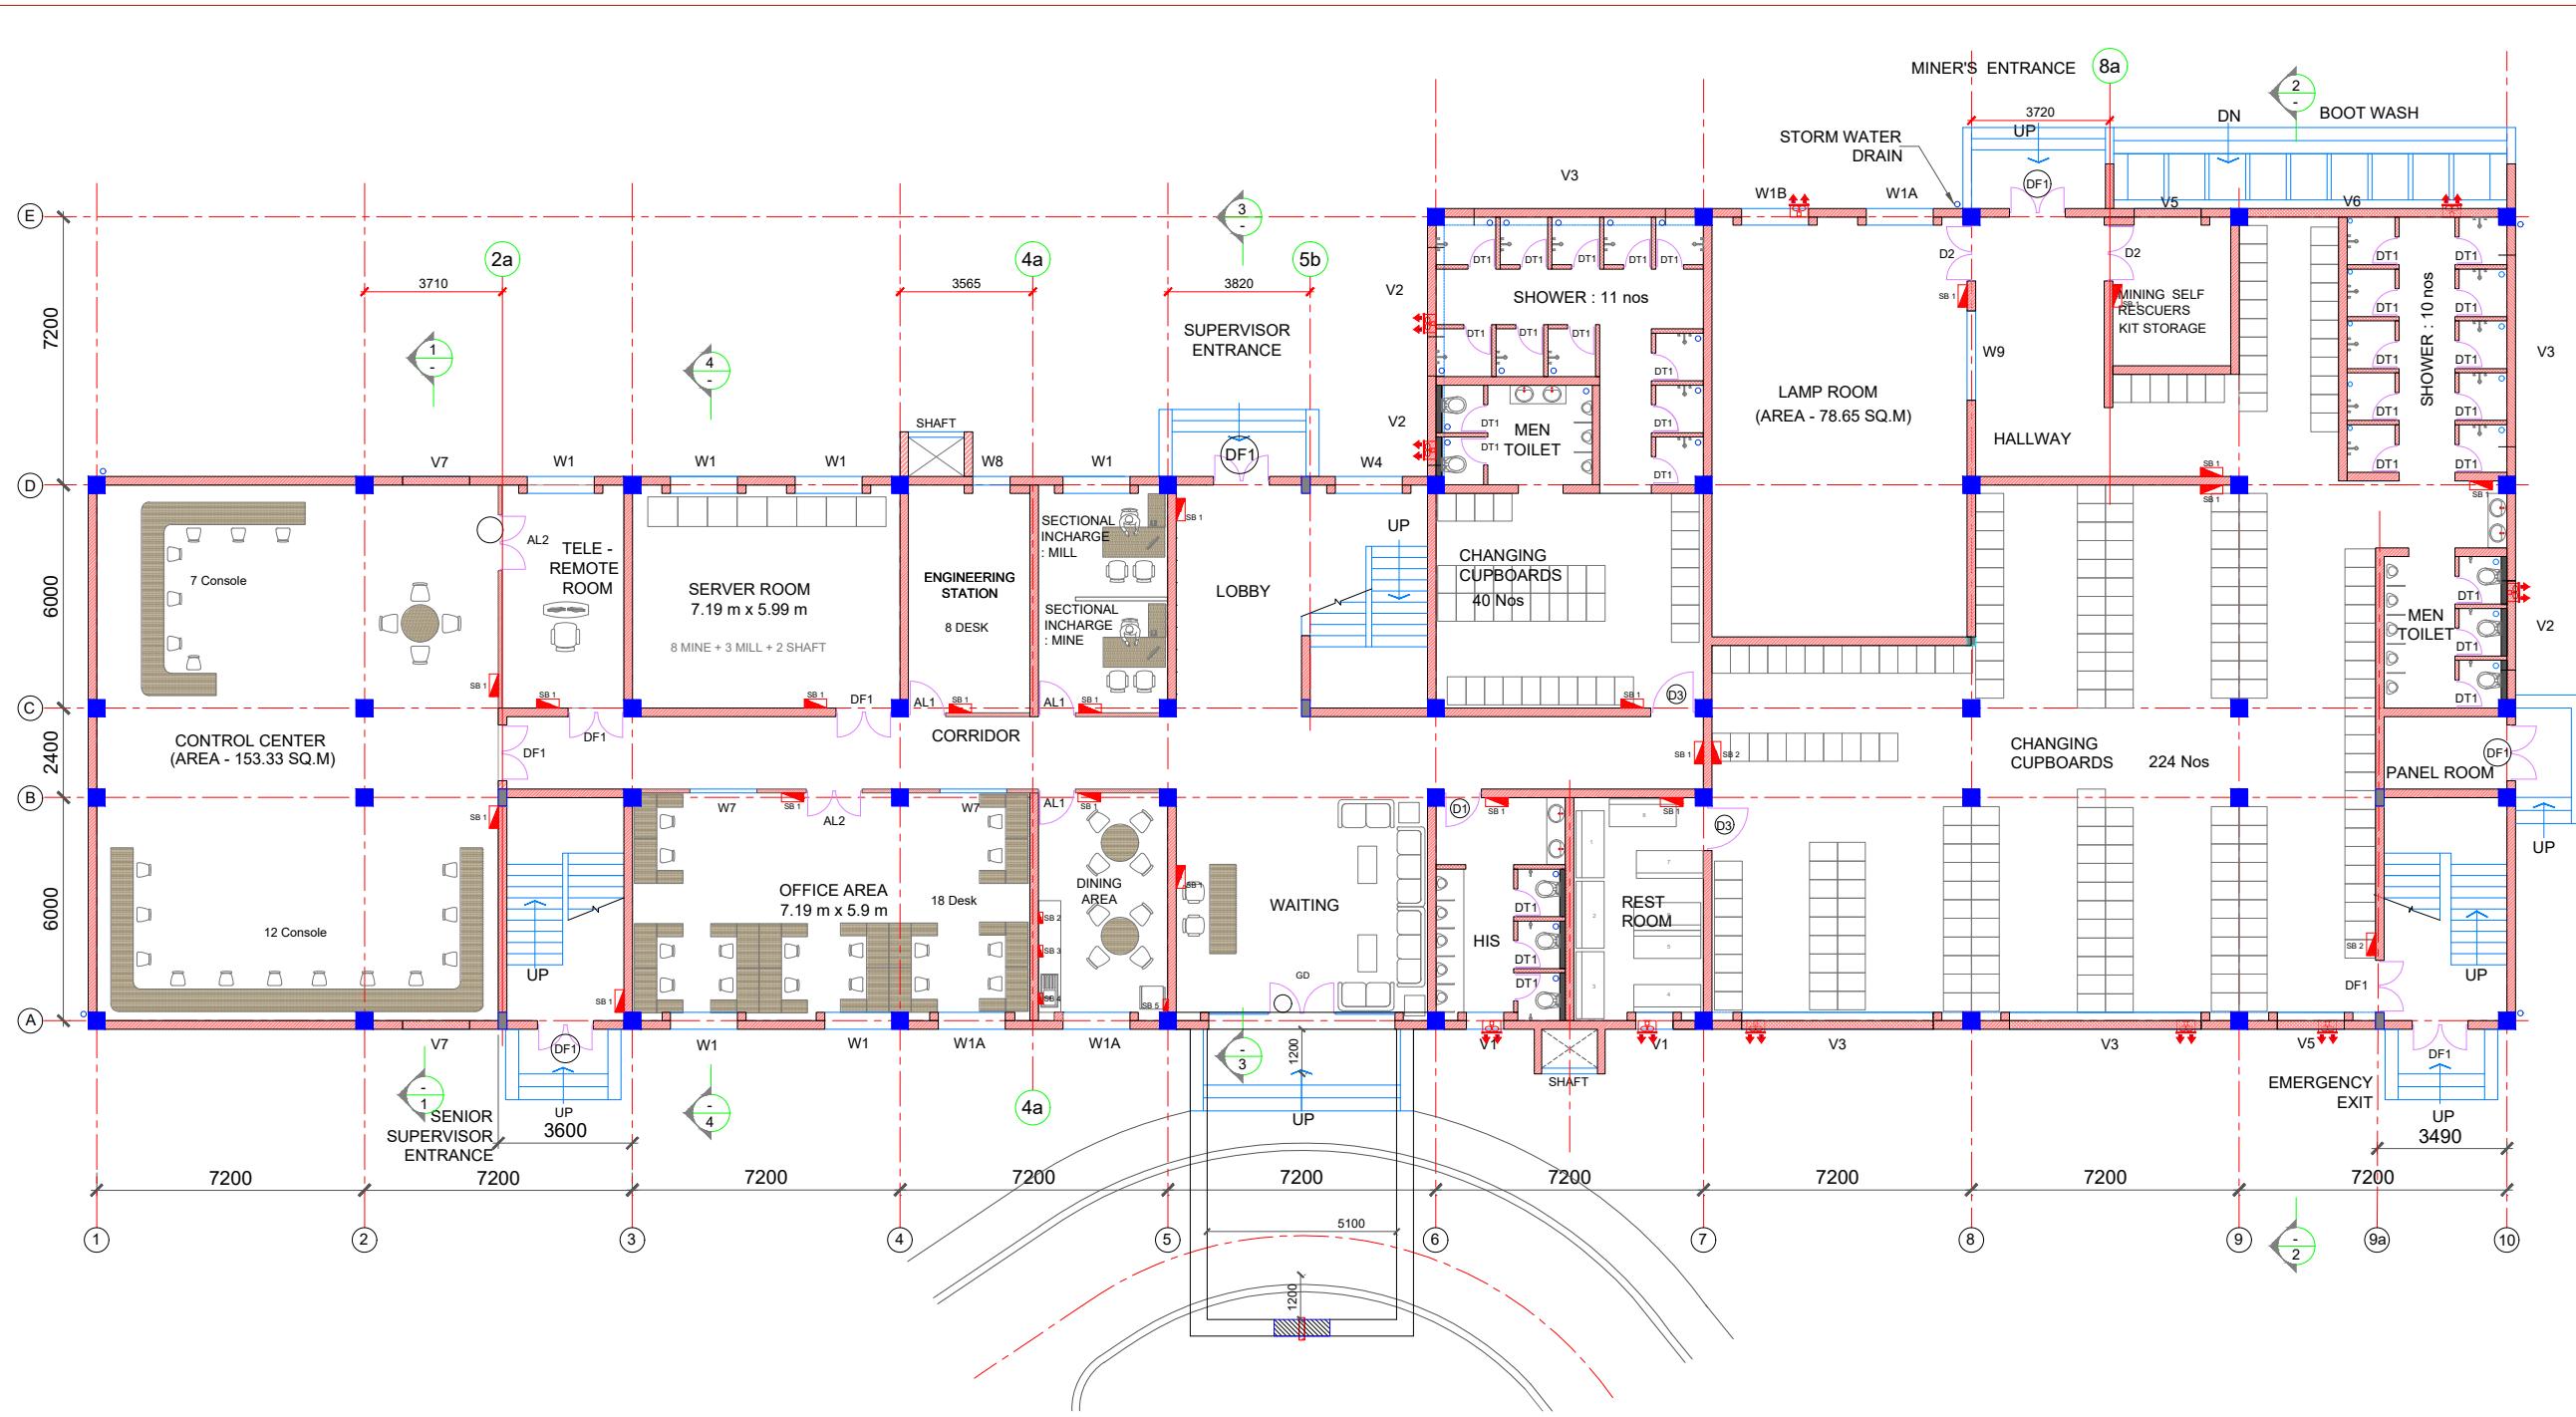


GROUND FLOOR PLAN + 0.00 M (FFL) / -0.10 M (TOC) U.N.O.

(SCALE 1:125)

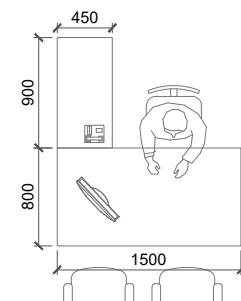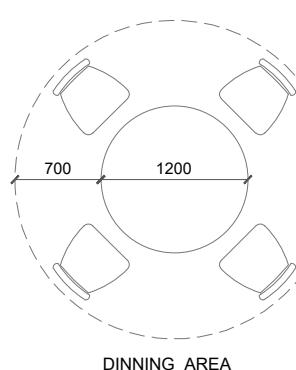

OFFICE AREA  
WORKSTATION : 01

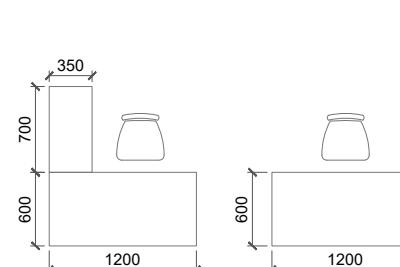


OFFICE AREA  
WORKSTATION : 02 SERVER / ENGINEERING  
WORKSTATION : 03

WINDOW SCHEDULE				
No	SILL	WIDTH	HEIGHT	DESCRIPTION
W1	1000	1800	2150	Aluminium Fixed Window
W1A	1000	1800	2150	Aluminium Sliding Window
W1B	1000	1800	2150	Aluminium Fixed / Exhaust
W2	1000	1800	1800	Aluminium Fixed Window
W2A	1000	1800	1800	Aluminium Sliding Window
W3	1000	1500	1800	Aluminium Sliding Window
W4	950	1800	1500	Aluminium Fixed Window
W4A	900	1800	1500	Aluminium Sliding Window
W7	1000	1800	1500	Aluminium Fixed Window
W8	1000	1000	2150	Aluminium Fixed Window
W9	1000	2400	2350	Aluminium Fixed Window



VENTILATOR SCHEDULE				
No	SILL	WIDTH	HEIGHT	DESCRIPTION
V1	1650	1000	1500	Aluminium Fixed Window - Louvers
V1A	1300	1000	1500	Aluminium Fixed Window - Louvers
V2	2400	2400	750	Aluminium Fixed Window
V3	2400	5150	750	Aluminium Fixed Window - Louvers
V4	1800	600	1000	Aluminium Fixed Window
V5	2400	1800	750	Aluminium Fixed Window - Louvers
V6	2400	6750	750	Aluminium Fixed Window - Louvers
V7	2400	1800	750	Aluminium Fixed Window

DOOR SCHEDULE			
No	WIDTH	HEIGHT	DESCRIPTION
D1	1000	2400	General Purpose Steel Door
D2	1500	2400	General Purpose Steel Door
D3	1200	2400	General Purpose Steel Door
DF1	1500	2400	Fire Rated HMPS Door
DT1	750	2100	General Purpose Metal Door
AL1	1000	2400	Aluminum Half Glazed Door
AL2	1500	2400	Aluminum Half Glazed Door
GD	1800	2400	Glass Door

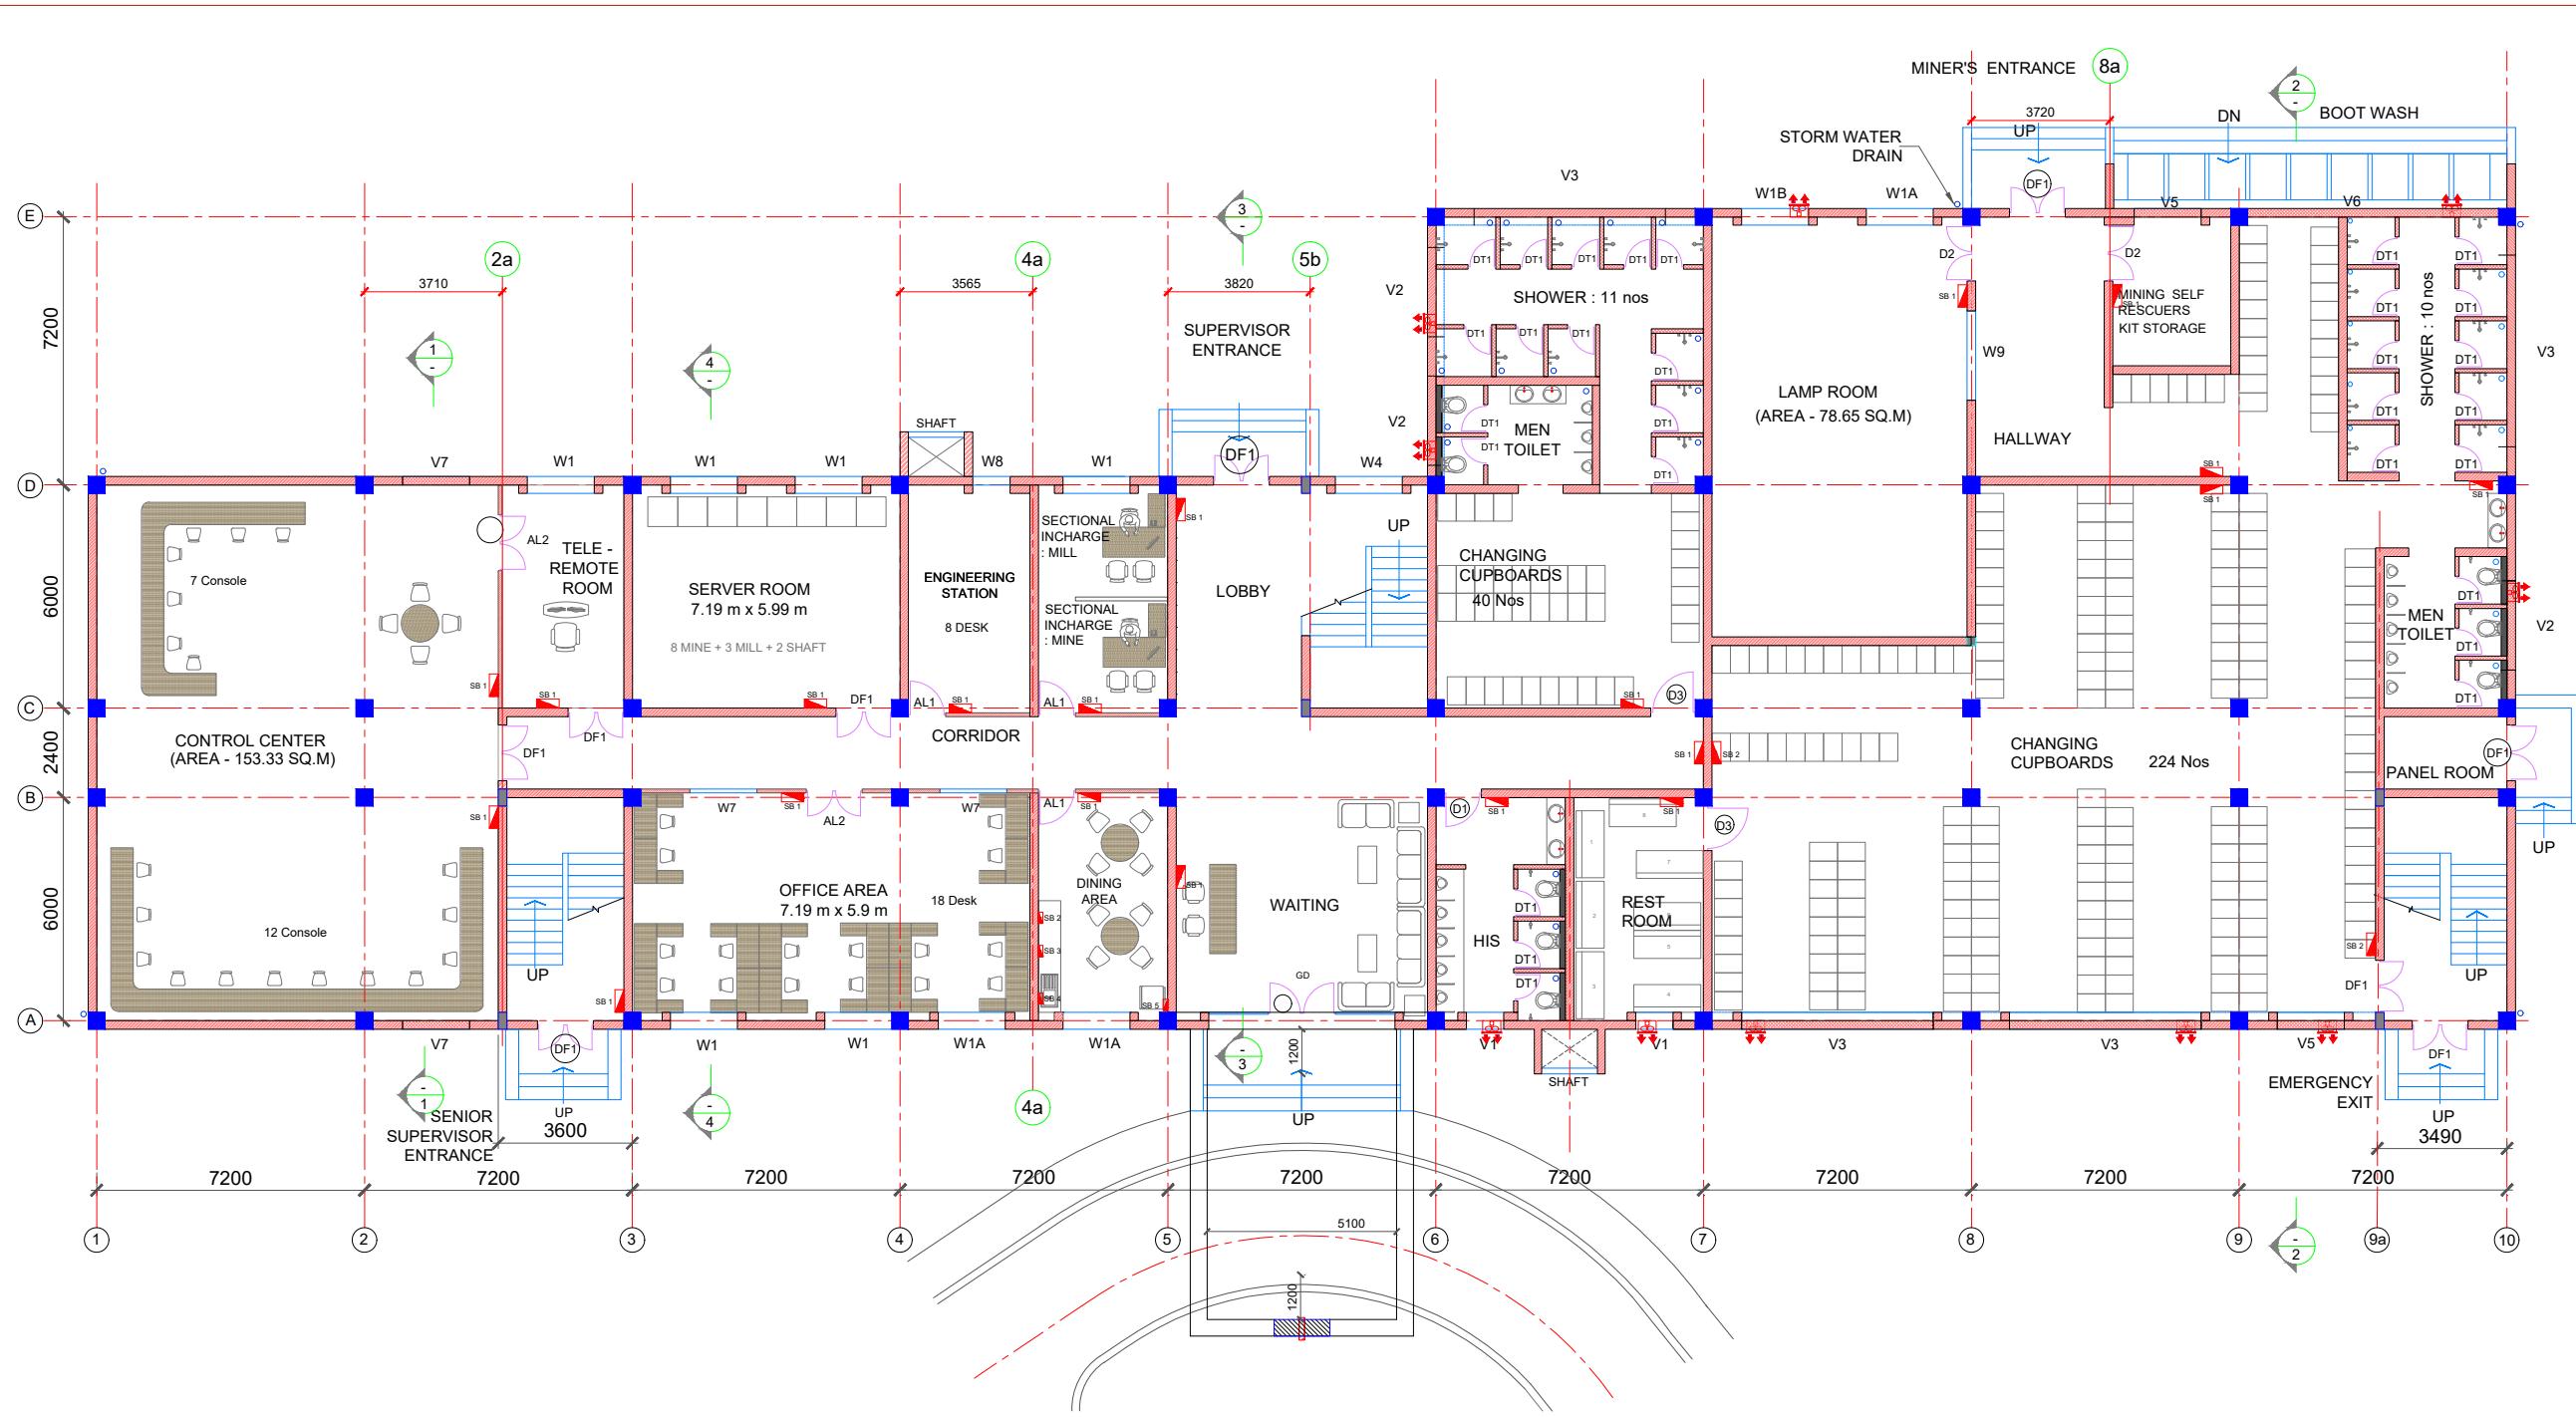


GROUND FLOOR PLAN + 0.00 M (FFL) / -0.10 M (TOC) U.N.O.

(SCALE 1:125)

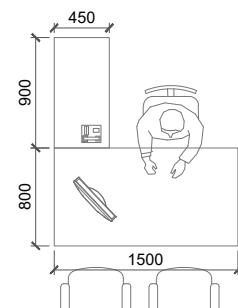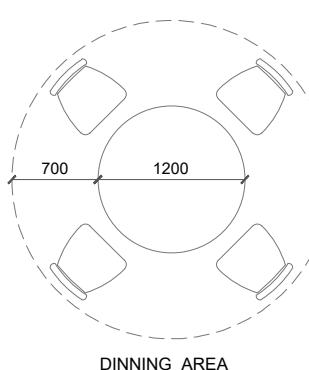

OFFICE AREA  
WORKSTATION : 01

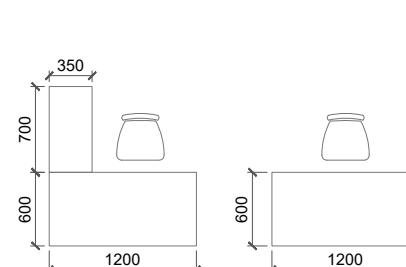

OFFICE AREA  
WORKSTATION : 02 SERVER / ENGINEERING  
WORKSTATION : 03

WINDOW SCHEDULE				
No	SILL	WIDTH	HEIGHT	DESCRIPTION
W1	1000	1800	2150	Aluminium Fixed Window
W1A	1000	1800	2150	Aluminium Sliding Window
W1B	1000	1800	2150	Aluminium Fixed / Exhaust
W2	1000	1800	1800	Aluminium Fixed Window
W2A	1000	1800	1800	Aluminium Sliding Window
W3	1000	1500	1800	Aluminium Sliding Window
W4	950	1800	1500	Aluminium Fixed Window
W4A	900	1800	1500	Aluminium Sliding Window
W7	1000	1800	1500	Aluminium Fixed Window
W8	1000	1000	2150	Aluminium Fixed Window
W9	1000	2400	2350	Aluminium Fixed Window

VENTILATOR SCHEDULE				
No	SILL	WIDTH	HEIGHT	DESCRIPTION
V1	1650	1000	1500	Aluminium Fixed Window - Louvers
V1A	1300	1000	1500	Aluminium Fixed Window - Louvers
V2	2400	2400	750	Aluminium Fixed Window
V3	2400	5150	750	Aluminium Fixed Window - Louvers
V4	1800	600	1000	Aluminium Fixed Window
V5	2400	1800	750	Aluminium Fixed Window - Louvers
V6	2400	6750	750	Aluminium Fixed Window - Louvers
V7	2400	1800	750	Aluminium Fixed Window

DOOR SCHEDULE			
No	WIDTH	HEIGHT	DESCRIPTION
D1	1000	2400	General Purpose Steel Door
D2	1500	2400	General Purpose Steel Door
D3	1200	2400	General Purpose Steel Door
DF1	1500	2400	Fire Rated HMPS Door
DT1	750	2100	General Purpose Metal Door
AL1	1000	2400	Aluminum Half Glazed Door
AL2	1500	2400	Aluminum Half Glazed Door
GD	1800	2400	Glass Door

